

CLEAR WIDTH (CW)	CLEAR HEIGHT (CH)	QUANTITY
3000	3500	1 NO

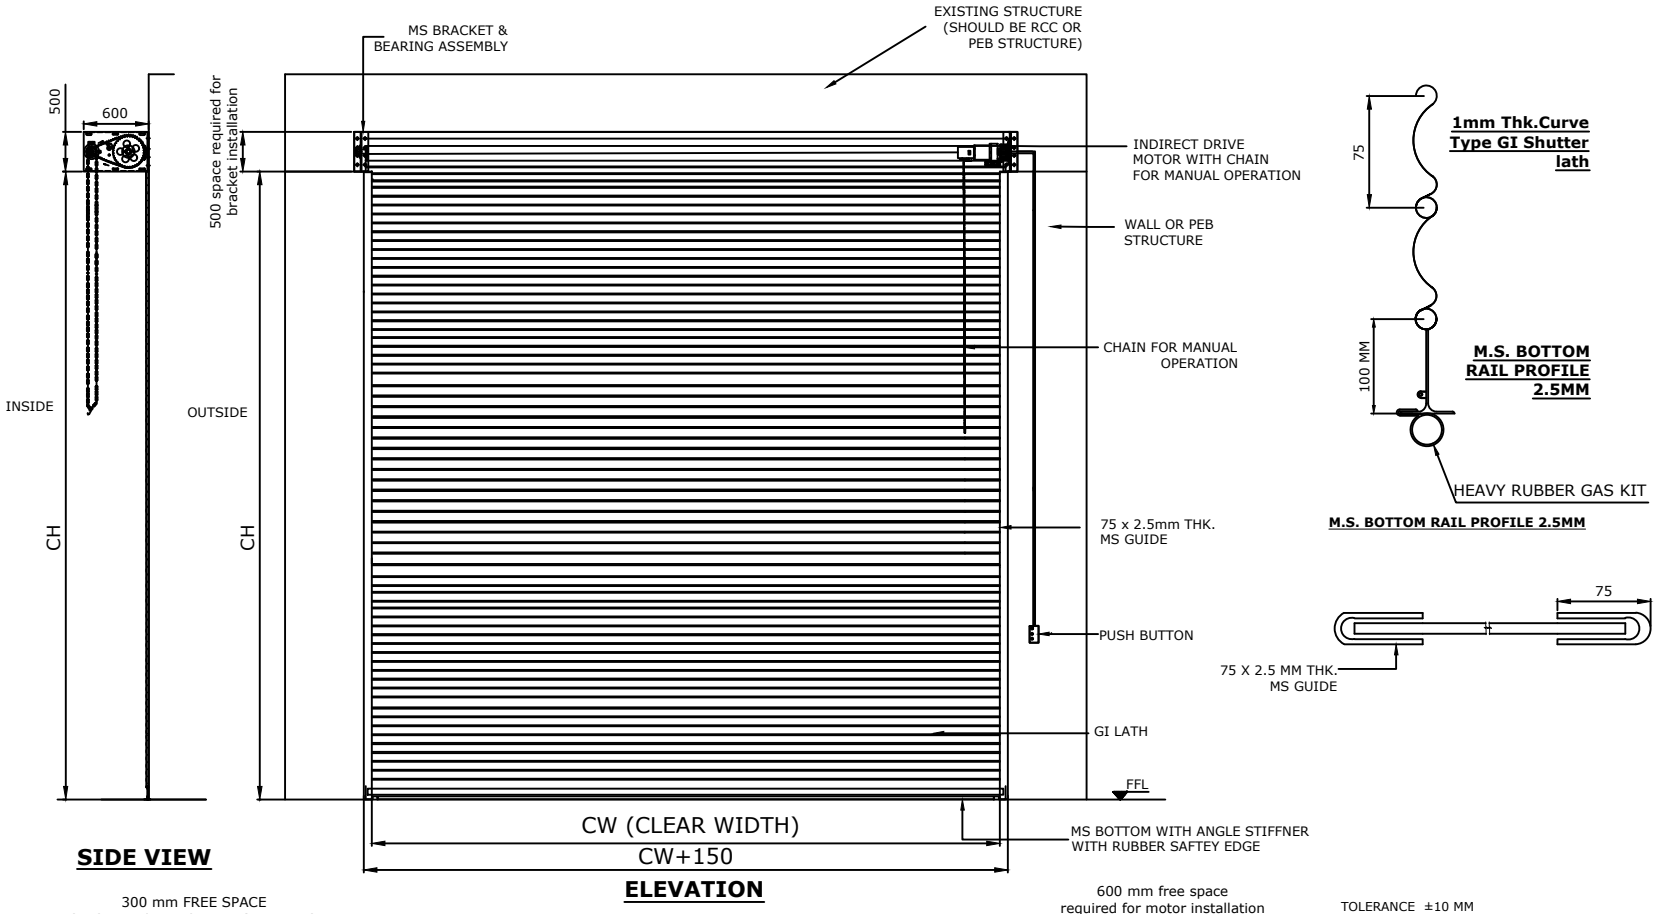

SIDE VIEW

ELEVATION

M.S. BOTTOM RAIL PROFILE 2.5MM

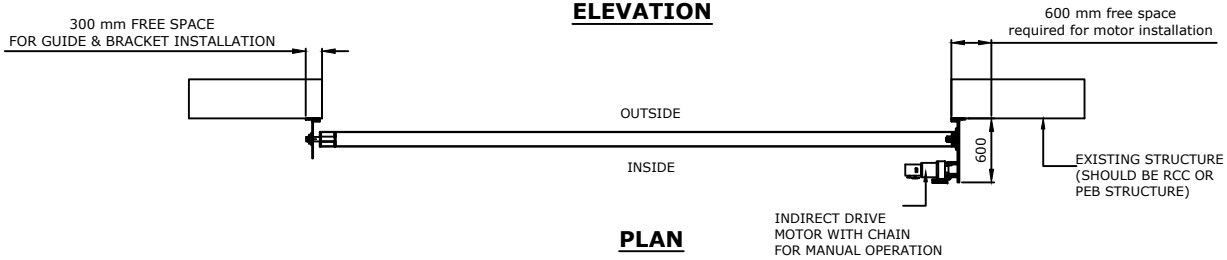

PLAN

TOLERANCE ±10 MM

This drawing & designing is the property of NIHVA TECHNOLOGIES. Not to be sold or copied to any other concern.

TITLE: MOTORIZED ROLLING SHUTTER

NIHVA TECHNOLOGIES PVT. LTD. PUNE
Tel : 020 66304033
Email:- info@nihva.com
Website:- www.nihva.com

	NAME		DATE
DRAWN	P.V.A		09.10.19
CHECK			
REV.			
APPROVAL			

CLIENT - GROUP SURYA
PROJECT - CUMMINS
SITE -
DWG. NO. : NIHVA/19-20/0115

If any queries contact : projects@nihva.com | SCALE: NTS | WT: | SHEET: 01 OF 01

ALL DIMENSION ARE IN mm