


Abbrevation's:
WOW-Wall Opening Width
WOH-Wall Opening Height
DH- Door Height
UC-Under Cut
FFL-Finished Floor Level

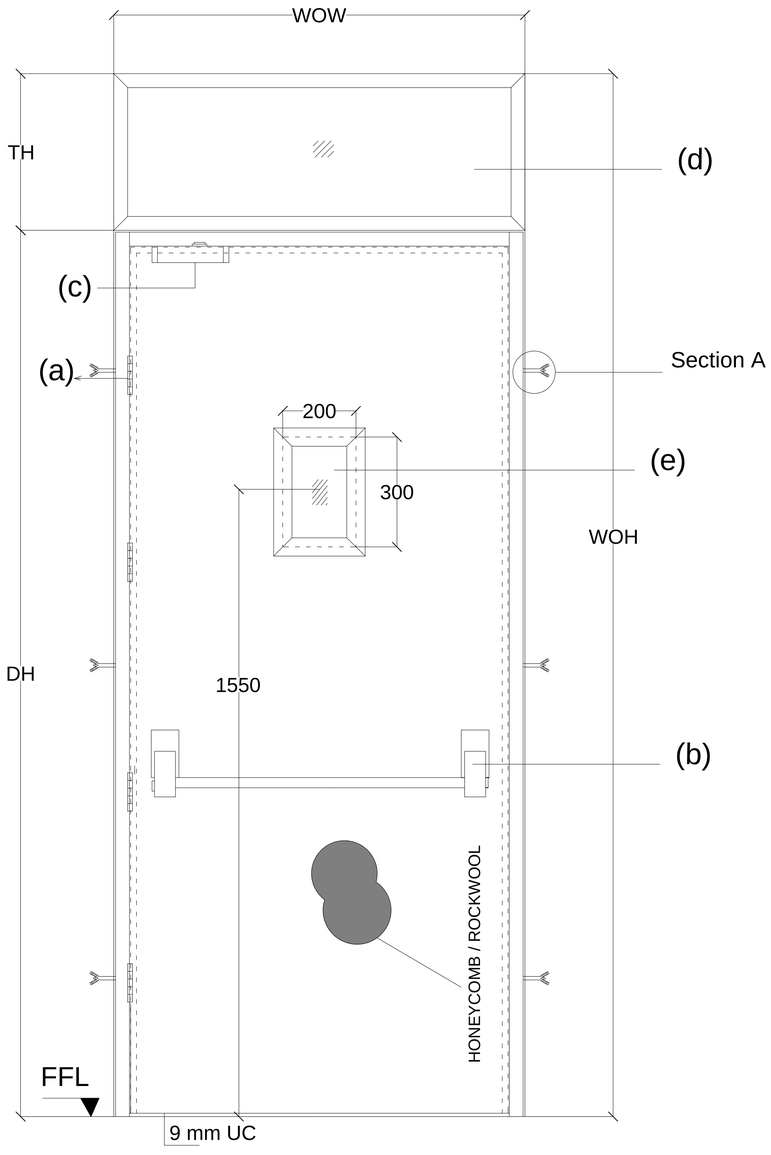

ELEVATION

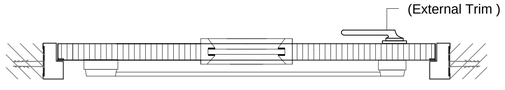

Top View

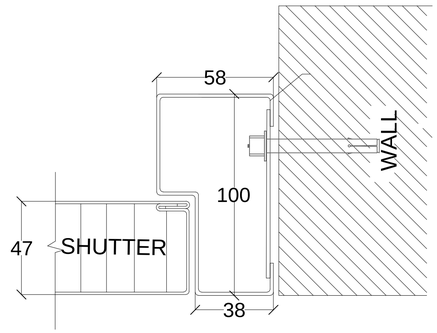

ASSESORIES DETALES

(a) HINGES: SS hinges 100x75x3mm

(b) LOCK : Mortise Lock with half cylinder.
Panic Bar
Outer trim

(c) DOOR CLOSER : F 8500

(d) FIXED GLASS(5mm THK.) WITH FRAME.

(e) VISION PANEL- 5mm THK. FIRE GLASS SIZE- 200X300mm.

Shutter thickness : 47 mm
Frame Sheet thick : 1.20mm
Shutter sheet thick : 0.80mm
Fixing : On Soliid Brick plasterd wall with Anchors

NOTE:- *All Dimensions are in mm.
*Tolerance:-All Linear Dimensions ±3mm,Others ±0.5mm.
*The Drawing Is For Location of Hardware only. Drawing Does Not Represent The Hardware For More Clarity, Please Go Through Hardware Broucher.

Fire door size

WOW	WOH	DH	TH	TYPE 1	TYPE 2	TYPE 3	TYPE 4	QUANTITY
1191	3000	2400	600					1
1180	3121	2400	721					1
1180	3029	2400	629					1
1195	3033	2400	633					1
1205	3017	2400	617					1
1194	2958	2400	558					1
1192	3000	2400	600					1

NOTE- CLIENT SHOULD SELECT DOOR TYPE FROM DOOR HANDLING SHEET & COLOR OF DOOR.

REVISION 1- UPPER VISION PANEL IS IN SINGLE PARTITION AS PER CLIENT'S REQUIREMENT.

This drawing & designing is the property of NIHVA TECHNOLOGIES. Not to be sold or copied to any other concern.

TITLE			
FIRE RATED DOORS WITH FIXED GLASS			NIHVA TECHNOLOGIES PVT. LTD. PUNE Tel : 020 66304033 Email:- info@nihva.com Website:- www.nihva.com
	SIGN	DATE	
DRAWN	OMKAR	19/07/17	CLIENT - VAICHAL CONSTRUCTION
CHECK	SHEKHAR	19/07/17	PROJECT - TAGMA CENTRE
REV.	00		SITE - CHAKAN
APPROVAL			DWG. NO. : NIHVA/17-18/0128/R01
If any queries contact : projects@nihva.com			SCALE: NTS | WT: | SHEET: 01 OF 01
ALL DIMENSION ARE IN mm			