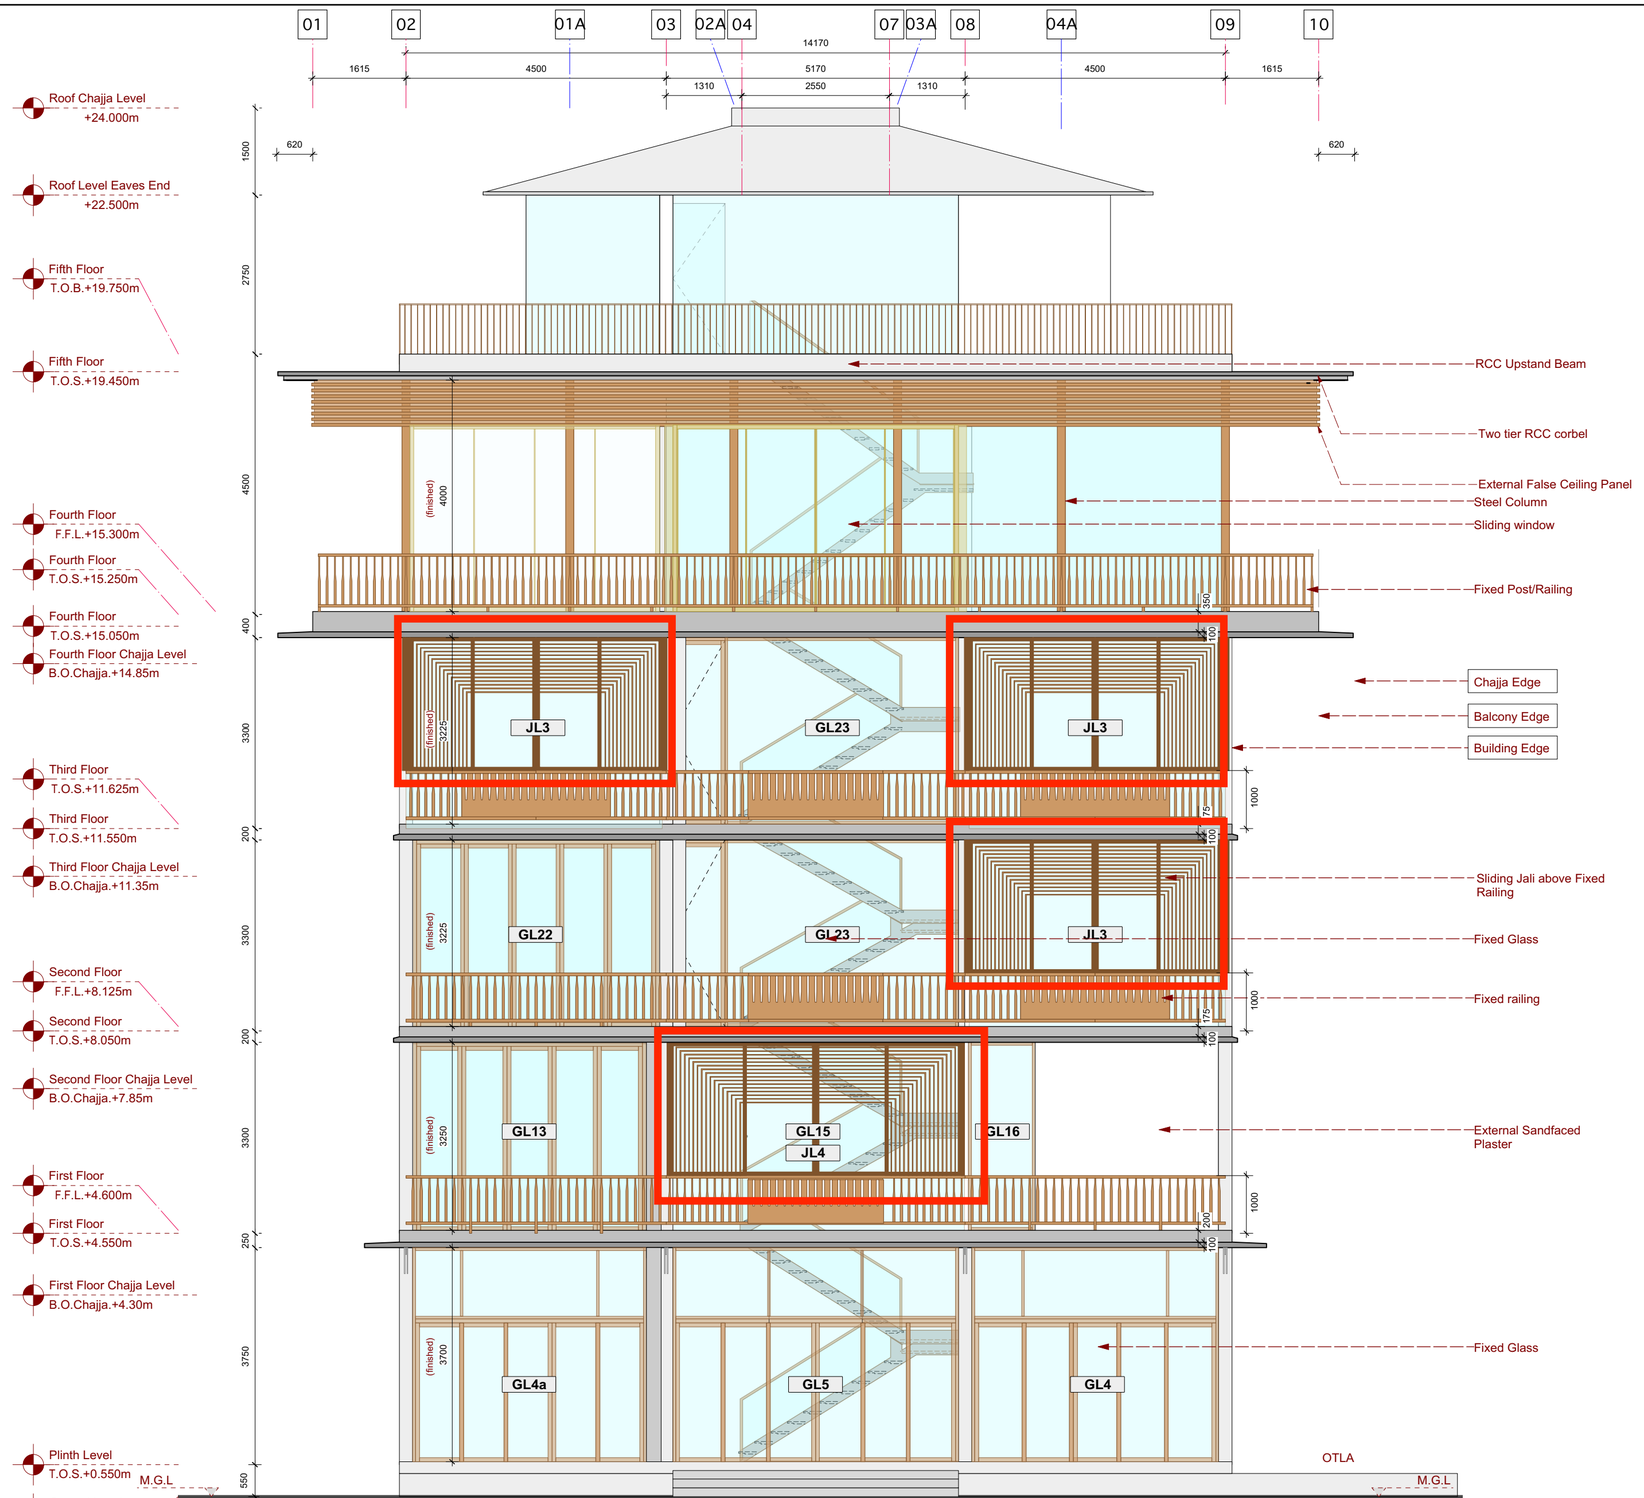


NORTH ELEVATION

ARCHITECT:

SJK ARCHITECTS

302-303,VEENA KILLEDAR INDL.EST.
,10/14,PAIS STREET, BYCULLA-WEST,
MUMBAI-400 011
TEL.NO.: 022- 2300 8766, 022-23008761
FAX.NO. : 022-2309 0983
email: design @sjkarchitect.com

This "drawing" is the copyright of **SJK Architects** and shall not be used for any purpose other than that for which it has been loaned.

STRUCTURAL:

MANJUNATH & CO.
CONSULTING ENGINEERS
#236 5th CROSS,
K.G. NAGAR,
BANGALORE - 560019
TEL.NO.: 080- 26616610
email:
manjaxe2010@gmail.com

MEP:

MEPTEK CONSULTANTS

-2;665, Millennium, Veer Savarkar Marg,
Dadar (W),
Mumbai-400028.
nimish.shah@meptekconsultants.com

PMC:

GENERAL NOTES:

1. All Dimensions Are In MILLIMETERS Unless Otherwise Specified.
2. All Dimensions Specified Are UnFinished Dimensions, Unless Otherwise specified.
3. All structural dimensions shall be referred as per Consultants' drawings.
4. DO NOT SCALE Drawing
5. Any Discrepancies In the Drawings Shall Be Brought To The Notice Of The Architect,Prior to Execution.

SPECIFIC NOTES / LEGEND:

1. All Boxed Dimensions are finished dimensions (i.e. after plaster, dado etc). Remaining are unfinished dimensions.
2. All External surfaces of walls shall have 20mm thk External Sandfaced Plaster.
3. All Internal surfaces of walls shall have 12mm thk Backing Coat of Plaster + POP Punning. (Except toilet walls, which will receive waterproofing and dado finish).

KEY PLAN

REVISION NOTES:

PROJECT:

NAGPUR HOUSE

CLIENT:

JAIN FAMILY

REV NO: R1
DATE OF REVISION:

DRAWING NO: NH-DD-ELE-003-R1


DRAWING TITLE:

NORTH ELEVATION

DATE OF ISSUE: 26-02-2020

SCALE: 1:75 **SHEET SIZE:** A2

PURPOSE :

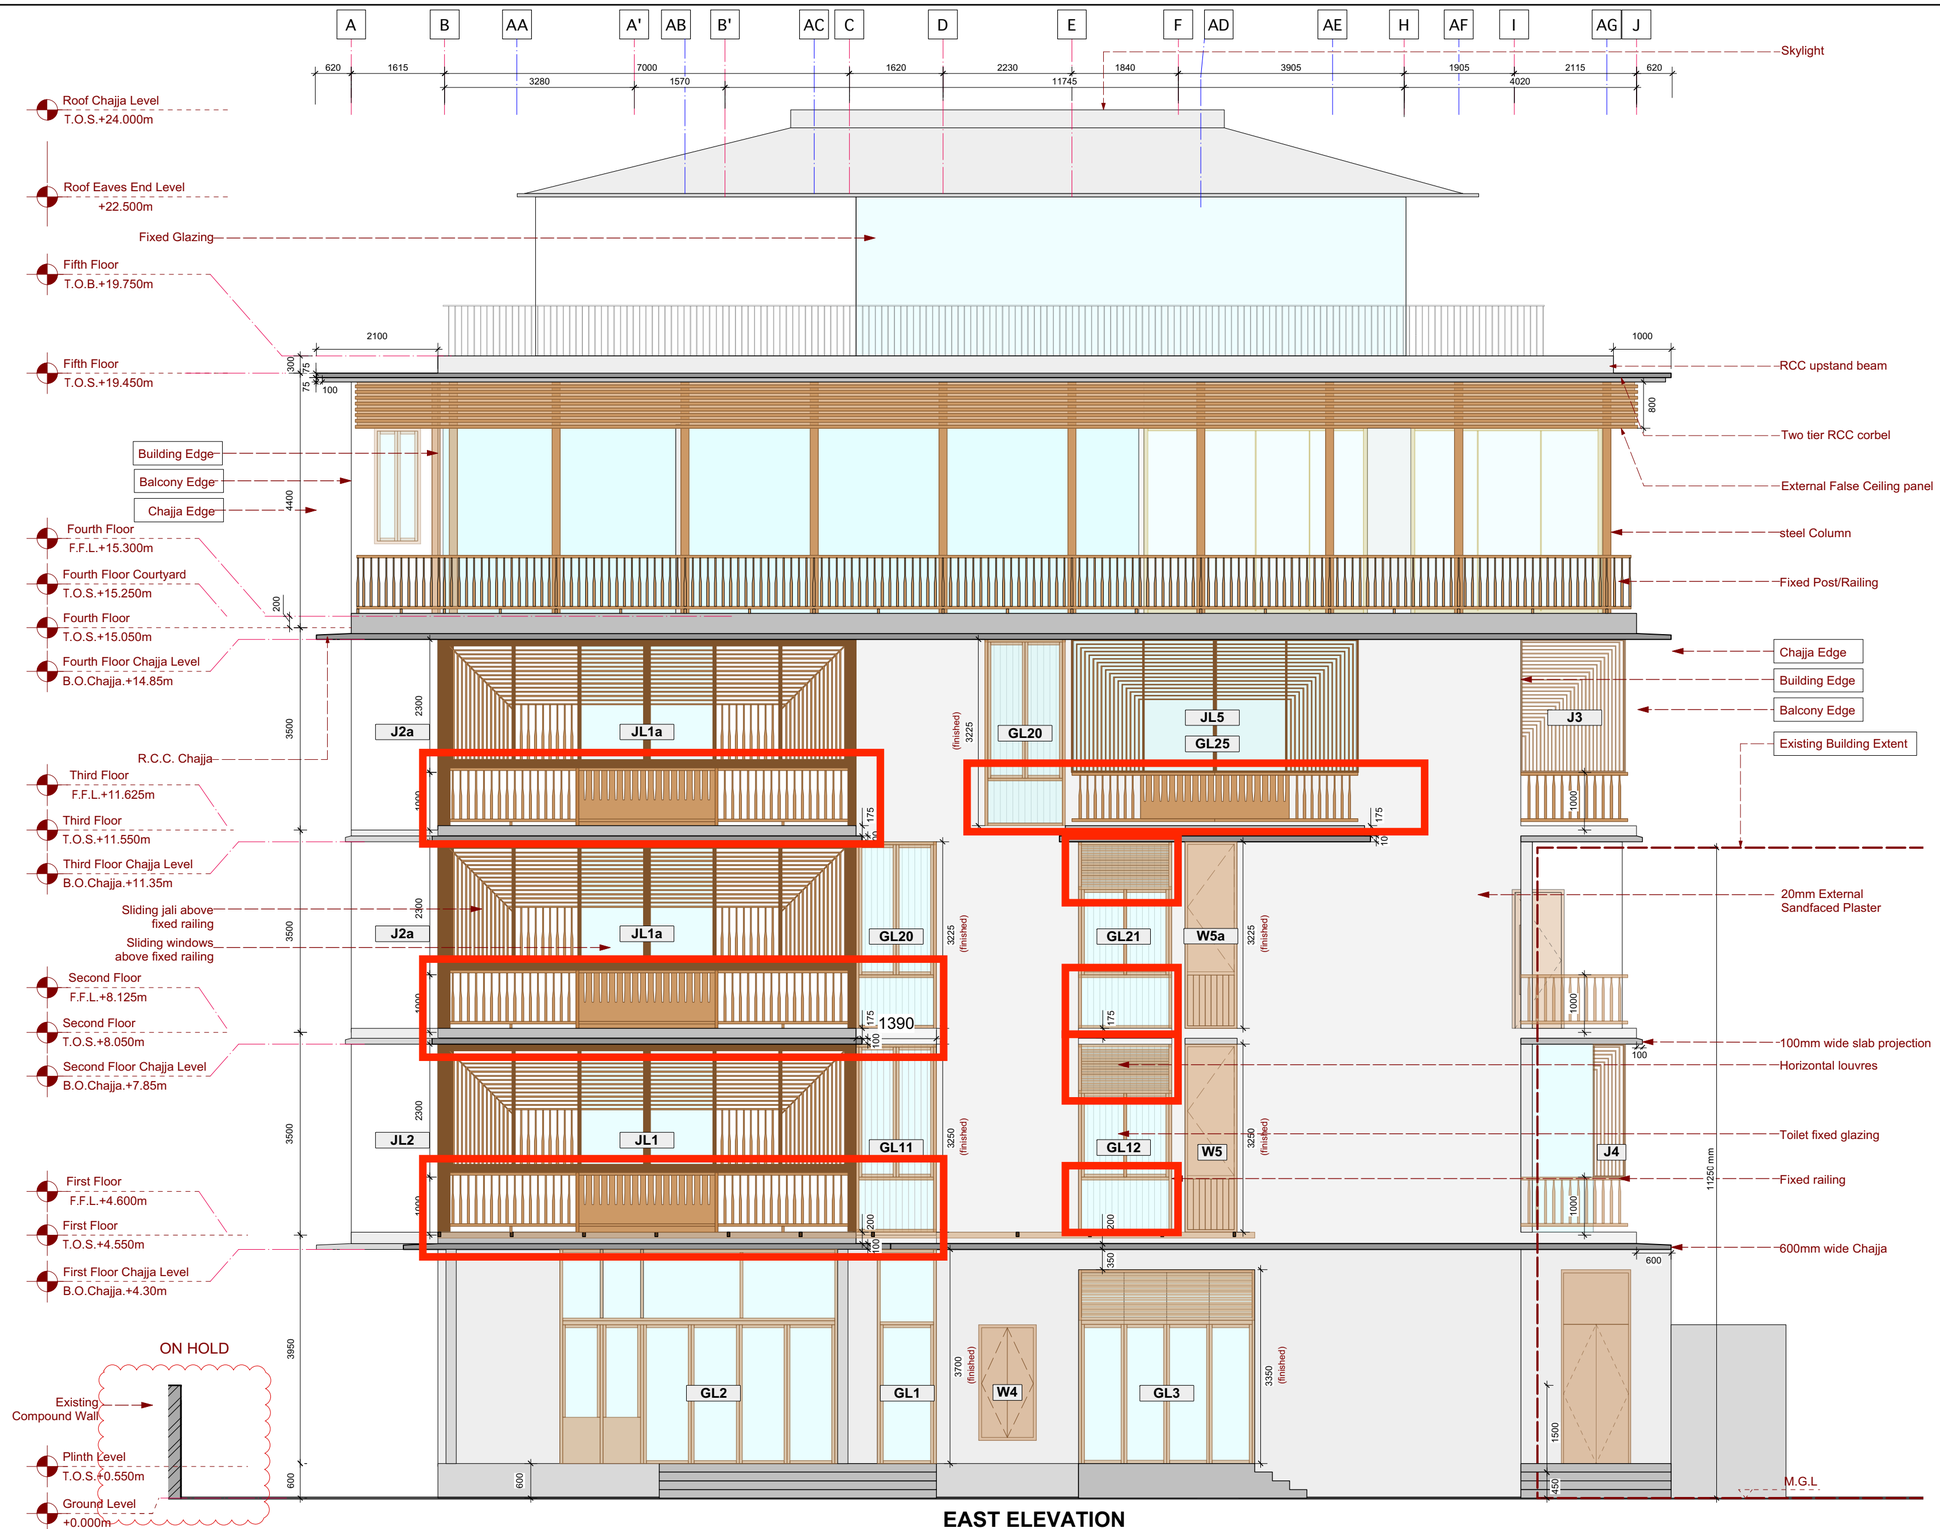

EAST ELEVATION

ARCHITECT: SJK ARCHITECTS 302-303,VEENA KILLEDAR INDL.EST. ,10/14,PAIS STREET, BYCULLA-WEST, MUMBAI-400 011 TEL.NO.: 022- 2300 8766, 022-23008761 FAX.NO. : 022-2309 0983 email: design @sjkarchitect.com	**STRUCTURAL:** MANJUNATH & CO. CONSULTING ENGINEERS #236 5th CROSS, K.G. NAGAR, BANGALORE - 560019 TEL.NO.: 080- 26616610 email: manjaxe2010@gmail.com	**MEP:** MEPTEK CONSULTANTS -2;665, Millennium, Veer Savarkar Marg, Dadar (W), Mumbai-400028. nimish.shah@meptekconsultants.com	**PMC:**

This "drawing" is the copyright of **SJK Architects** and shall not be used for any purpose other than that for which it has been loaned.

GENERAL NOTES:

1. All Dimensions Are In MILLIMETERS Unless Otherwise Specified.
2. All Dimensions Specified Are UnFinished Dimensions, Unless Otherwise specified.
3. All structural dimensions shall be referred as per Consultants' drawings.
4. DO NOT SCALE Drawing
5. Any Discrepancies In the Drawings Shall Be Brought To The Notice Of The Architect,Prior to Execution.

SPECIFIC NOTES / LEGEND:

1. All Boxed Dimensions are finished dimensions (i.e. after plaster, dado etc). Remaining are unfinished dimensions.
2. All External surfaces of walls shall have 20mm thk External Sandfaced Plaster.
3. All Internal surfaces of walls shall have 12mm thk Backing Coat of Plaster + POP Punning. (Except toilet walls, which will receive waterproofing and dado finish).

KEY PLAN


REVISION NOTES:

REV NO: R0
DATE OF REVISION:

PROJECT:
NAGPUR HOUSE

CLIENT:
JAIN FAMILY

DRAWING NO: NH-DD-SEC-001-R0
DRAWING TITLE:
SECTION 2-2
DATE OF ISSUE: 26-02-2020
SCALE: 1:75 **SHEET SIZE:** A2
PURPOSE :

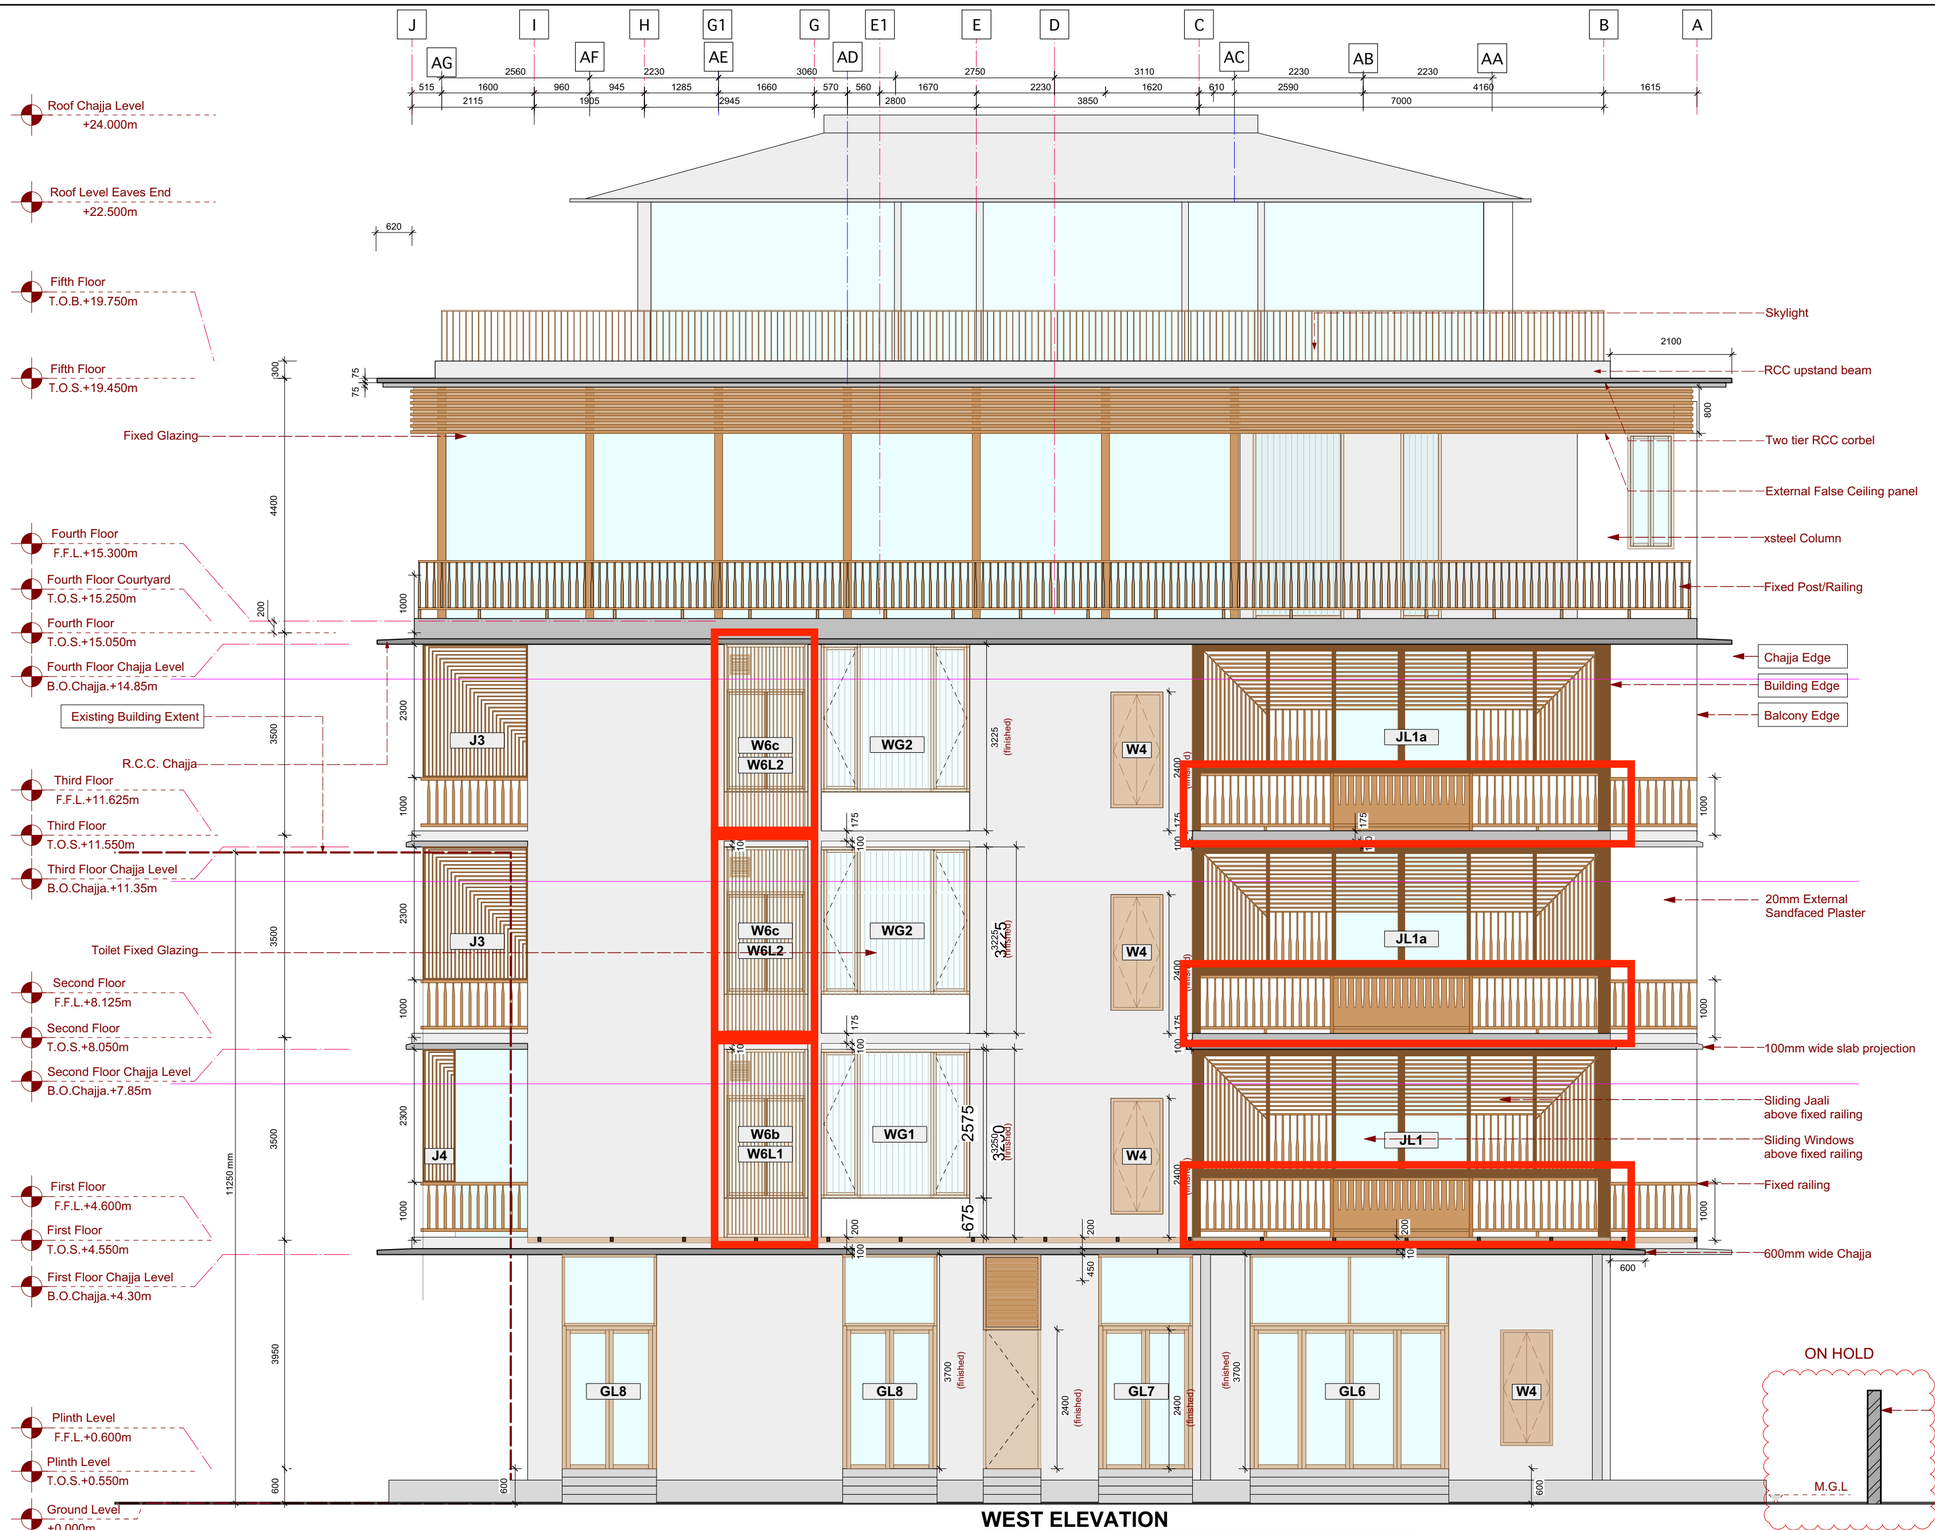

WEST ELEVATION

ARCHITECT:

SJK ARCHITECTS

302-303,VEENA KILLEDAR INDL.EST.
,10/14,PAIS STREET, BYCULLA-WEST,
MUMBAI-400 011
TEL.NO.: 022- 2300 8766, 022-23008761
FAX.NO. : 022-2309 0983
email: design @sjkarchitect.com

This "drawing" is the copyright of **SJK Architects** and shall not be used for any purpose other than that for which it has been loaned.

STRUCTURAL:

MANJUNATH & CO.
CONSULTING ENGINEERS
#236 5th CROSS,
K.G. NAGAR,
BANGALORE - 560019
TEL.NO. : 080- 26616610
email:
manjaxe2010@gmail.com

MEP:

MEPTEK CONSULTANTS
Complete MEP Design Solutions

-2;665, Millennium, Veer
Savarkar Marg,
Dadar (W),
Mumbai-400028.
nimish.shah@meptekcons
ultants.com

PMC:

GENERAL NOTES:

1. All Dimensions Are In MILLIMETERS Unless Otherwise Specified.
2. All Dimensions Specified Are UnFinished Dimensions, Unless Otherwise specified.
3. All structural dimensions shall be referred as per Consultants' drawings.
4. DO NOT SCALE Drawing
5. Any Discrepancies In the Drawings Shall Be Brought To The Notice Of The Architect,Prior to Execution.

SPECIFIC NOTES / LEGEND:

1. All Boxed Dimensions are finished dimensions (i.e. after plaster, dado etc). Remaining are unfinished dimensions.
2. All External surfaces of walls shall have 20mm thk External Sandfaced Plaster.
3. All Internal surfaces of walls shall have 12mm thk Backing Coat of Plaster + POP Punning. (Except toilet walls, which will receive waterproofing and dado finish).

KEY PLAN

REVISION NOTES:

REV NO: R0
DATE OF REVISION:

PROJECT:

NAGPUR HOUSE

CLIENT:

JAIN FAMILY

DRAWING NO: NH-DD-SEC-001-R0


DRAWING TITLE:

SECTION 5a-5a

DATE OF ISSUE: 26-02-2020

SCALE: 1:75 **SHEET SIZE:** A2

PURPOSE :

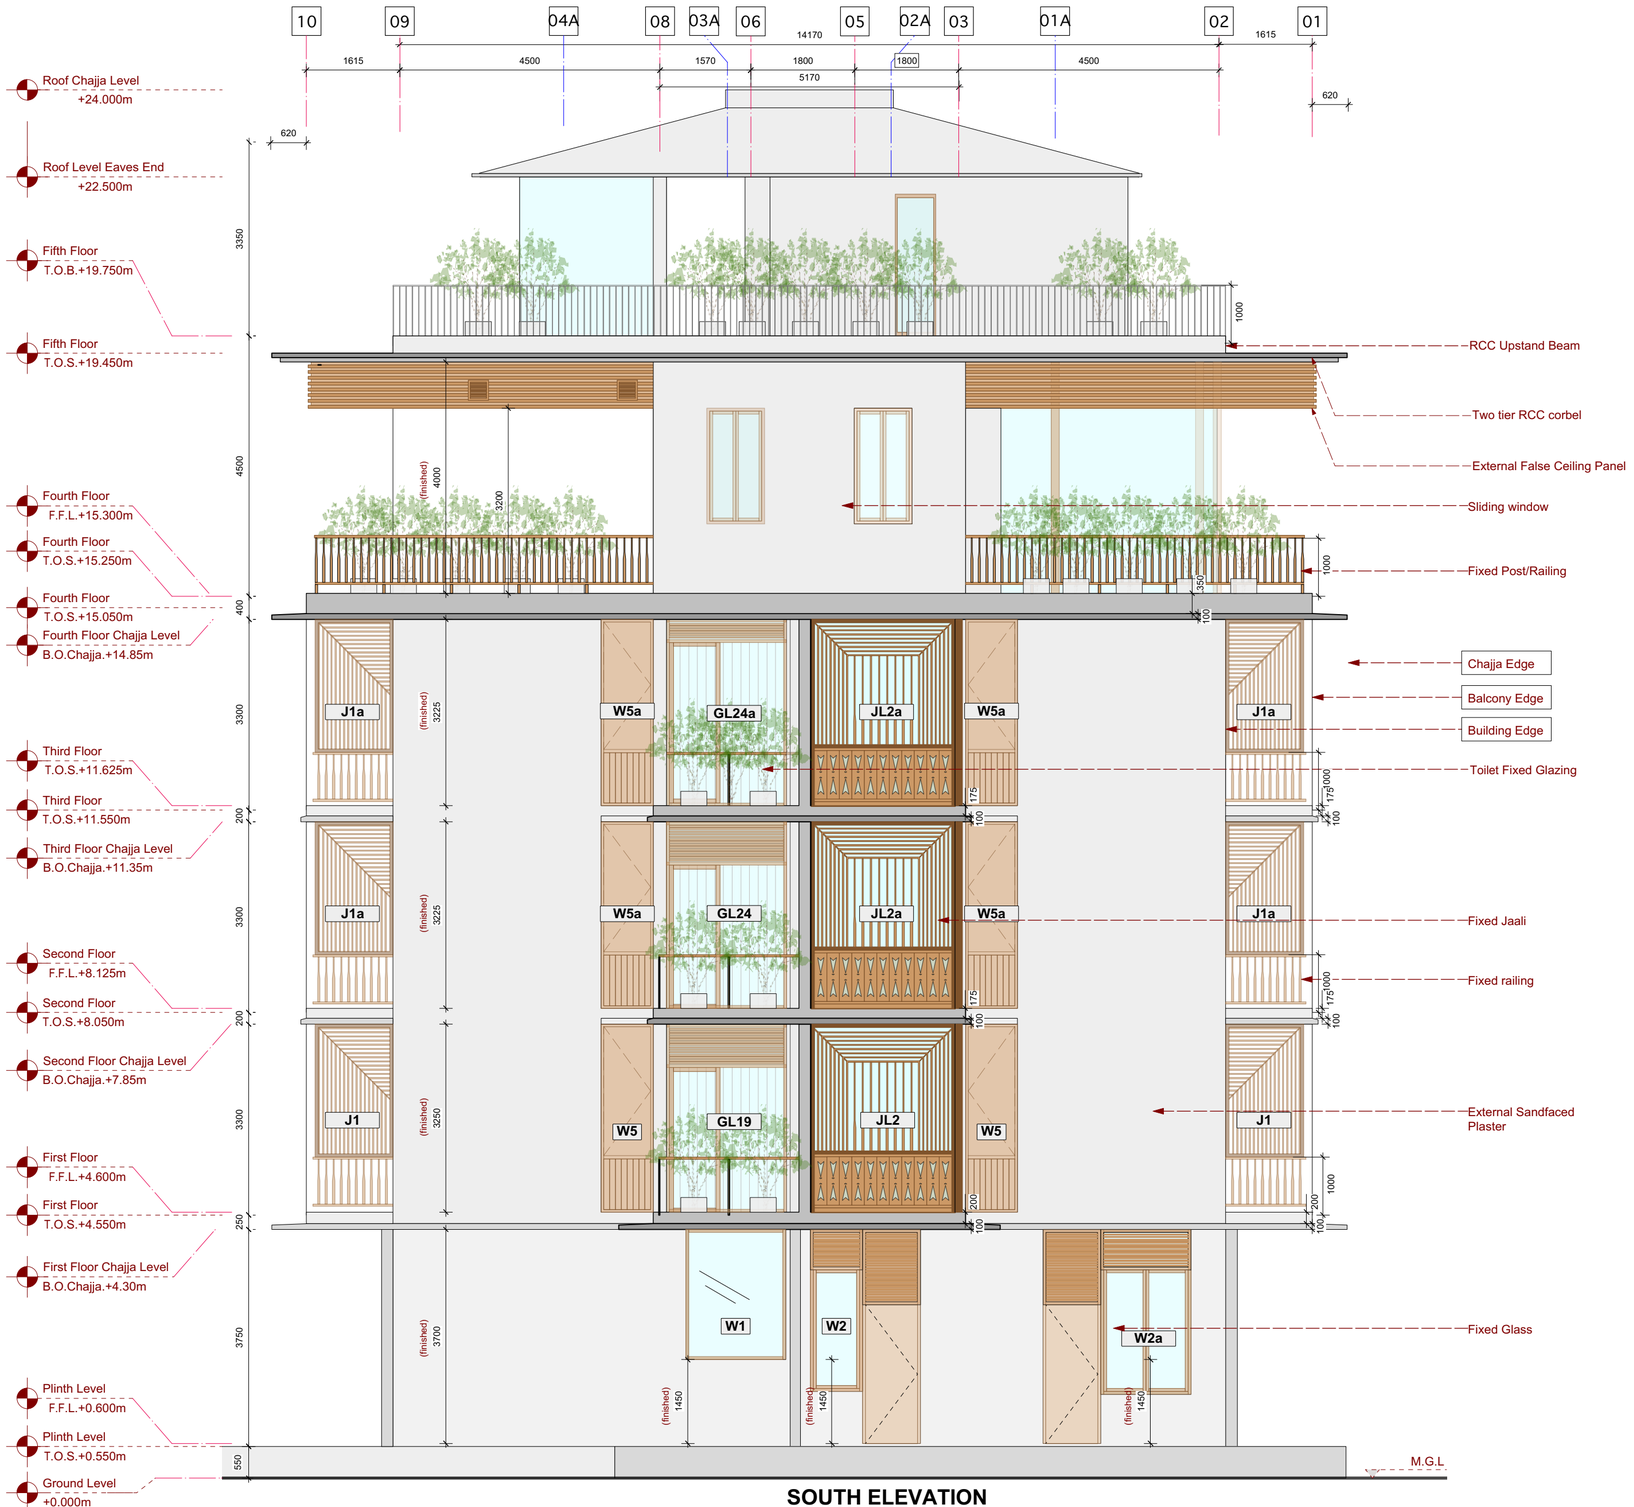

SOUTH ELEVATION

ARCHITECT:

SJK ARCHITECTS

302-303,VEENA KILLEDAR INDL.EST.
,10/14,PAIS STREET, BYCULLA-WEST,
MUMBAI-400 011
TEL.NO.: 022- 2300 8766, 022-23008761
FAX.NO. : 022-2309 0983
email: design @sjkarchitect.com

This "drawing" is the copyright of **SJK Architects** and shall not be used for any purpose other than that for which it has been loaned.

STRUCTURAL:

MANJUNATH & CO.
CONSULTING ENGINEERS
#236 5th CROSS,
K.G. NAGAR,
BANGALORE - 560019
TEL.NO. : 080- 26616610
email:
manjaxe2010@gmail.com

MEP:

MEPTEK CONSULTANTS

-2;665, Millennium, Veer Savarkar Marg,
Dadar (W),
Mumbai-400028.
nimish.shah@meptekconsultants.com

PMC:

GENERAL NOTES:

1. All Dimensions Are In MILLIMETERS Unless Otherwise Specified.
2. All Dimensions Specified Are UnFinished Dimensions, Unless Otherwise specified.
3. All structural dimensions shall be referred as per Consultants' drawings.
4. DO NOT SCALE Drawing
5. Any Discrepancies In the Drawings Shall Be Brought To The Notice Of The Architect,Prior to Execution.

SPECIFIC NOTES / LEGEND:

1. All Boxed Dimensions are finished dimensions (i.e. after plaster, dado etc). Remaining are unfinished dimensions.
2. All External surfaces of walls shall have 20mm thk External Sandfaced Plaster.
3. All Internal surfaces of walls shall have 12mm thk Backing Coat of Plaster + POP Punning. (Except toilet walls, which will receive waterproofing and dado finish).

KEY PLAN

REVISION NOTES:

PROJECT:

NAGPUR HOUSE

CLIENT:

JAIN FAMILY

REV NO: R1
DATE OF REVISION:

DRAWING NO: NH-DD-ELE-003-R1

DRAWING TITLE:

NORTH ELEVATION

DATE OF ISSUE: 26-02-2020

SCALE: 1:75 **SHEET SIZE:** A2

PURPOSE :