





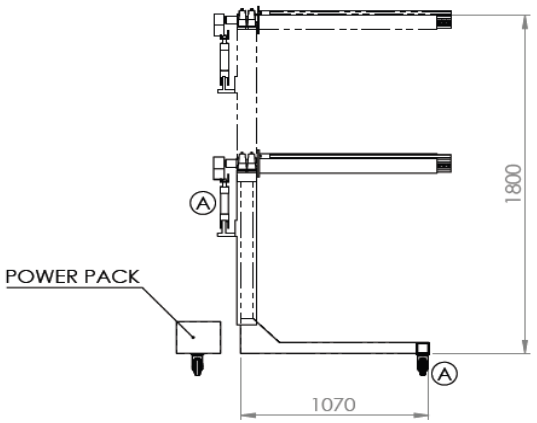

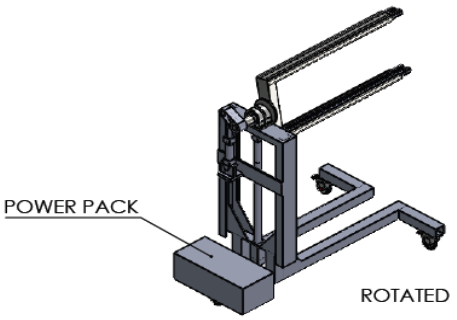

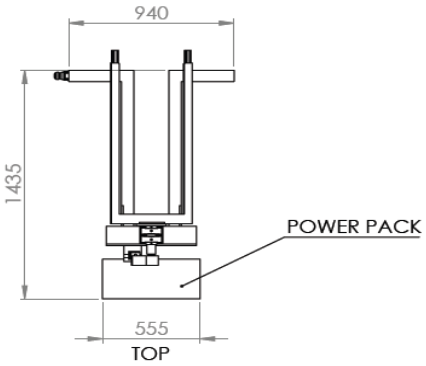

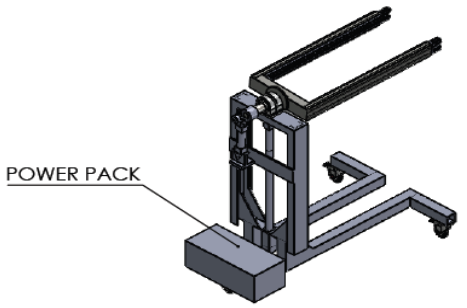

D4, E5, E7	A	WHEELS ADDED; CYLINDER FOR ROTATION IS AN OPTIONAL CHOICE	11-11-2017	
ZONE	REV.	DESCRIPTION	DATE	APPROVED
REVISIONS				

UNLESS OTHERWISE SPECIFIED:
DIMENSIONS ARE IN MILLIMETERS
SURFACE FINISH:
TOLERANCES:
LINEAR:
ANGULAR:

FINISH:

DEBURR AND BREAK SHARP EDGES

DO NOT SCALE DRAWING | REVISION A

NIHVA TECHNOLOGIES PVT LTD
Email:-info@nihva.com
Website:-www.nihva.com

	NAME	SIGNATURE	DATE
DRAWN	SURAJ		
CHK'D	VIKRANT		
APPV'D	SHEKHAR		
MFG	BIPLOB		
Q.A			

TITLE: TRAY LIFTER AND TILTER

MATERIAL: MILD STEEL

WEIGHT: GMS

DWG NO. 17035-CD-01

A3

SCALE:1:25 | SHEET 1 OF 1

SHEKHAR SHINDE MAYUR DERLE VIKAS DESHPANDE

17035-NESTLE LIFTER AND TILTER

BOM FOR TRAY LIFTER AND TILTER						
SS MATERIAL		by 350/Kg	Lifter & Tilter		Only Lifter	
	Structure All	172.08726	₹	60,230.54	₹	60,230.54
					₹	-
	~~MS Material~~	~~by 140/Kg~~			₹	-
		0	₹	-	₹	-
					₹	-
	Castor Wheel	3	₹	3,000.00	₹	3,000.00
					₹	-
Hydraulic					₹	-
	dia 40 x 200	1	₹	4,000.00	₹	-
	dia 40 x 900	1	₹	30,000.00	₹	30,000.00
	PowerPack	1	₹	30,000.00	₹	30,000.00
	UCUP Bearing (UCUP210D1(50,D1))	2	₹	24,000.00	₹	-
	UHMW 50X10 2M	2	₹	1,000.00	₹	1,000.00
~~Elsa~~	~~Elsa Ganter 614 Track 1m~~	~~4~~	~~₹~~	~~———~~	~~₹~~	~~———~~
	Elsa Ganter 812 Knob	2	₹	4,000.00	₹	4,000.00
					₹	-
	Painting 10%		₹	15,623.05	₹	12,823.05
	Misc 20%		₹	34,370.72	₹	28,210.72
		Total	₹	2,06,224.31	₹	1,69,264.31
		Round up	**₹**	**2,10,000.00**	**₹**	**1,70,000.00**

SHEKHAR SHINDE MAYUR DERLE VIKAS DESHPANDE