
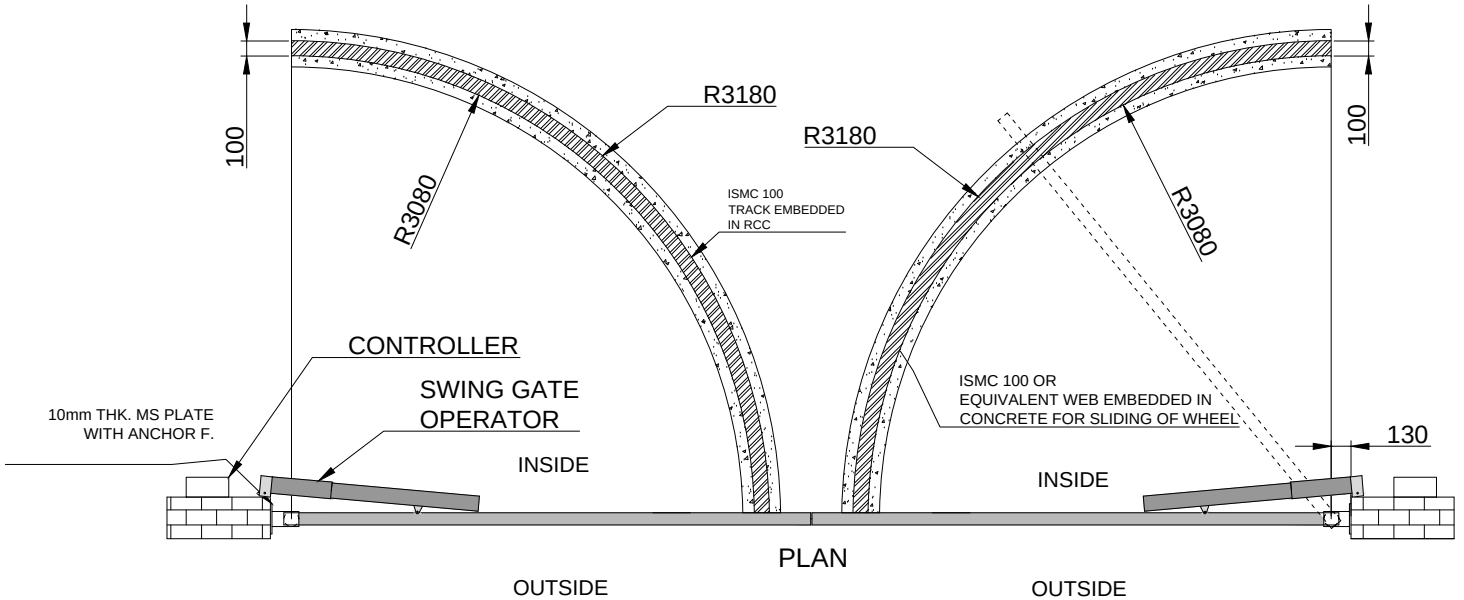


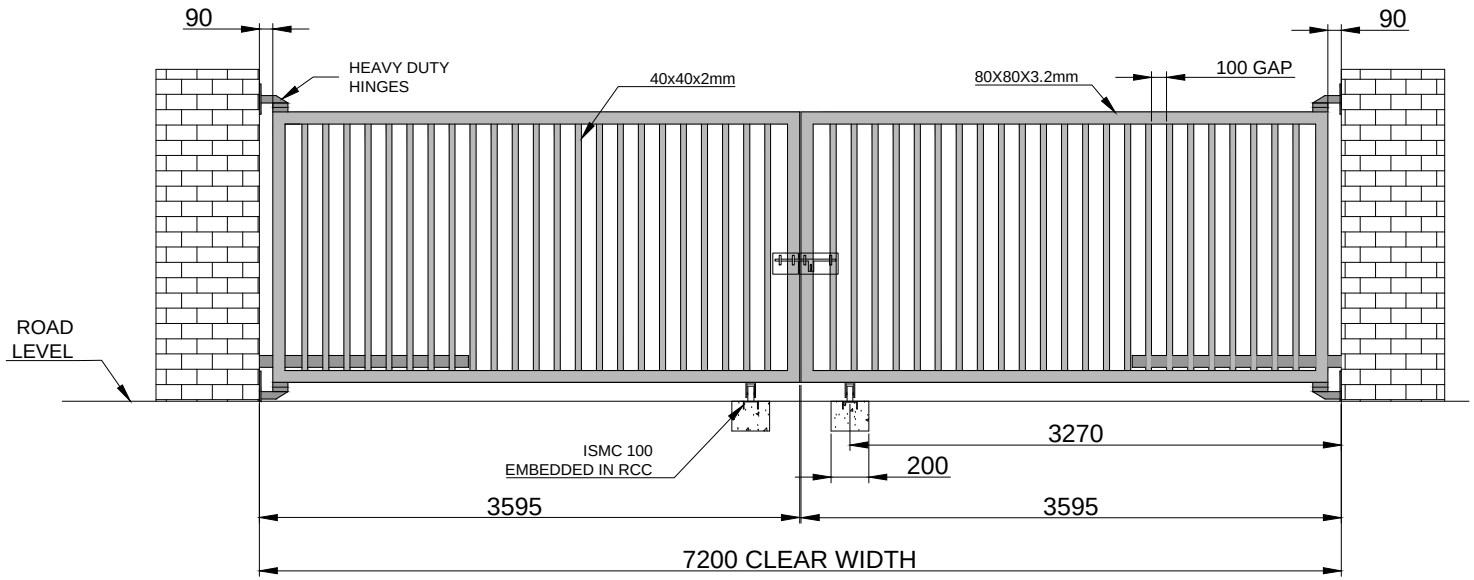

ELEVATION

REV 1(25-04-2018) - OPERATION OF GATE CHANGED FROM MANUAL TO MOTORIZED.

TOLERANCE- ±10mm

DIMENSION :

CLEAR WIDTH	CLEAR HEIGHT	QUANTITY
7200mm	1800mm	1 NOS

MATERIAL:

SR NO	TUBE SPECIFICATION	
1	MS 80X80X3.2mm	OUTER FRAME
2	MS 40X40X2mm	INNER PATTERN

THICKNESS :

NOTE-
1. ALL REQUIRED CIVIL WORK WILL BE IN CLIENTS SCOPE.
2. ONE COAT OF RED OXIDE & TWO COAT OF APPROVED RAL SHADE WILL BE GIVEN TO THE GATE.

NIHVA
NIHVA TECHNOLOGIES PVT. LTD.
NIHVA TECHNOLOGIES PVT. LTD. PUNE
Email:- info@nihva.com
Website:- www.nihva.com

TITLE:

AUTOMATIC SWING GATE
7.2X1.8m GATE NO 7

CLIENT'S APPROVAL :

CLIENT - TATA PROJECT

PROJECT - ALSTOM

SITE LOCATION -MADHEPURA,BIHAR

DWG. NO. : NIHVA/17-18/0081/R01	REV - 01
SCALE: NTS	WT:	SHEET:1 OF 1
DRAWN BY: SURAJ	DATE: 17-05-2017
CHECK BY : SAGAR P	DATE: 17-05-2017
APPROVED BY : S.S	DATE: 17-05-2017

If any queries contact : projects@nihva.com

NOTE: ALL DIMENSIONS ARE IN mm

THIS DRAWING & DESIGN IS THE PROPERTY OF NIHVA TECHNOLOGIES. NOT TO BE SOLD OR COPIED TO ANY OTHER CONCERN.