


DWG.NO: SALT_1729_STR_03_R0

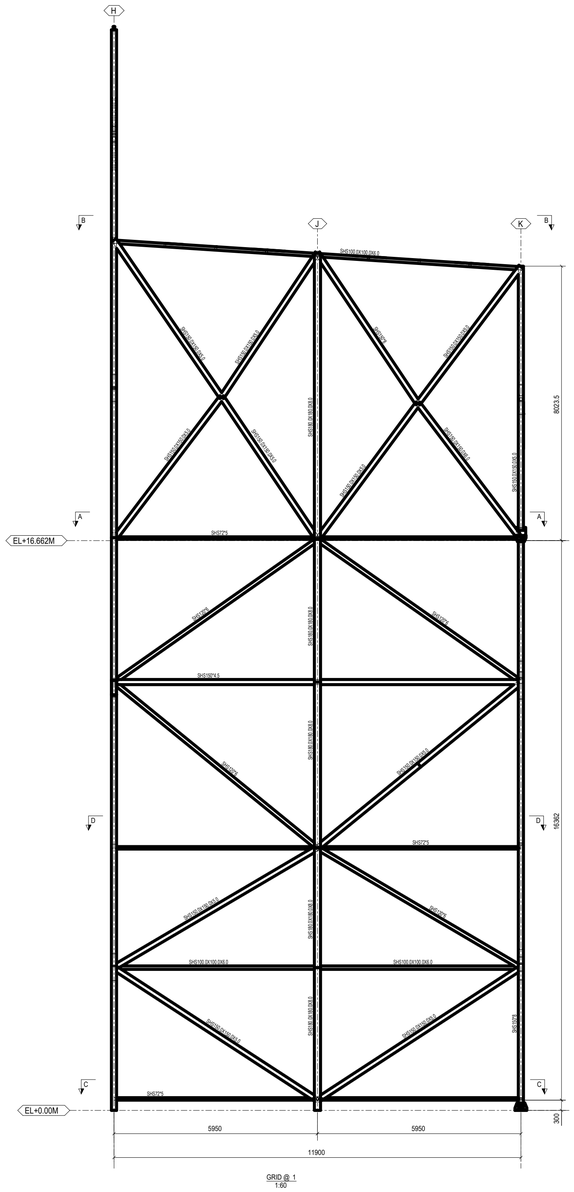


GRID @ 1
1:60

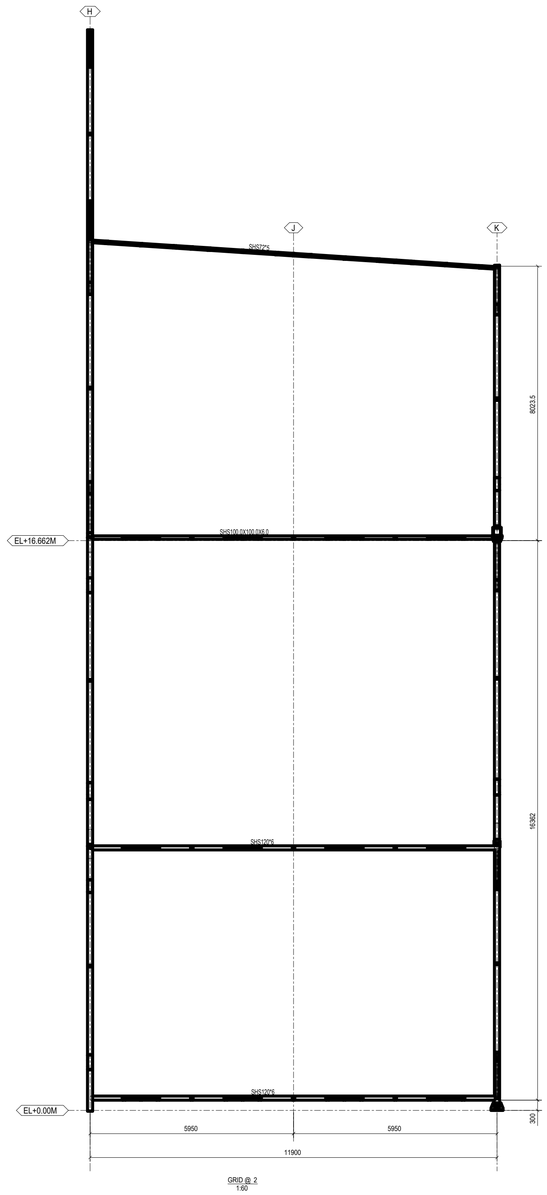


GRID @ 2
1:60

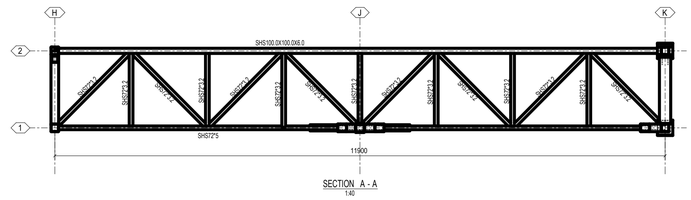


SECTION A - A
1:40

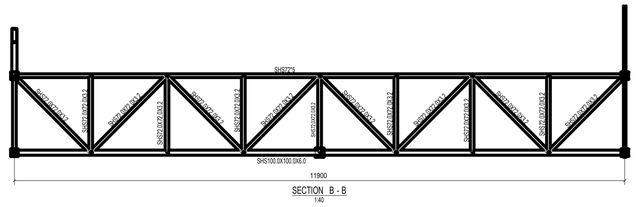

SECTION B - B
1:40

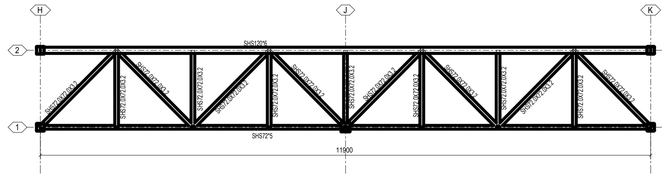

SECTION C - C
1:40

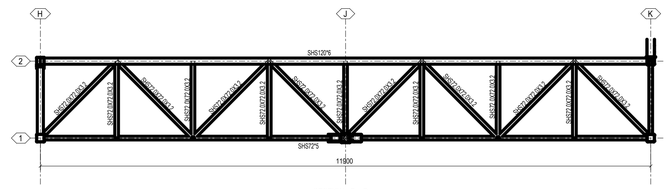

SECTION D - D
1:40

REV.NO.	DESCRIPTION.	REV.DATE	DRAWN.	CHKD.	APPD.
0					

DWG.TITLE :- STRUCTURAL DRAWING FOR DOOR FRAME

PROJECT	HANGER DOOR
CLIENT	GMR

SALT Design Services

SALT DESIGN SERVICES
4-PUSHKAR NIRZAR, SBI COLONY,
NEAR ICICI BANK, KOTHRUD, PUNE-411038.

DRAWN :CDD	CHECKED : HAB	SCALE: 1:100
APPROVED : HAB	JOB CODE. : 1714	DATE: 22.10.2022
DWG.NO: SALT_1729_STR_03_R0	(SH-1OF1)	REV. - R0 SIZE. - A0

A0 [841 x 1189]