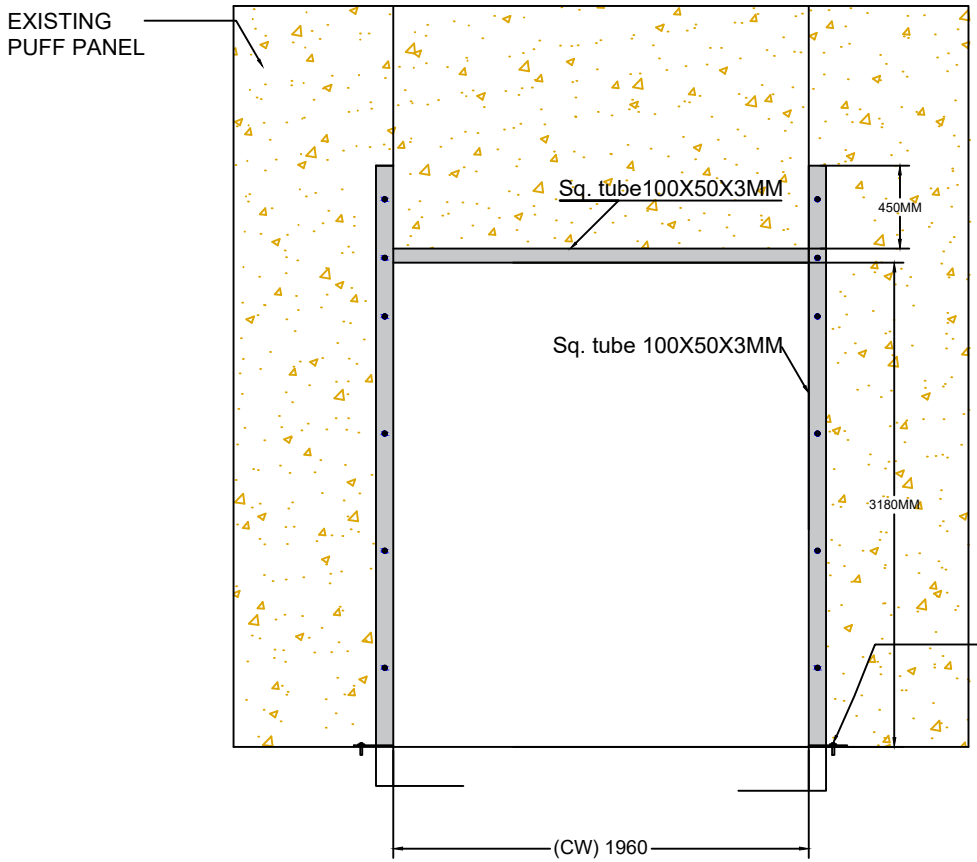


M.S. STRUCTURE DETAILS

Sr	Description	Clear Width (CW)	Clear Height (CH)	QTY
1	HSD With Sensor	**2180**	**3180**	1

This drawing & design is the property of NIHVA TECHNOLOGIES. Not to be sold or copied to any other concern.

TITLE	HIGH SPEED DOOR STRUCTURE DRAWING			NIHVA TECHNOLOGIES PVT. LTD. PUNE Tel : 020 66304033 Email:- info@nihva.com Website:- www.nihva.com	
	NAME	SIGN	DATE		
DRAWN	J.P		01.10.2025	CLIENT - TENNECO CLEAN AIR	
CHECK	B.S		01.10.2025	PROJECT - MACHINE PROTECTION DOOR	
APPRD.	V.T		01.10.2025	FORMAT NO - NIHVA-DD-F-03	
If any queries contact : projectsupport@nihva.com				DWG. NO. : NIHVA/23-24/00XX	REV- R00
ALL DIMENSION ARE IN mm				SCALE: NTS	WT: SHEET: