



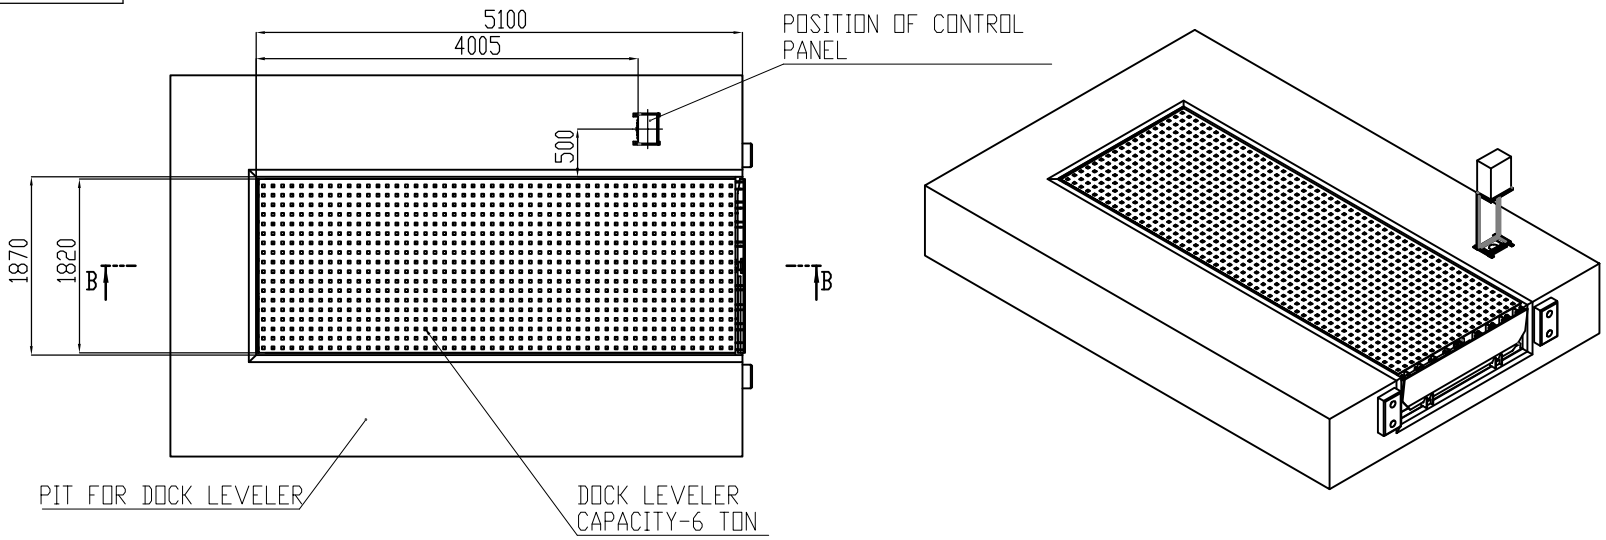


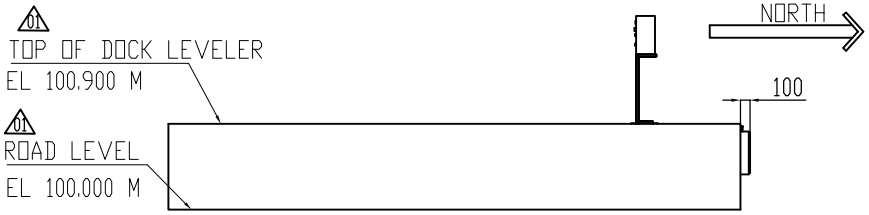

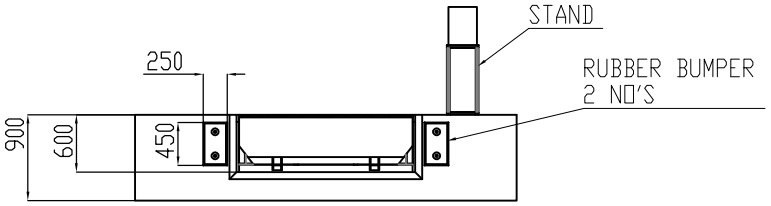

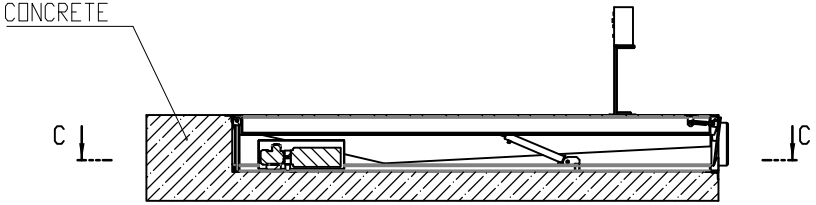

SECTION B-B
SCALE 1 : 28

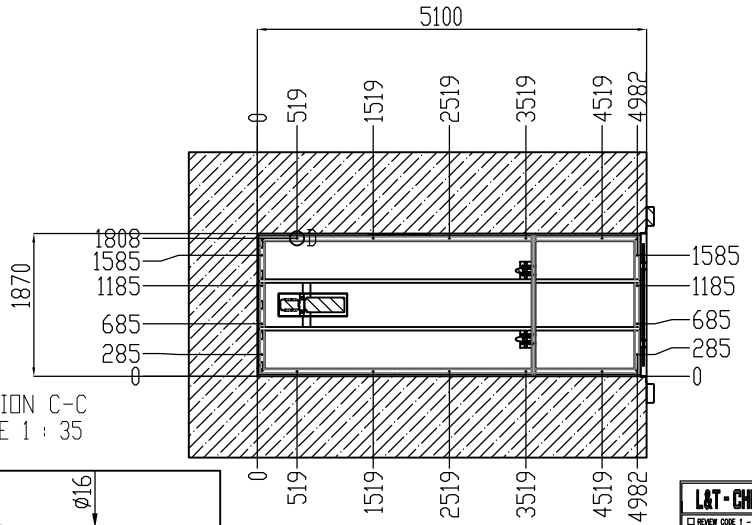


SECTION C-C
SCALE 1 : 35

01

PRODUCT DESCRIPTION -

1. DOCK LEVELER - PIT MOUNTED ELECTRO-HYDRAULIC TYPE
2. CAPACITY- 6 TON POINT LOAD
3. QTY- 2 NOS
4. PRODUCT SIZE- 5100mm(L)X1820mm(W)X600mm(D)
5. PIT SIZE-5100mm(L)X1870mm(W)X600mm(D)

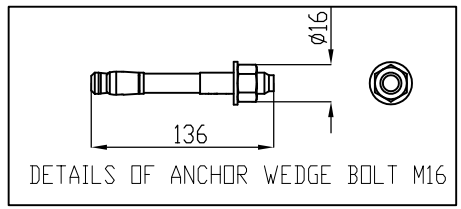

DETAILS OF ANCHOR WEDGE BOLT M16

ø18 HOLE

DETAIL D
SCALE 1 : 35

THIS DOCUMENT AND ANY DATA AND INFORMATION CONTAINED HEREIN ARE CONFIDENTIAL AND THE PROPERTY OF L&T HYDROCARBON ENGINEERING (LTHE) AND THE COPYRIGHT THEREIN IS VESTED IN LTHE. NO PART OF IT MAY BE REPRODUCED, STORED IN A RETRIEVAL SYSTEM OR TRANSMITTED IN ANY FORM OR BY ANY MEANS (ELECTRONIC, MECHANICAL, PHOTOCOPYING, RECORDING OR OTHERWISE) WITHOUT THE PRIOR WRITTEN PERMISSION OF LTHE. IT MUST NOT BE LENT, COPIED OR USED FOR ANY PURPOSE OTHER THAN THAT FOR WHICH IT IS SUPPLIED WITHOUT THE PRIOR WRITTEN CONSENT OF LTHE. ALL RIGHTS RESERVED.

504-LZ-930A/B	GAD OF DOCK LEVELER 01	01
DRAWING NO.	DRAWING TITLE	REV

REFERENCE DOCUMENTS / DRAWINGS

DRG. CATEGORY: (USE TICK MARK) [R] [I] EIL REVIEW/APPROVAL VPTL NO.:
SOIL DATE OF SUBMISSION CODE:

DOCUMENT STATUS
STATEMENT OF SUB: [1st] [2nd] [3rd]
☐ FINAL FOR CODE-1 ☐ AS BUILT
ISSUED FOR
☐ AS BUILT ☑ INFORMATION
☐ CONSTRUCTION ☐ REVIEW

☐ REVIEW CODE 1 – NO COMMENTS PROCEED WITH MANUFACTURE / FABRICATION/ CONSTRUCTION AS PER THE DOCUMENT.
☐ REVIEW CODE 2 – PROCEED WITH MANUFACTURE / FABRICATION / CONSTRUCTION AS PER THE COMMENTED DOCUMENT. REVISED DOCUMENT REQUIRED.
☐ REVIEW CODE 3 – DOCUMENT DOES NOT CONFORM TO BASIC REQUIREMENTS AS MARKED. RESUBMIT FOR REVIEW.
☐ R – DOCUMENT IS RETAINED FOR RECORDS. PROCEED WITH MANUFACTURE / FABRICATION
☐ V-VOID

SIGN: DATE: NAME DICIPLINE SIGN. DATE

REV.	DESCRIPTION	DRN	CHECKED	APPROVED	REVIEWED	APPROVED	DATE
01	ISSUED FOR APPROVAL	SMS	VJ	AK			

OWNER: HINDUSTAN PETROLEUM CORPORATION LIMITED
VISAKH REFINERY MODERNIZATION PROJECT
EPCC-03 PACKAGE FOR RESIDUE UP-GRADATION FACILITY (RUF)

PMC : ENGINEERS INDIA LIMITED (A Govt. of India Undertaking)

LSTK CONTRACTOR: L&T Hydrocarbon Engineering

DETAILED ENGINEERING CENTER: L&T - CHIYODA LIMITED

VENDOR : NIHVA TECHNOLOGIES PVT LTD
VENDOR PO NO: REFINARY/75000-82256/VHM
VENDOR DWG. NO: NIHVA_20-21_0158

DATE: 31.05.21 SCALE: 1:1
DEPT: DESIGN
TITLE: CIVIL DRAWING FOR DOCK LEVELER (504-LZ-930A/B) 01
DRN BY: SMS
CHK BY: VJ
APP BY: AK
PROJECT: LAY-RUF
PWO NO.:
DRG. NO.: 2016-RUF-LT-504-HP-DV-HTPLCD-12005
SH. 2 OF 4
REV. 02
CAD FILE:

L&T - CHIYODA LIMITED

☐ REVIEW CODE 1 – NO COMMENTS PROCEED WITH MANUFACTURE / FABRICATION/ CONSTRUCTION AS PER THE DOCUMENT.
☐ REVIEW CODE 2 – PROCEED WITH MANUFACTURE/ FABRICATION /CONSTRUCTION AS PER THE COMMENTED DOCUMENT. REVISED DOCUMENT REQUIRED.
☐ REVIEW CODE 3 – DOCUMENT DOES NOT CONFORM TO BASIC REQUIREMENTS AS MARKED. RESUBMIT FOR REVIEW.
☐ R – DOCUMENT IS RETAINED FOR RECORDS. PROCEED WITH MANUFACTURE / FABRICATION
☐ V-VOID

COMMENTED BY	REVIEWED BY	APPROVED BY	DATE

THIS REVIEW / APPROVAL DOES NOT RELIEVE THE VENDOR / MANUFACTURER OF THE FULL RESPONSIBILITY AS TO DESIGN CORRECTNESS OF DIMENSIONS & COMPLIANCE WITHALL APPLICABLE REGULATIONS AND WITH THE REQUIREMENTS MADE IN PURCHASER SPECIFICATIONS.