

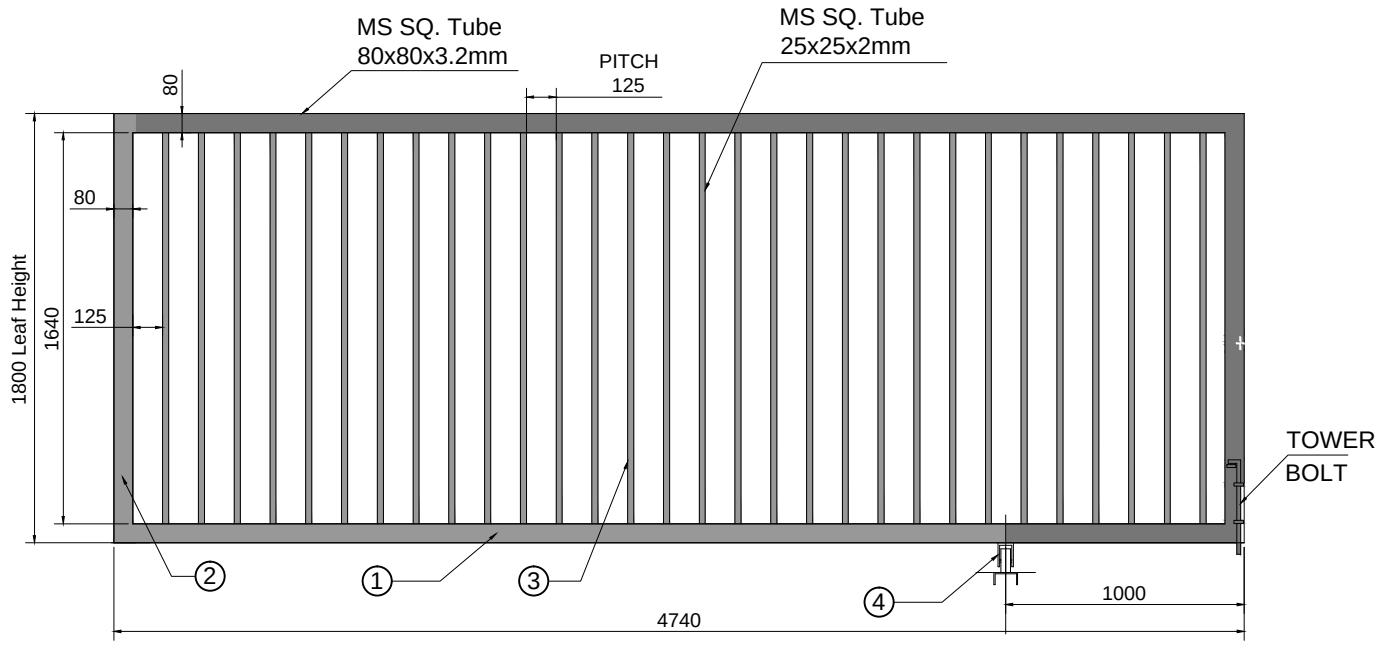


Elevation 1

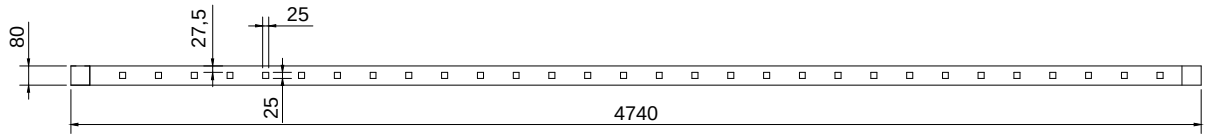

Plan

TOWER BOLT IN SINGLE PIECE

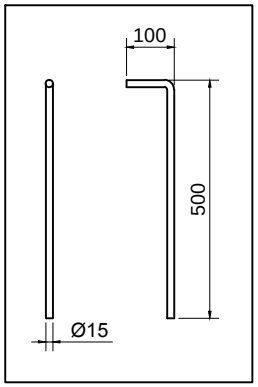

NOTE : ~ OUTER TUBE NOTCH 45° FOR WELDING.

1. OUTER TUBE NOTCH 45° FOR WELDING.
2. GAP BETWEEN INNER TUBE IS 125 MM.
3. WELDING SHOULD BE PROPER.
4. REMOVE ALL SPATTERS FROM ALL OVER GATE.
5. AVOID SUCH TYPE BLOW HOLES IN WELDING.
6. AVOID ALL SHARP CORNERS OR EDGES.
7. WHEEL BKT SHOULD BE LASER CUTTING PROFILE AVOID GAS CUTTING.

Color- 1. For Outer Boundry Golden Yellow RAL 1004
2. For Inner Tubes Marine blue RAL 5002

NOTE : ~ LEAF QTY = 2 NOS.

SR NO	DESCRIPTION	QTY
1	80 x 80 x 3.2THK x 4740L	2 NOS
2	80 x 80 x 3.2THK x 1800L	2 NOS
3	25 x 25 x 2THK x 1640L	30 NOS
4	STD WHEEL BKT & WHEEL	1 NO
5	TOWER BOLT(SEE DRG)	1 NO

TOLERANCE - ±10mm

This drawing & design is the property of NIHVA TECHNOLOGIES. Not to be sold or copied to any other concern.

TITLE
SWING GATE

NIHVA TECHNOLOGIES PVT. LTD.
NIHVA TECHNOLOGIES PVT. LTD. PUNE
Tel : 020 66304033
Email:- info@nihva.com
Website:- www.nihva.com

	NAME	SIGN	DATE
DRAWN	PRADEEP		12.05.2018
CHECK	OMKAR		12.05.2018
APPRD.	OMKAR		12.05.2018

CLIENT -
PROJECT -
SITE LOCATION -

If any queries contact : design@nihva.com
DWG. NO. : NIHVA/17-18/VDR/022
REV- 0
ALL DIMENSION ARE IN mm
SCALE: NTS
WT:
SHEET: 01 OF 01