

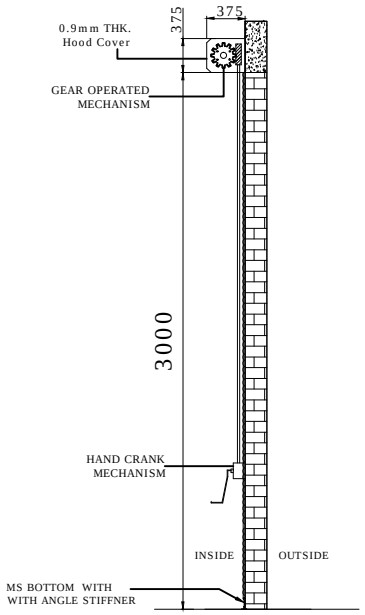



SIDE VIEW

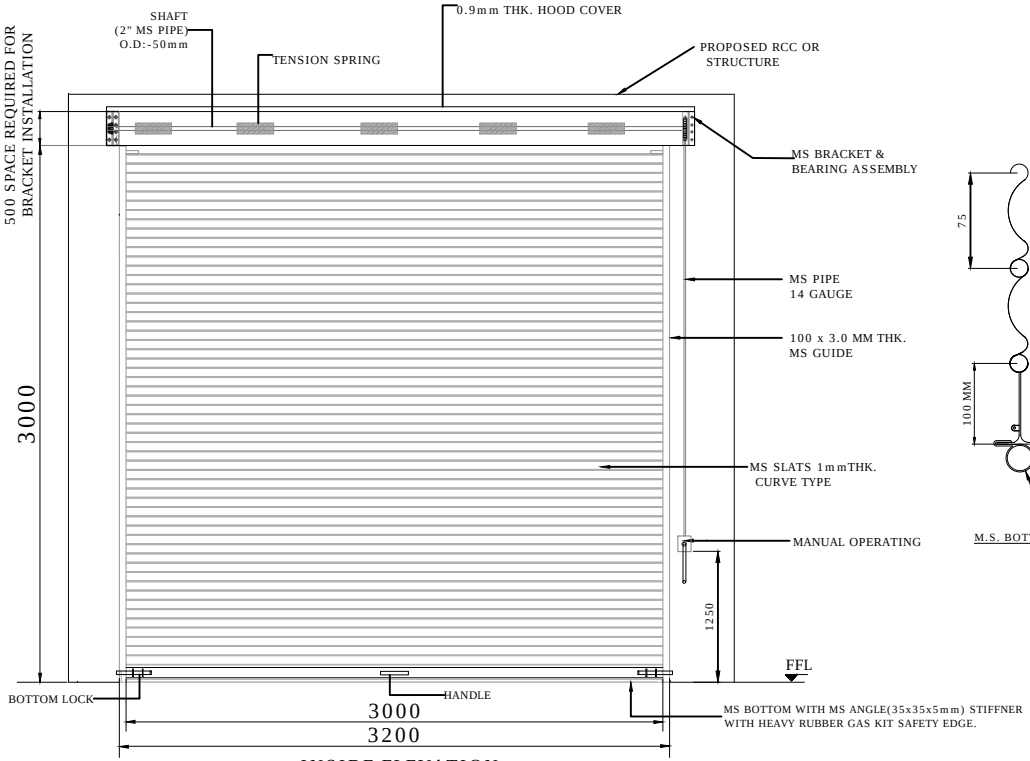


INSIDE ELEVATION

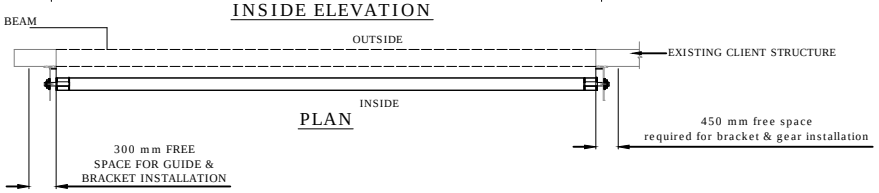

PLAN

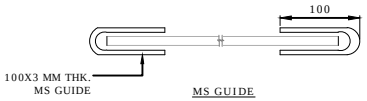

MS GUIDE

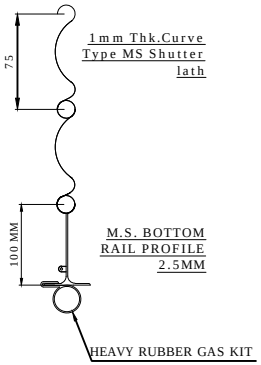

M.S. BOTTOM RAIL PROFILE 2.5MM

R02:-MORE DETAILS ADDED TO THE DRAWING.
R01:- SHUTTER SIZE CHANGED.

CLEAR WIDTH (CW)	CLEAR HEIGHT (CH)	GUIDE SIZE	BRACKET SIZE	SHAFT SIZE (O.D)	QUANTITY	LOCATION
3000	3000	100X3mm	375X375X5mm	50mm	3	PUMP ROOM

DIMENSION :

CLEAR WIDTH	CLEAR HEIGHT	QUANTITY
3000	3000	03 NOS

NOTE:
1.REQUIRED STRUCTURE FOR ROLLING SHUTTER WILL BE CLIENT'S SCOPE.
2. SHUTTER WILL BE POWDER COATED CLIENT SHOULD CONFIRM RAL COLOR SHADE.
3.POWER SUPPLY LOCATION WILL BE ACTUAL SITE CONDITION.

REV NO	DATE	DESCRIPTION
REV 0	29-11-17	INITIAL DRAWING
REV 1	29-11-17	SHUTTER SIZE CHANGED
REV 2	13-12-17	MORE DETAILS ADDED TO THE DRAWING.

NIHVA TECHNOLOGIES PVT. LTD.
NIHVA TECHNOLOGIES PVT. LTD. PUNE
Email:- info@nihva.com
Website:- www.nihva.com

TITLE:

GEAR OPERATED ROLLING SHUTTER 3X3m

CLIENT'S APPROVAL :

CLIENT - SCON PROJECTS

PROJECT - ENZENE BIOSCIENCES LTD.

SITE LOCATION - CHAKAN.

DWG. NO. : NIHVA/17-18/0297 REV.:-02

SCALE: NTS WT: SHEET:1 OF 1

		DATE	SIGN.
DRAWN	SURAJ	13-12-2017	
CHECK	OMKAR	13-12-2017	
APPRD	SHEKHAR	13-12-2017	

If any queries contact : design@nihva.com

NOTE: ALL DIMENSIONS ARE IN mm

THIS DRAWING & DESIGN IS THE PROPERTY OF NIHVA TECHNOLOGIES. NOT TO BE SOLD OR COPIED TO ANY OTHER CONCERN.