
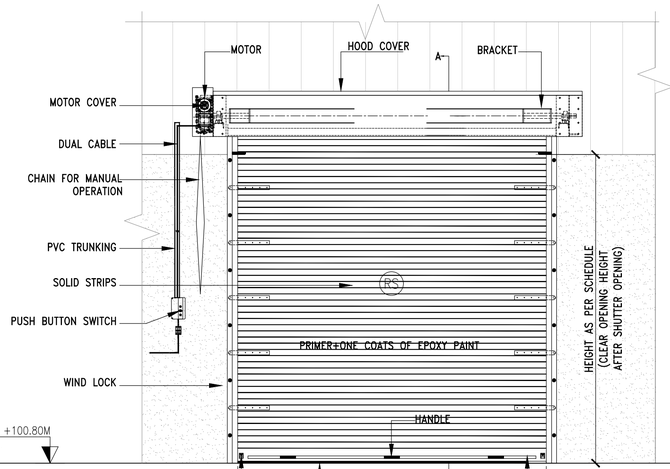


ELEVATION–E3


SCALE 1:30

M.S ROLLING SHUTTER (RS1,RS2,RS3,RS5)

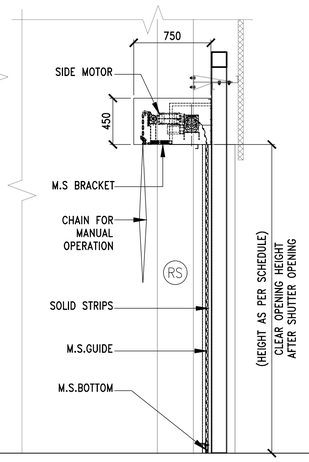

SECTION:D–D


SCALE 1:30

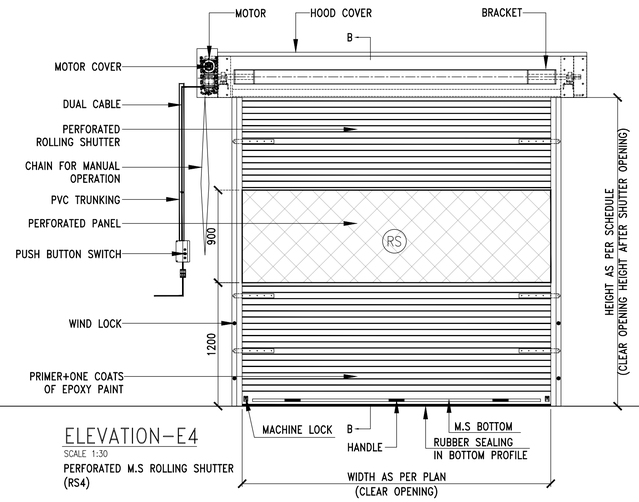

ELEVATION–E4


SCALE 1:30

PERFORATED M.S ROLLING SHUTTER (RS4)

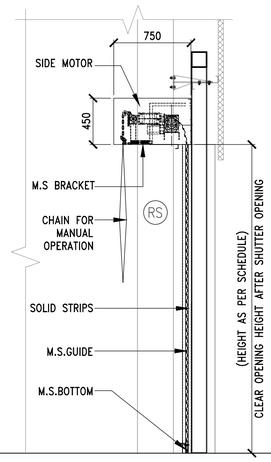

TYPICAL SECTION OF ROLLING SHUTTER

SCALE 1:30

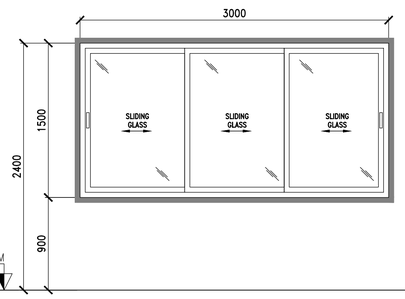


W1–3000X1500

SCALE 1:30

THREE TRACK SLIDING ALUMINUM WINDOW

TOTAL : 73 NOS.

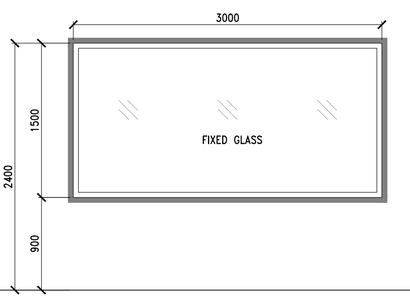


W1A–3000X1500

SCALE 1:30

ALUMINUM FIXED GLASS WINDOW

TOTAL : 02 NOS.

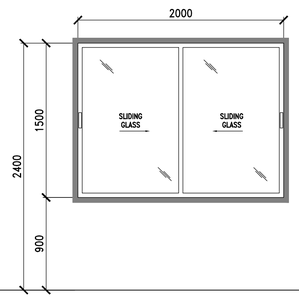


W2–2000X1500

SCALE 1:30

TWO TRACK SLIDING ALUMINUM WINDOW

TOTAL : 11 NOS.

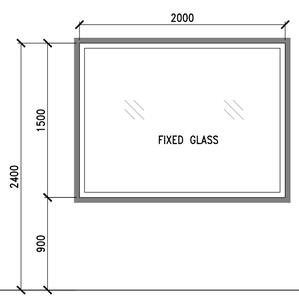


W2A–2000X1500

SCALE 1:30

ALUMINUM FIXED GLASS WINDOW

TOTAL : 04 NOS.

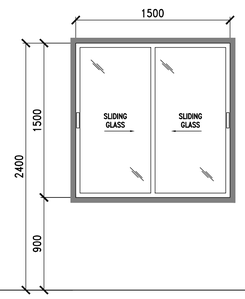


W3–1500X1500

SCALE 1:30

TWO TRACK SLIDING ALUMINUM WINDOW

TOTAL : 01 NOS.

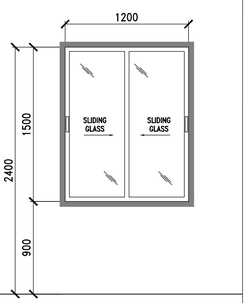


W4–1200X1500

SCALE 1:30


TWO TRACK SLIDING ALUMINUM WINDOW

TOTAL : 01 NOS.

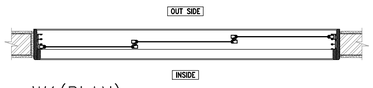


W1(PLAN)

SCALE 1:30

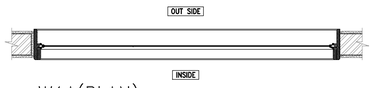


W1A(PLAN)

SCALE 1:30

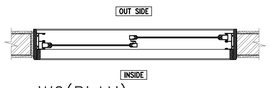


W2(PLAN)

SCALE 1:30

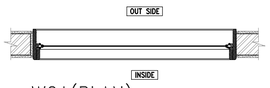


W2A(PLAN)

SCALE 1:30

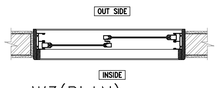


W3(PLAN)

SCALE 1:30

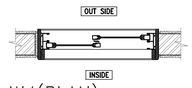

W4(PLAN)

SCALE 1:30

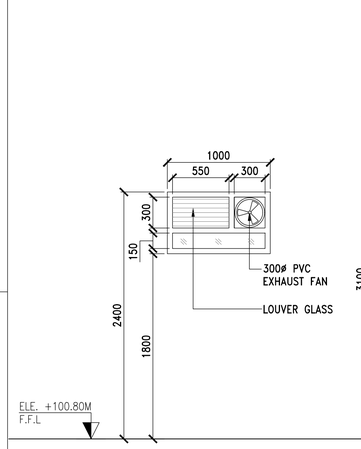


V1–1000X600

SCALE 1:30

ALU. LOUVERED VENTILATOR WITH FIXED GLASS AND EXHAUST FAN

TOTAL : 06 NOS.

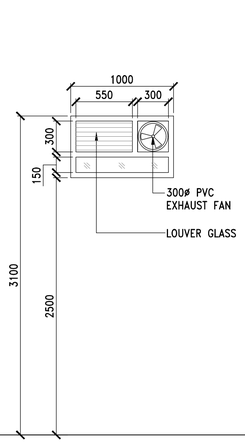


V1A–1000X600

SCALE 1:30

ALU. LOUVERED VENTILATOR WITH FIXED GLASS AND EXHAUST FAN

TOTAL : 01 NOS.

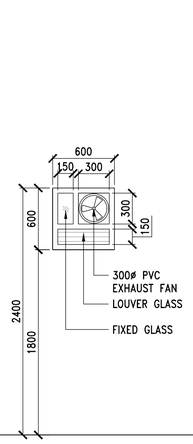


V2–600X600

SCALE 1:30

ALU. LOUVERED VENTILATOR WITH FIXED GLASS AND EXHAUST FAN

TOTAL : 14 NOS.

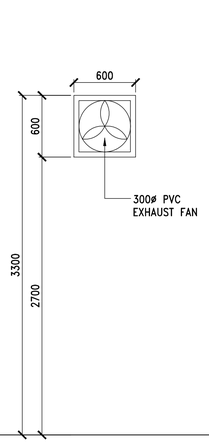


EX–600 X 600

SCALE 1:30

EXHAUST FAN

TOTAL : 02 NOS.

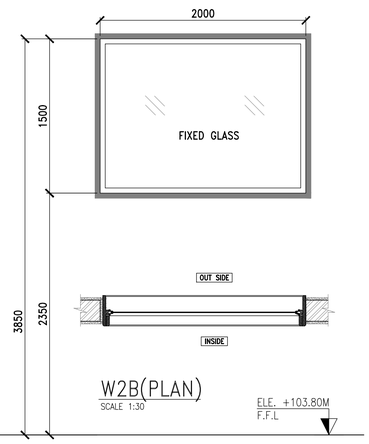

W2B(PLAN)

SCALE 1:30

W2B–2000X1500

SCALE 1:30

ALUMINUM FIXED GLASS WINDOW

TOTAL : 01 NOS.

ROLLING SHUTTER SCHEDULE

TYPE	WIDTH	WIDTH WITH STONE	HEIGHT	LINTEL	NOS.	DESCRIPTION
RS1	5.00	–	5.00	–	1	M.S ROLLING SHUTTER
RS2	4.00	–	5.00	–	1	M.S ROLLING SHUTTER
RS3	3.50	–	4.00	–	1	M.S ROLLING SHUTTER
RS4	3.00	–	3.00	–	1	PERFORATED M.S ROLLING SHUTTER
RS5	2.50	–	3.00	–	2	M.S ROLLING SHUTTER

WINDOW SCHEDULE

TYPE	WIDTH	WIDTH WITH STONE	HEIGHT	SILL	LINTEL	NOS.	DESCRIPTION
EX	0.60	0.70	0.60	2.70	3.35	2	EHAUST FAN
V1	1.00	1.10	0.60	1.80	2.40	6	ALU. LOUVERED VENTILATOR WITH FIXED GLASS AND EXHAUST FAN
V1A	1.00	1.10	0.60	2.50	3.15	1	ALU. LOUVERED VENTILATOR WITH FIXED GLASS AND EXHAUST FAN
V2	0.60	0.70	0.60	1.80	2.45	14	ALU. LOUVERED VENTILATOR WITH FIXED GLASS AND EXHAUST FAN
W1	3.00	3.10	1.50	0.90	2.45	76	THREE TRACK SLIDING ALUMINUM WINDOW
W1A	3.00	3.10	1.50	0.90	2.45	2	ALUMINUM FIXED GLASS WINDOW
W2	2.00	2.10	1.50	0.90	2.45	11	TWO TRACK SLIDING ALUMINUM WINDOW
W2A	2.00	2.10	1.50	0.90	2.45	4	ALUMINUM FIXED GLASS WINDOW
W3	1.50	1.60	1.50	0.90	2.45	1	TWO TRACK SLIDING ALUMINUM WINDOW
W4	1.20	1.30	1.50	0.90	2.45	1	TWO TRACK SLIDING ALUMINUM WINDOW

REFERENCE DRAWINGS

SR.NO.	DRAWING TITLE	DRAWING NO.
01	GROUND FLOOR DOOR & WINDOW OPENING LAYOUT OF FACTORY BUILDING	2410-FAC-A05-SH1-A1-R0
02	GROUND & FIRST FLOOR DOOR & WINDOW OPENING LAYOUT OF ELECTRICAL SUBSTATION, COMPRESSOR AND CANTEEN BUILDING	2410-ELE/COMP/CAN-A05-SH1-A1-R0
03	GROUND,FIRST & TERRACE DOOR & WINDOW OPENING LAYOUT OF LAB/ADMIN BUILDING	2410-LAB/ADM-A05-SH1-A1-R0
04	GROUND FLOOR DOOR & WINDOW OPENING LAYOUT OF CANTEEN/ADMIN BUILDING (LEAN TO SHED)	2410-ADM-A05-SH1-A1-R0

NOTE :-

1. DO NOT SCALE THE DRAWING. REFER TO WRITTEN DIMENSIONS ONLY.
2. ALL MEASUREMENTS MUST BE CHECKED AND VERIFIED AT SITE. ANY DISCREPANCY FOUND,TO BE NOTIFIED TO THE CONSULTING ENGINEER. BEFORE EXECUTION.
3. ALL DIMENSIONS ARE IN MM.& ALL LEVELS ARE IN METERS UNLESS OTHERWISE SPECIFIED.
4. F.G.L & F.R.L AS PER SITE ROAD LAYOUT PLAN.

LEGEND :-

F.G.L.	= FINISHED GROUND LEVEL
F.R.L.	= FINISHED ROAD LEVEL
F.F.L.	= FINISHED FLOOR LEVEL
I	= IN SIDE OPEN
O	= OUT SIDE OPEN
	230MM THK. BRICK MASONRY WALL
	115MM THK. BRICK MASONRY WALL
	100MM THK. PARTITION WALL

REV.	DATE	DESCRIPTION	DRN.	CHK.	APP.	PRN.
R0	24-09-24	ISSUED FOR CONSTRUCTION	MITUL	AMITA	VIRAL	MAIL
R0	09-09-24	ISSUED FOR REVIEW	MITUL	AMITA	VIRAL	MAIL

ISSUED FOR

☐ INFORMATION ☐ APPROVAL ☑ CONSTRUCTION

☐ ENQUIRY ☐ ORDER ☐ REVIEW

CLIENT : ROCATE CABLES LLP, BAVLA

PROJECT : PLANT BUILDING

CONSULTANT : SHAH & TALATI Design & Engineering
9th FLOOR, KIRTI TOWER, TILAK ROAD, VADODARA-390001, GUJARAT, INDIA.
PHONE : +91-265-2440701 / 2440726
E-MAIL : design@shahntalati.com
WEBSITE : www.shahntalati.com

PROJECT NO. :- 2410

TITLE :- TYPICAL WINDOW & ROLLING SHUTTER DETAIL DRAWING

DRAWN BY	MITUL PARMAR	R0 24 09 24
CHECKED BY	AMITA	
APPROVED BY	VIRAL	
DRAWING NO.	2410-FAC-A05-SH4-A1-R0	SHEET 4 OF 4
SCALE : 1:30		

THIS DOCUMENT OR DRAWING IS THE PROPERTY OF SHAH & TALATI CONSULTING ENGINEERS AND SHALL NOT, UNDER ANY CIRCUMSTANCES, BE TOTALLY OR PARTIALLY, DIRECTLY OR INDIRECTLY, TRANSFERRED, REPRODUCED, COPIED, DISCLOSED OR USED WITHOUT SHAH & TALATI'S PRIOR WRITTEN CONSENT.

A1