
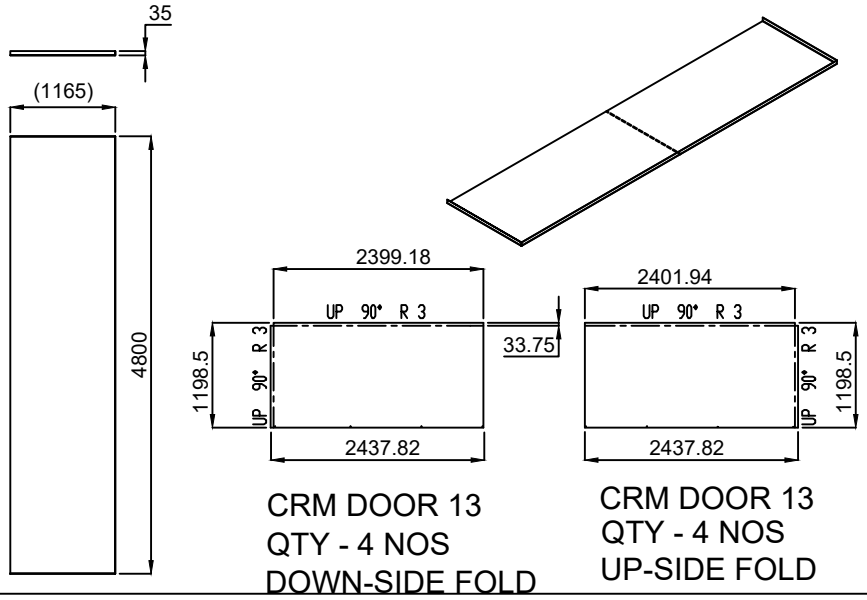



CRM DOOR 13
QTY - 4 NOS
DOWN-SIDE FOLD

CRM DOOR 13
QTY - 4 NOS
UP-SIDE FOLD

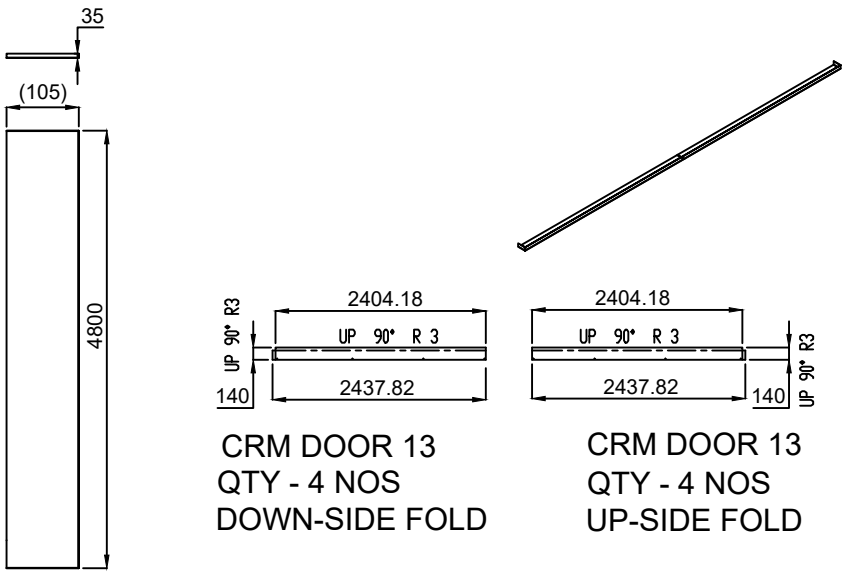

CRM DOOR 13
QTY - 4 NOS
DOWN-SIDE FOLD

CRM DOOR 13
QTY - 4 NOS
UP-SIDE FOLD

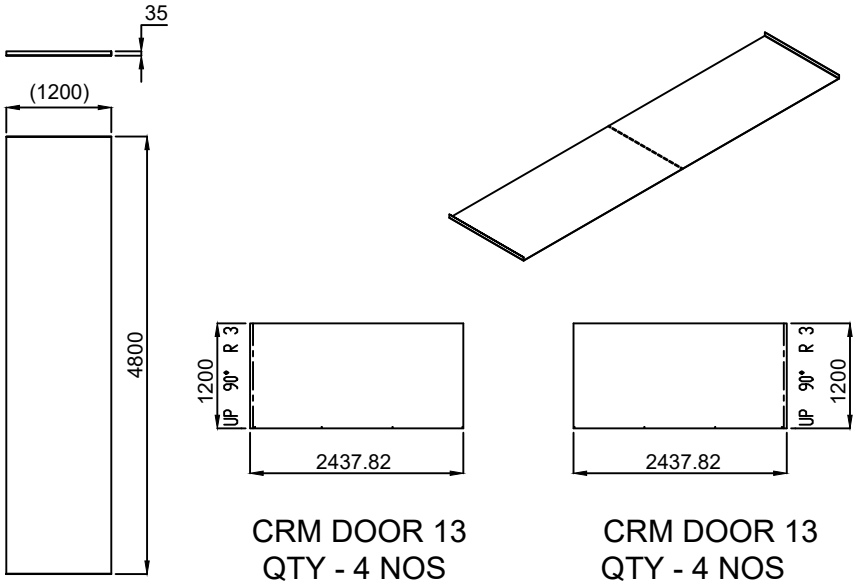


CRM DOOR 13
QTY - 4 NOS
DOWN-SIDE FOLD

CRM DOOR 13
QTY - 4 NOS
UP-SIDE FOLD

NOTE: DURING BENDING CRITICAL DIMENSION SHOULD BE MANDETORY

CRM DOOR ALL

QTY - 16 NOS / each sheet all qty

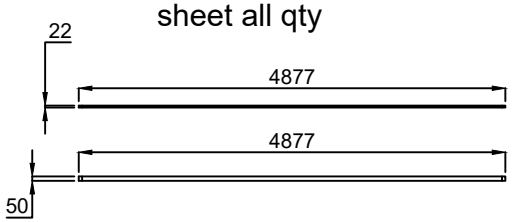

PPGI SHEET 1 MM

REV.	REVISION DESCRIPTION	Date	Revised By
000	MODIFIED DUE TO RECIEVED COIL SIZE 1210 MM INSTEAD OF 1250 MM	21/05/2022	MAHESH S.

This drawing & design is the property of NIHVA TECHNOLOGIES. Not to be sold or copied to any other concern.

TITLE:- 4 LEAF PPGI CLADDING CRM DOOR 13

NIHVA TECHNOLOGIES PVT. LTD.

NIHVA TECHNOLOGIES PVT. LTD. PUNE
Tel : 020 66304033
Email:- info@nihva.com
Website:- www.nihva.com

	NAME	DATE	SIGN
DRAWN	M.SUTAR	21/05/2022	
CHECK	M.SUTAR	21/05/2022	
APPRD.			

CLIENT - NIHVA TECHNOLOGIES PVT.LTD

LOCATION -

PRODUCT - SLIDING DOOR

If any queries contact : design@nihva.com

DWG NO:-NIHVA/22-23/VDR/0015 REV- 0

ALL DIMENSION ARE IN mm

SCALE: NTS SCALE:-- 1:1 SHEET: 01 OF 02