




SIDE VIEW

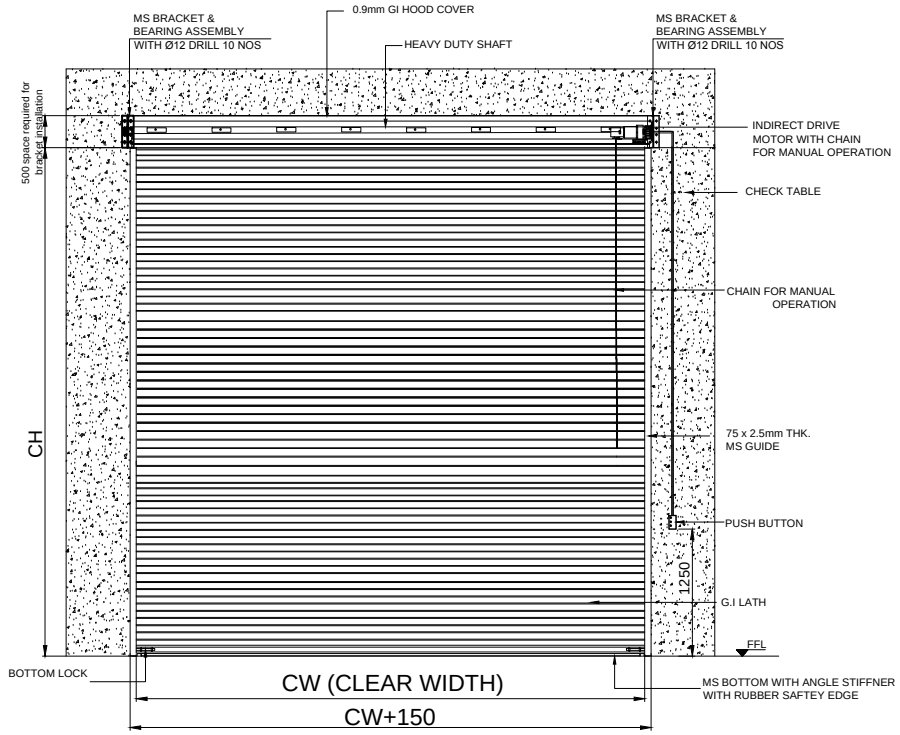


ELEVATION

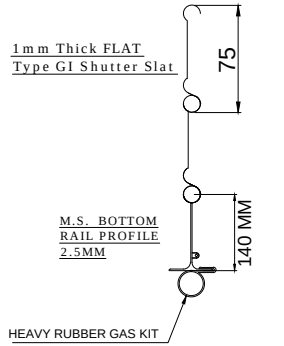

M.S. BOTTOM RAIL PROFILE 2.5MM

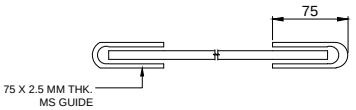

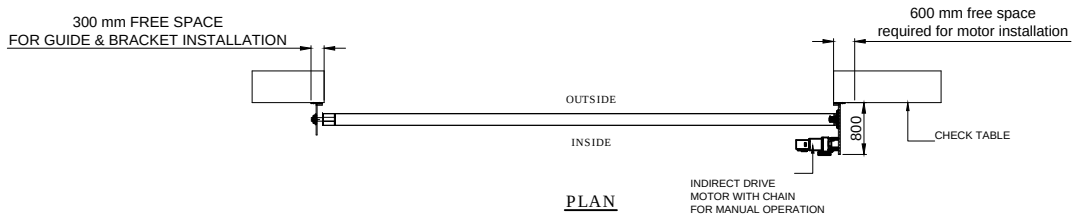

PLAN

NOTE-
1. ALL CIVIL WORK WILL BE CLIENT'S SCOPE.

TOLERANCE - ±10mm

S.NO	RAL CODE	COLOR	CLEAR WIDTH	CLEAR HEIGHT	QTY.	MOUNTING
01	RAL 9002	WHITE GRAY	4000mm	5000mm	02 NOS	STRUCTURE
			2500mm	3000mm	11 NOS	WALL

This drawing & design is the property of NIHVA TECHNOLOGIES. Not to be sold or copied to any other concern.

TITLE
MOTORISED ROLLING SHUTTER

	NAME	SIGN	DATE
DRAWN	P.A		07.01.2020
CHECK	G.J		07.01.2020
APPRD.			

If any queries contact : design@nihva.com

ALL DIMENSION ARE IN mm

NIHVA
NIHVA TECHNOLOGIES PVT. LTD.
Website:- www.nihva.com
NIHVA TECHNOLOGIES PVT. LTD. PUNE
Tel : 020 66304033
Email:- info@nihva.com

CLIENT -
PROJECT -
SITE LOCATION -
DWG. NO. : NIHVA/19-20/VDR/273 | REV- R00
SCALE: NTS | WT: | SHEET: 01 OF 01