
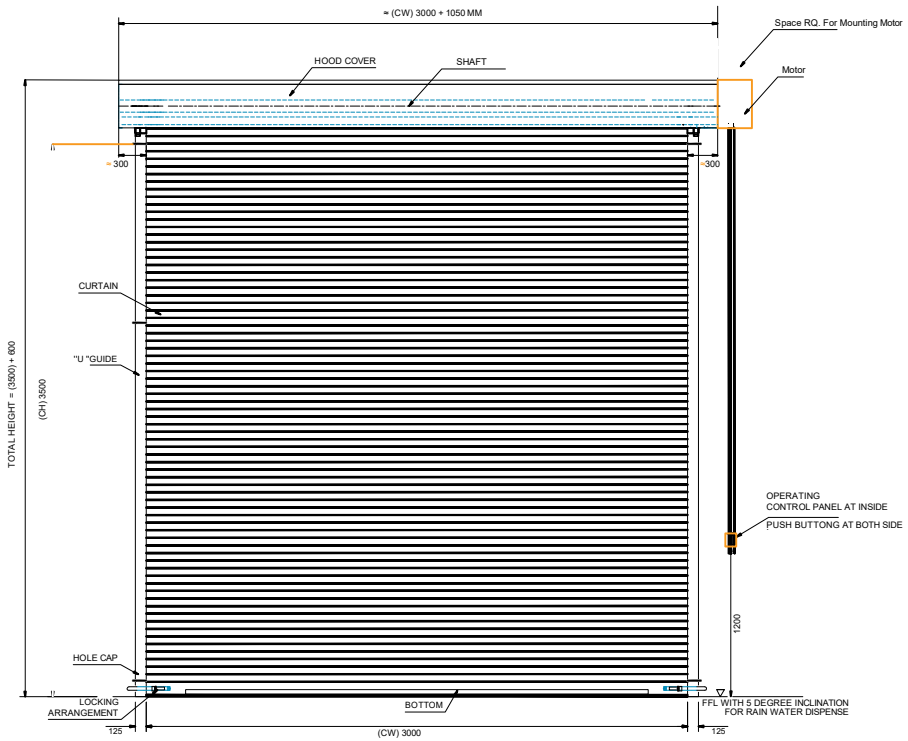


INSIDE ELEVATION

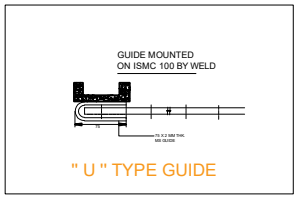

" U " TYPE GUIDE

TECHNICAL SPECIFICATION:-

SR.	SPECIFICATION	DETAILS
1.	Description & Drive	Double Wall PUF Insulated Motorised Rolling Shutter (Direct Drive) with Manual Chain Arrangment
2.	Location Area	Inside / Outside
3.	Mounting Surface	Side Brackets: Optional / Structure
4.	Slat	Galvanised Steel - 95 x 19 mm With PUF Filled Inside (THK-0.5 mm TCT)
5.	Density	48 kg /m3 (For Wind Speed 50 m/Sec)
6.	Bottom Profile	MS Plate 100 x 2 mm Thk. with Angle Stiffner
7.	Guide Profile	M.S." U " Shape profile 75 x 2 mm Thk.
8.	Hood Cover & Motor Cover	Made of GI Sheet Thickness 0.9 mm
9.	Accessories	Control Panel,Push Button On Both Side,In-Built Limit Switches

SHUTTER SIZES :-

SR.	CLEAR WIDTH	CLEAR HEIGHT	QTY.
01	3000	3500	01


This drawing & designing is the property of NIHVA TECHNOLOGIES. Not to be sold or copied to any other concern.

TITLE :-
DOUBLE WALL PUF INSULATED
MOTORISED ROLLING SHUTTER

NIHVA TECHNOLOGIES PVT. LTD.
NIHVA TECHNOLOGIES
PVT. LTD. PUNE
Tel : 020 66304033
Email:- info@nihva.com
Website:- www.nihva.com

	NAME	DATE
DRAWN	J.S.	19/01/2024
CHECK	A.K.	19/01/2024
APPROVAL	V.T.	19/01/2024

CLIENT - RINAC
PROJECT -ROLLING SHUTTER
FORMAT NO - NIHVA-DD-F-03
DWG. NO. : NIHVA/23-24/104 REV-01
SCALE: NTS WT: SHEET: 01 OF 01
ALL DIMENSION ARE IN mm
If any queries contact : design@nihva.com

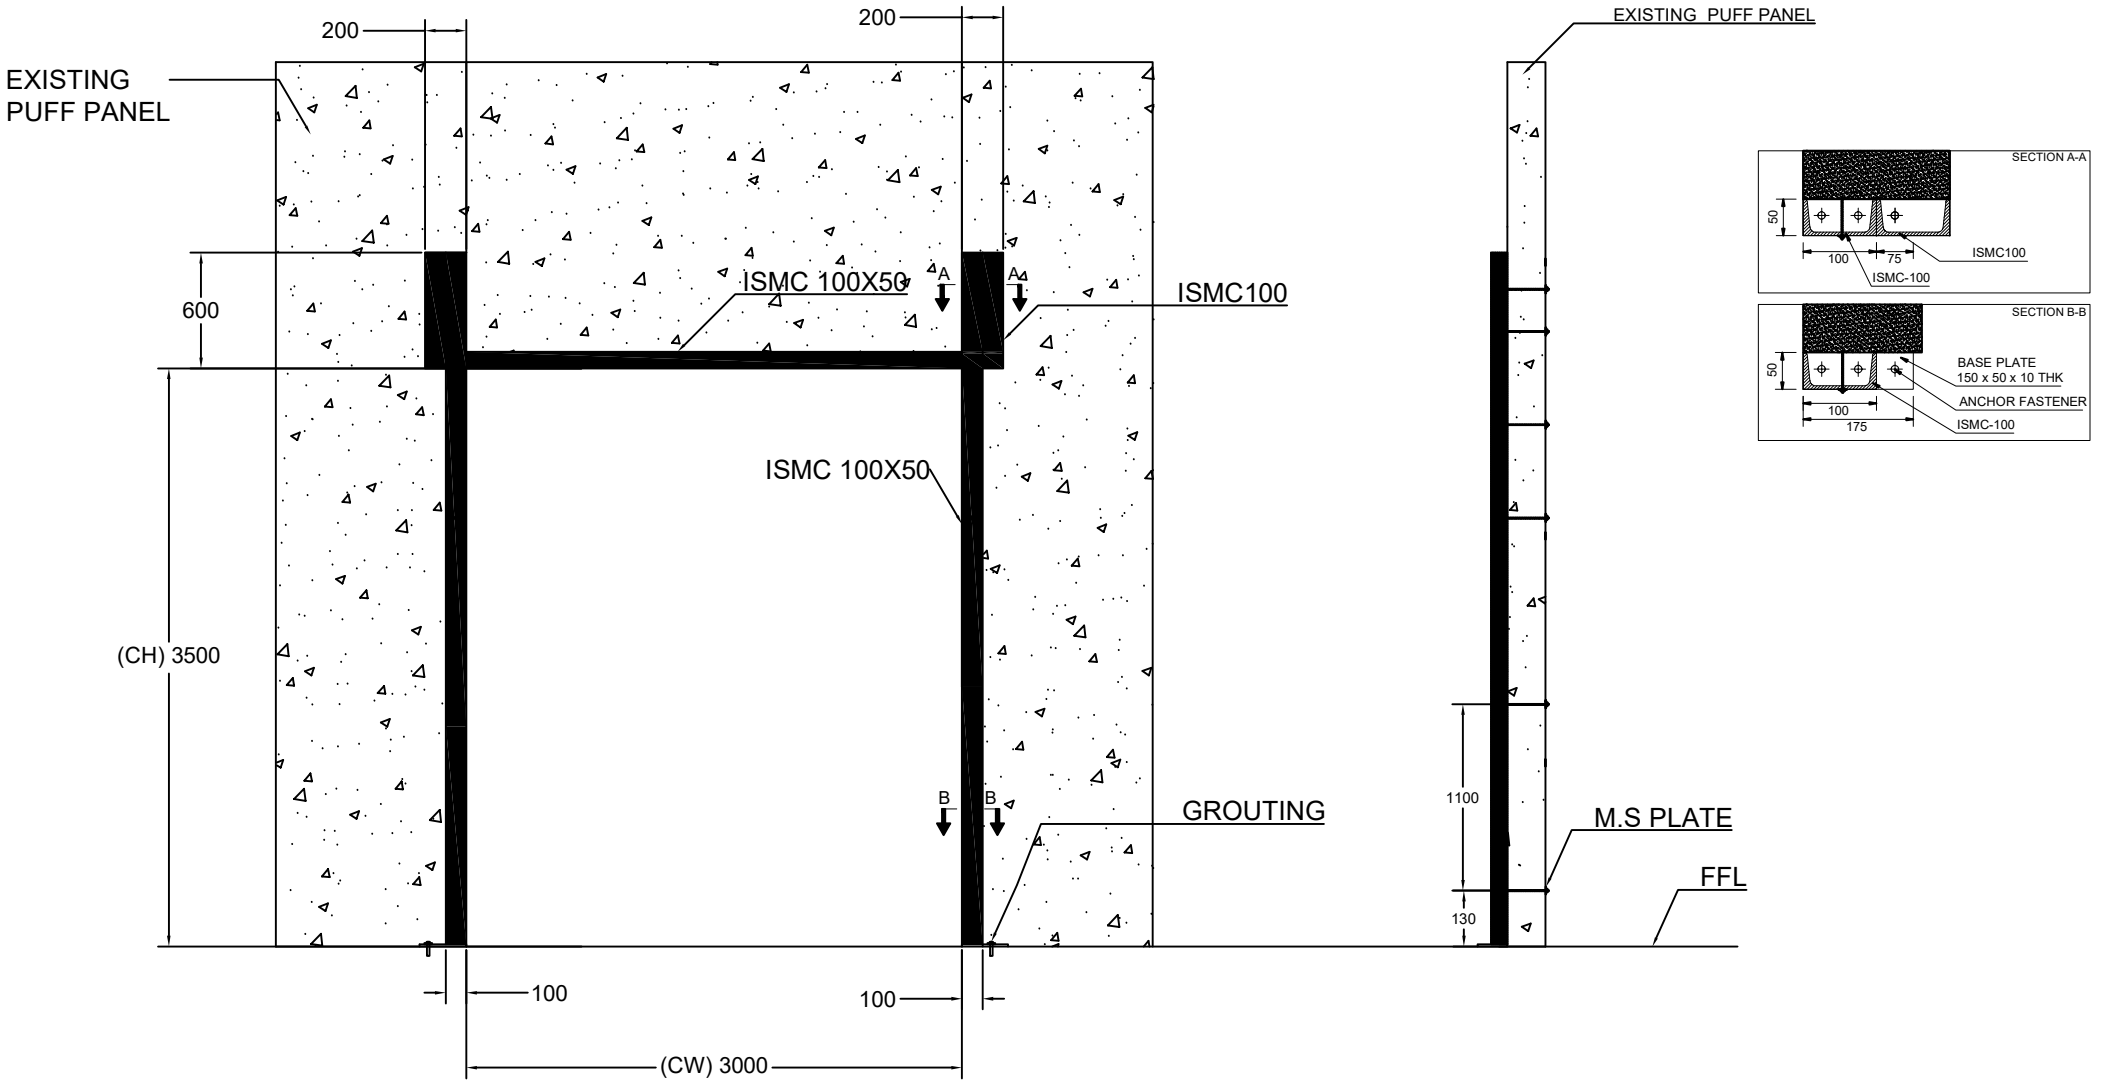

M.S. STRUCTURE DETAILS

SR.	CLEAR WIDTH	CLEAR HEIGHT	QTY.
01	3000	3500	01

This drawing & design is the property of NIHVA TECHNOLOGIES. Not to be sold or copied to any other concern.

TITLE	SHUTTER ST.			
	NAME	SIGN	DATE	
DRAWN	J.S		19.01.2024	CLIENT - RINAC
CHECK	A.K		19.01.2024	PROJECT - ROLLING SHUTTER ST.
APPRD.	V.T		19.01.2024	FORMAT NO - NIHVA-DD-F-03
If any queries contact : projectsupport@nihva.com				DWG. NO. : NIHVA/23-24/104 / REV- R00
ALL DIMENSION ARE IN mm				SCALE: NTS / WT: / SHEET:

NIHVA TECHNOLOGIES PVT. LTD.
NIHVA TECHNOLOGIES PVT. LTD. PUNE
Tel : 020 66304033
Email:- info@nihva.com
Website:- www.nihva.com