



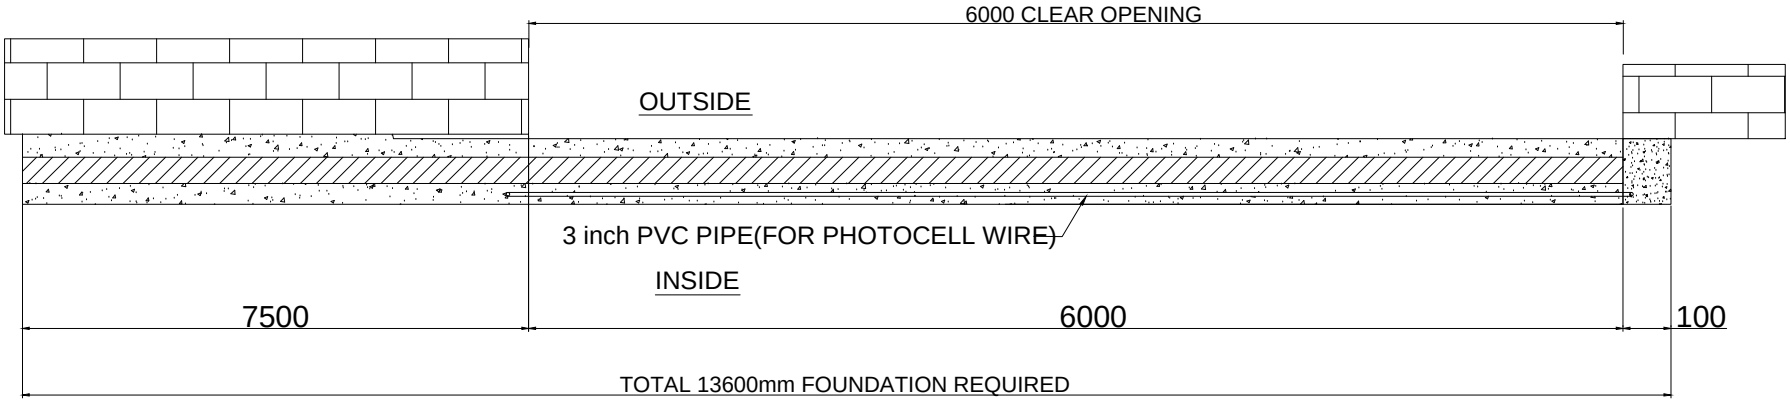

PLAN

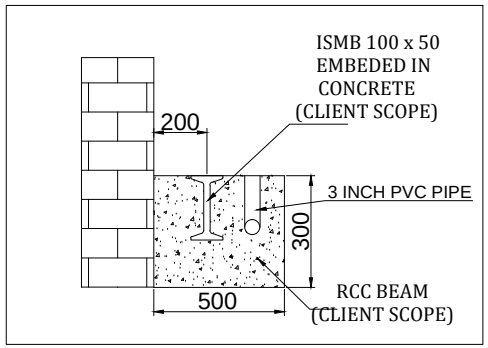

This drawing & design is the property of NIHVA TECHNOLOGIES. Not to be sold or copied to any other concern.

TITLE: FOUNDATION OF SLIDING GATE 6X1.8m GATE NO 6		NIHVA TECHNOLOGIES PVT. LTD. PUNE Tel : 020 66304033 Email:- info@nihva.com Website:- www.nihva.com
	SIGN	DATE
DRAWN	SURAJ	15/09/17
CHECK	SAGAR P.	15/09/17
REV.		
APPROVAL	S.S	15/09/17
If any queries contact : projects@nihva.com		
ALL DIMENSION ARE IN mm		

CLIENT - TATA PROJECT		
PROJECT - ALSTOM		
SITE LOCATION -MADHEPURA,BIHAR		
DWG. NO. : NIHVA/17-18/0088/R01		
SCALE: NTS	WT:	SHEET: 01 OF 01