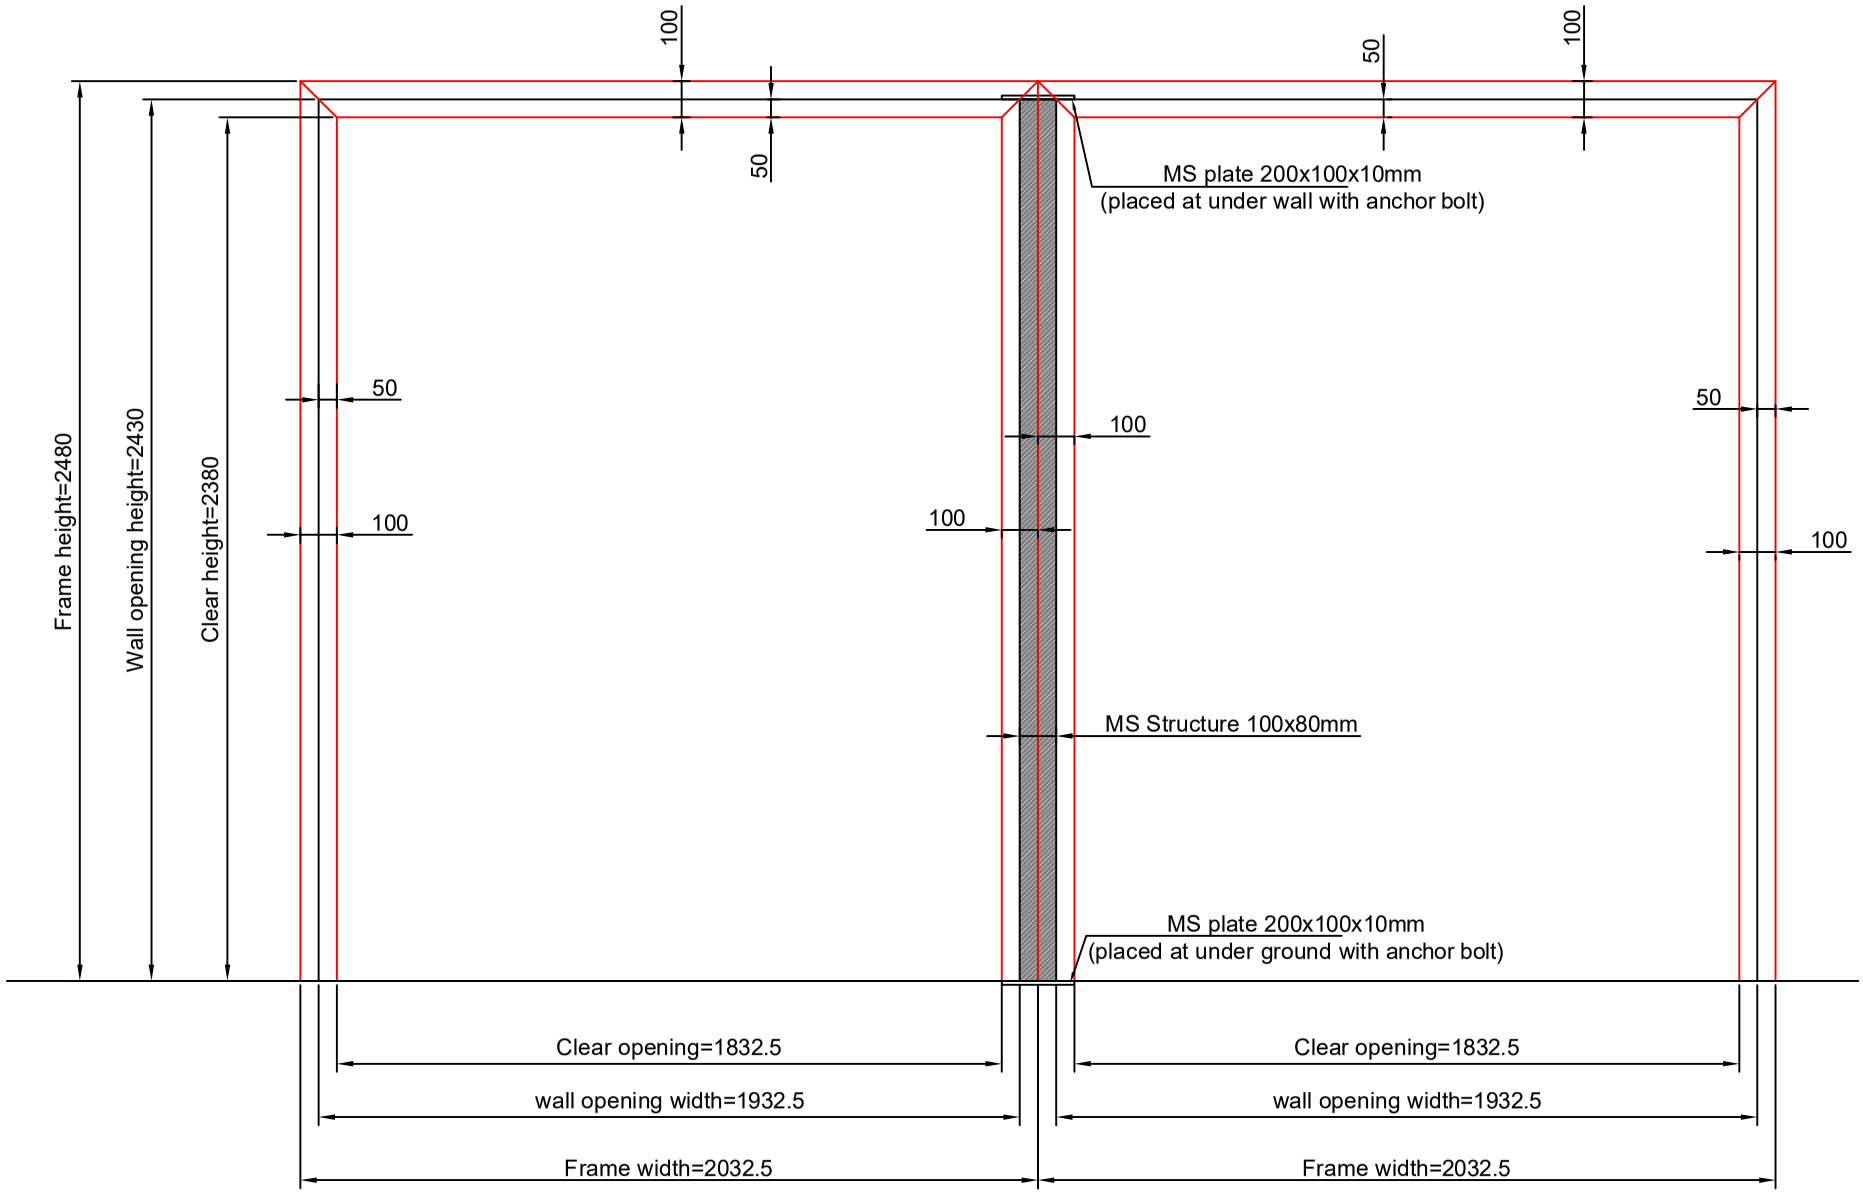


Note:-

1.All dimension are in MM

2.All Civil work and Required structure is in client scope

3.Required100x80mm MS structure

Rev No.	Revision	Date	Revised By

This drawing & design is the property of NIHVA TECHNOLOGIES. Not to be sold or copied to any other concern.

TITLE:- NIHVA Make NFF3 Flip Flap Door Structure

NIHVA TECHNOLOGIES PVT. LTD.

NIHVA TECHNOLOGIES PVT. LTD. PUNE
Tel : 020 66304033
Email:- info@nihva.com
Website:- www.nihva.com

	NAME	DATE	SIGN
DRAWN	SUJATA	25-03-2022	
CHECK	G.P	25-03-2022	
APPRD.	P.J	25-03-2022	

If any queries contact : design@nihva.com

ALL DIMENSION ARE IN mm

CLIENT - RBCC

LOCATION - PUNE

PRODUCT - FLIP FLAP DOOR

DWG NO:-NIHVA/21-22/CLT/0376 | REV- 0

SCALE: NTS | SCALE:-- 1:1 | SHEET: 01 OF 01