
LOCATION AREA :- SEZ 1 C - GROUND FLOOR- EXIT

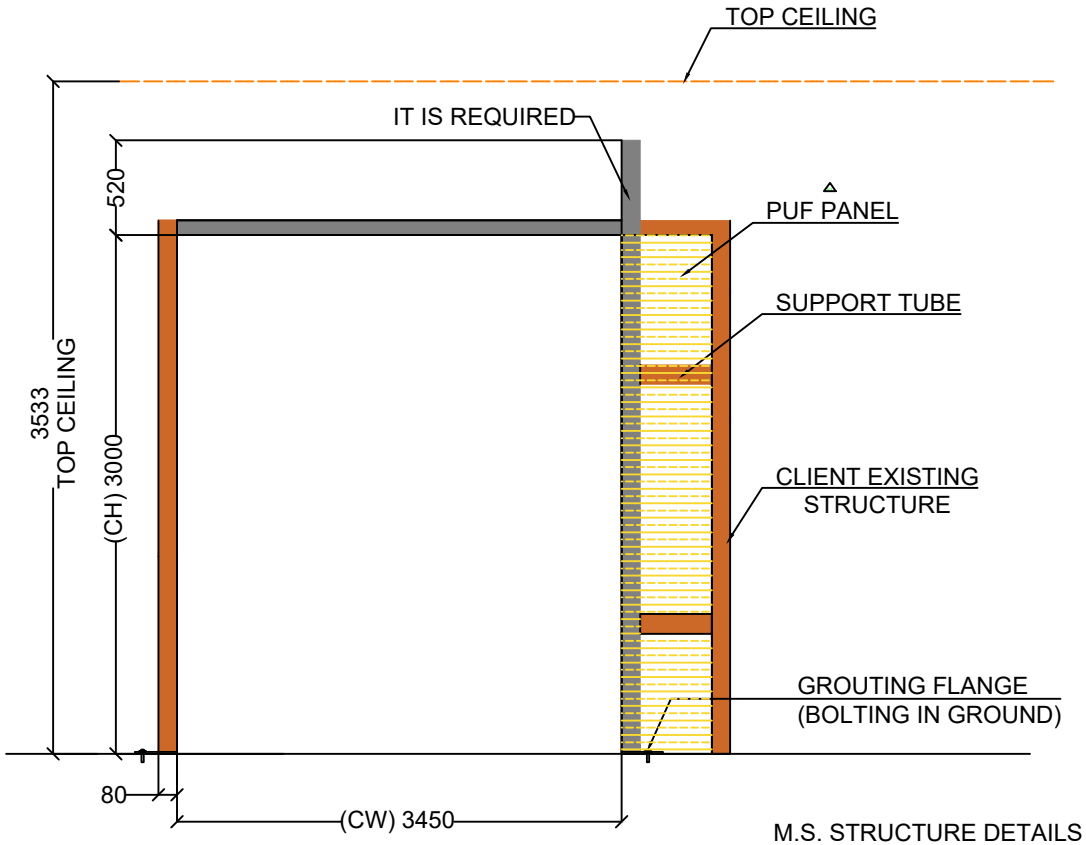

M.S. STRUCTURE DETAILS

Clear Width (CW)	Clear Height (CH)	QTY
3450	**3000**	01

NOTE :-

1. ALL DIMENSIONS ARE IN MM
2. THIS DRAWING IS SOLELY MEANT TO BE UNDERSTOOD.

Sr.No	DESCRIPTION	REV.NO	DRAWN	DATE
1.	PUF PANEL ADD	REV.01	S.J.	02.12.2024
2.				

This drawing & design is the property of NIHVA TECHNOLOGIES. Not to be sold or copied to any other concern.

TITLE:- HIGH SPEED DOOR STRUCTURE DRAWING

	NAME	SIGN	DATE
DRAWN	S.J		14.11.2024
CHECK	S.W.		14.11.2024
APPRD.	V.T		14.11.2024

If any queries contact : projectsupport@nihva.com

ALL DIMENSION ARE IN mm

NIHVA TECHNOLOGIES PVT. LTD.
NIHVA TECHNOLOGIES PVT. LTD. PUNE
Tel : 020 66304033
Email:- info@nihva.com
Website:- www.nihva.com

CLIENT - SERUM INSTITUTE OF INDIA PVT.LTD

PROJECT - HIGH SPEED DOOR ST.

FORMAT NO - NIHVA-DD-F-03

DWG. NO. : NIHVA/24-25/SM/24100301 | REV- R01

SCALE: NTS | WT: | SHEET: