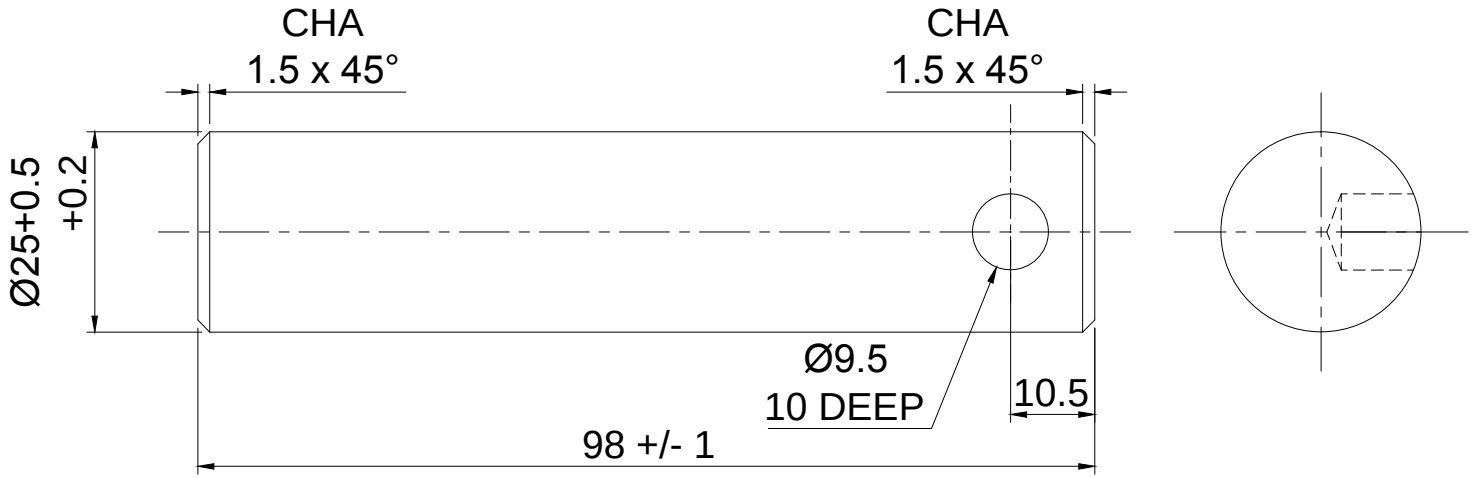


NOTE:~ MTL : EN8

Ø25 X 101L = 1 NO

TOLERANCE - ±10mm

This drawing & design is the property of NIHVA TECHNOLOGIES. Not to be sold or copied to any other concern.

TITLE: DECK CYL TOP PIN			NIHVA TECHNOLOGIES PVT. LTD. PUNE Tel : 020 66304033 Email:- info@nihva.com Website:- www.nihva.com
NAME	SIGN	DATE	
DRAWN P.A			CLIENT -
CHECK SHEKHAR			PROJECT - DLBJ1001
APPRD. SHEKHAR			SITE LOCATION -
If any queries contact : design@nihva.com			DWG. NO. : NIHVA/17-18/ REV- 0
ALL DIMENSION ARE IN mm			SCALE: NTS WT: SHEET: 01 OF 01