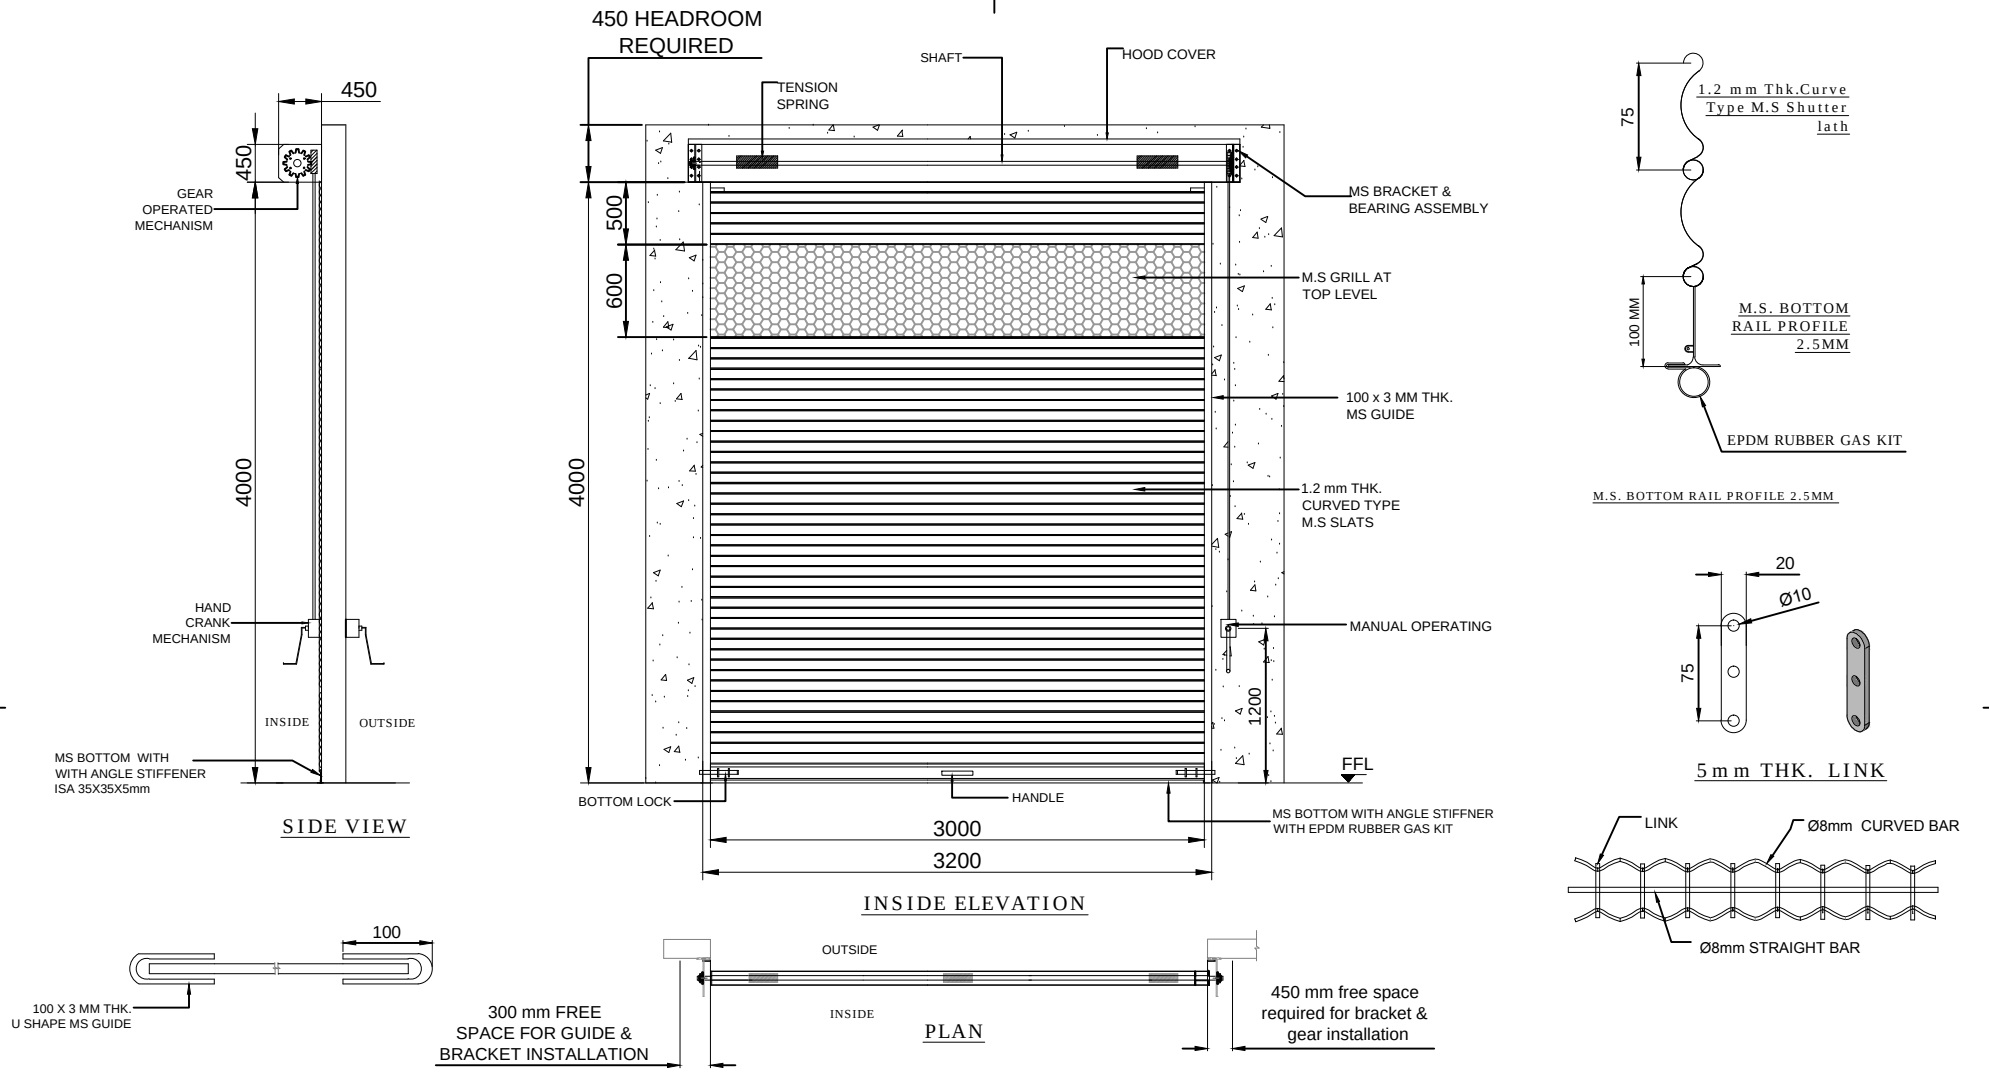


TOLERANCE - ±10mm

QTY : 7 NOS

NOTE-
1. ALL CIVIL WORK WILL BE CLIENT'S SCOPE.
2.STRUCTURE REQUIRED FOR SHUTTER IS IN CLIENT'S SCOPE.
3.**PAINT -** 2 COATS (EACH COAT OF 35 MICRONS DFT) OF EPOXY POLYAMIDE-BASED ENAMEL FINISH OF APPROVED COLOR RAL 9010 AND MAKE OVER A COAT (EACH ONE COAT 25 MICRONS DFT) OF EPOXY POLYAMIDE BASED RED OXIDE ZINC PHOSPHATE PRIMER.

This drawing & design is the property of NIHVA TECHNOLOGIES. Not to be sold or copied to any other concern.

TITLE	GEAR OPERATED ROLLING SHUTTER 3m X 4 m Right side gear box.		
	NAME	SIGN	DATE
DRAWN	P.A		23.12.2019
CHECK	G.J		23.12.2019
APPRD.			

NIHVA TECHNOLOGIES PVT. LTD.
NIHVA TECHNOLOGIES PVT. LTD. PUNE
Tel : 020 66304033
Email:- info@nihva.com
Website:- www.nihva.com

CLIENT -
PROJECT -
SITE LOCATION -
If any queries contact : design@nihva.com
DWG. NO. : NIHVA/19-20/VDR/247
REV- R04
ALL DIMENSION ARE IN mm
SCALE: NTS
WT:
SHEET: 01 OF 01