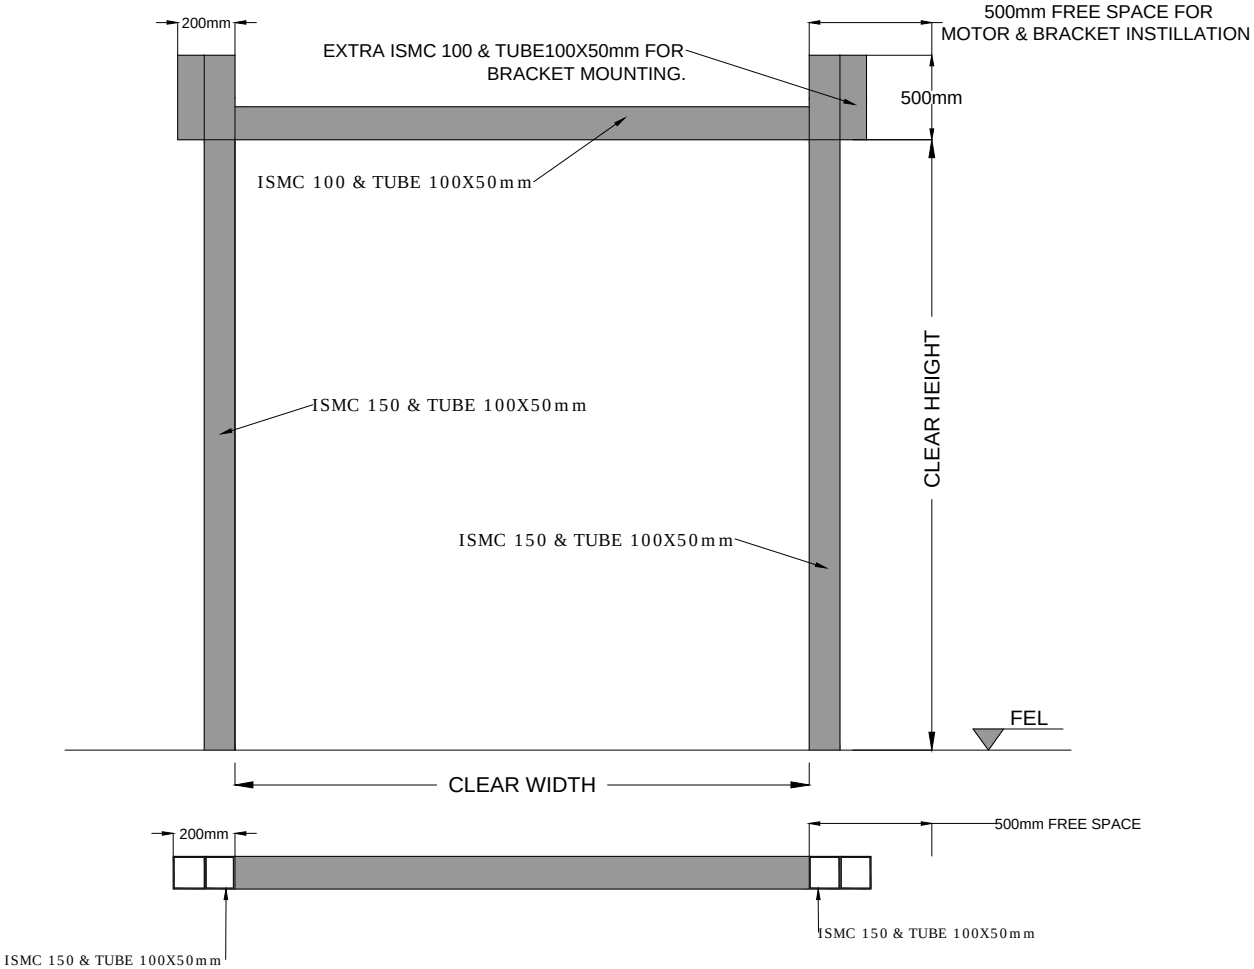


TOLERANCE - ±10mm

CLEAR WIDTH	CLEAR HEIGHT	QTY.
3000mm	3000mm	02 NOS
5000mm	5000mm	01 NOS
3000mm	3000mm	02 NOS

(NOTE: REQUIRED STRUCTURE FOR DOOR SHOULD BE IN CLIENT SCOPE.)

This drawing & design is the property of NIHVA TECHNOLOGIES. Not to be sold or copied to any other concern.

TITLE: MOTORISED ROLLING SHUTTER STRUCTURE.

	NAME	SIGN	DATE
DRAWN	SURAJ		21-08-2018
CHECK	PRADEEP		21-08-2018
APPRD.	R.D		21-08-2018

If any queries contact : design@nihva.com

ALL DIMENSION ARE IN mm

NIHVA TECHNOLOGIES PVT. LTD.
NIHVA TECHNOLOGIES PVT. LTD. PUNE
Tel : 020 66304033
Email:- info@nihva.com
Website:- www.nihva.com

CLIENT -DEVI CONSTRUCTION

PROJECT -

SITE LOCATION - PUNE.

DWG. NO. : NIHVA/18-19/0110 | REV- 0

SCALE: NTS | WT: | SHEET: 01 OF 01