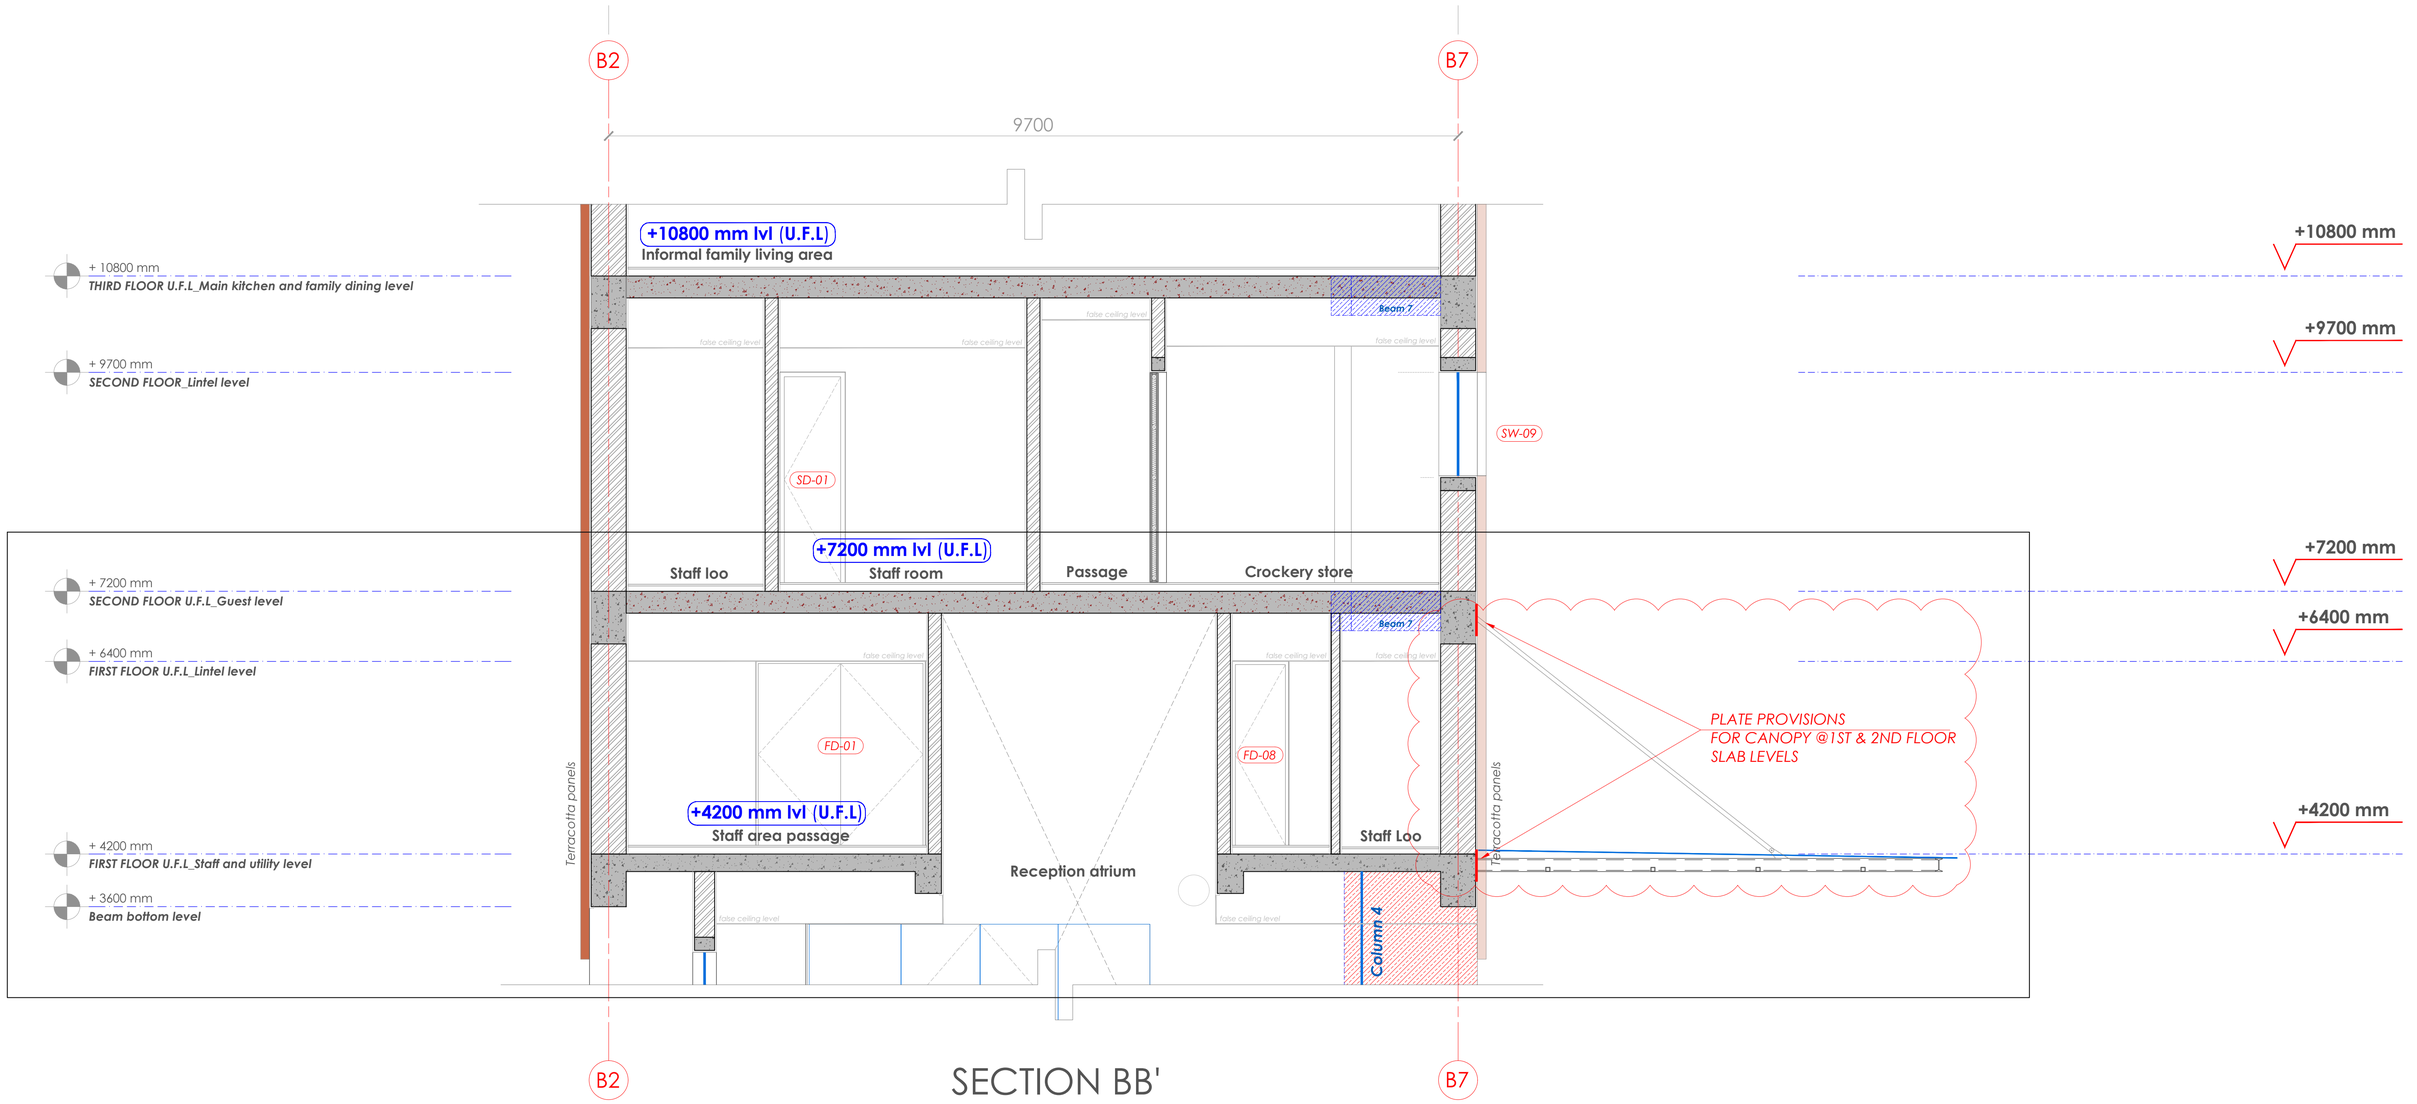

B2
B7
9700
+10800 mm lvl (U.F.L)
Informal family living area
+ 10800 mm
THIRD FLOOR U.F.L_Main kitchen and family dining level
+ 9700 mm
SECOND FLOOR_Lintel level
Beam 7
false ceiling level
SW-09
SD-01
+7200 mm lvl (U.F.L)
Staff loo
Staff room
Passage
Crockery store
+ 7200 mm
SECOND FLOOR U.F.L_Guest level
+ 6400 mm
FIRST FLOOR U.F.L_Lintel level
FD-01
FD-08
Terracotta panels
+4200 mm lvl (U.F.L)
Staff area passage
Reception atrium
Staff Loo
Column 4
PLATE PROVISIONS
FOR CANOPY @1ST & 2ND FLOOR
SLAB LEVELS
+ 4200 mm
FIRST FLOOR U.F.L_Staff and utility level
+ 3600 mm
Beam bottom level
+10800 mm
+9700 mm
+7200 mm
+6400 mm
+4200 mm

SECTION BB'