



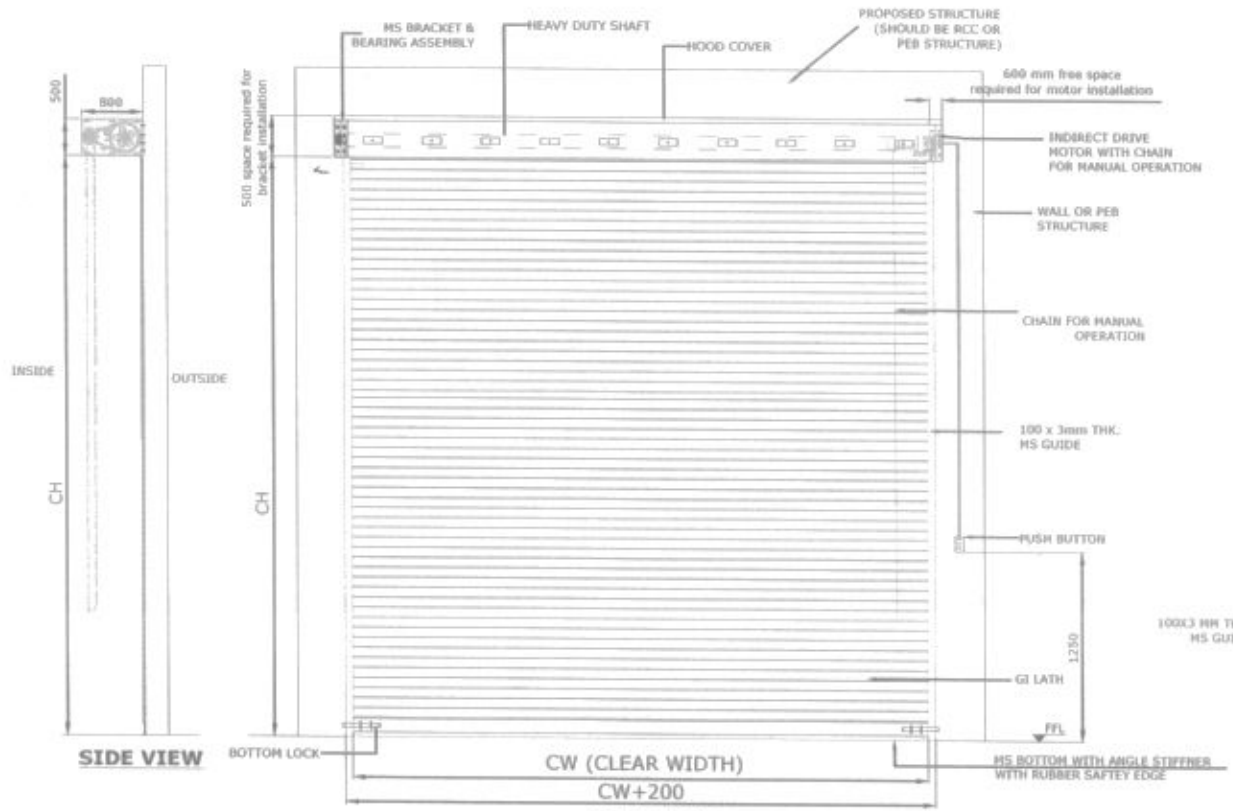



Shapoorji Pallonji & Co. Pvt. Ltd. Mahindra Tower project.

Skhanhan approved.

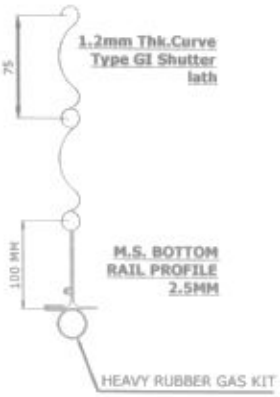

CLEAR WIDTH (CW)	CLEAR HEIGHT (CH)	QUANTITY
4000	4000	01 NO

TOLERANCE:±10mm

REV:-19-6-2018
I-SLAT THK. CHANGED 1mm TO 1.2mm

This drawing & designing is the property of NIHVA TECHNOLOGIES. Not to be sold or copied to any other concern.

TITLE: MOTORISED ROLLING SHUTTER

NIHVA TECHNOLOGIES PVT. LTD.

NIHVA TECHNOLOGIES PVT. LTD. PUNE
Tel : 020 66304033
Email:- info@nihva.com
Website:- www.nihva.com

	SIGN	DATE
DRAWN	SURAJ	02.06.18
CHECK	PRADEEP	02.06.18
APPROVAL	PRADEEP	02.06.18
RFG.		

If any queries contact : design@nihva.com

ALL DIMENSION ARE IN mm

CLIENT - Shapoorji Pallonji and Co.Pvt Ltd

PROJECT -

SITE -

DWG. NO. : NIHVA/18-19/0050/R01 | REV-01

SCALE: NTS | WT: | SHEET: 01 OF 01