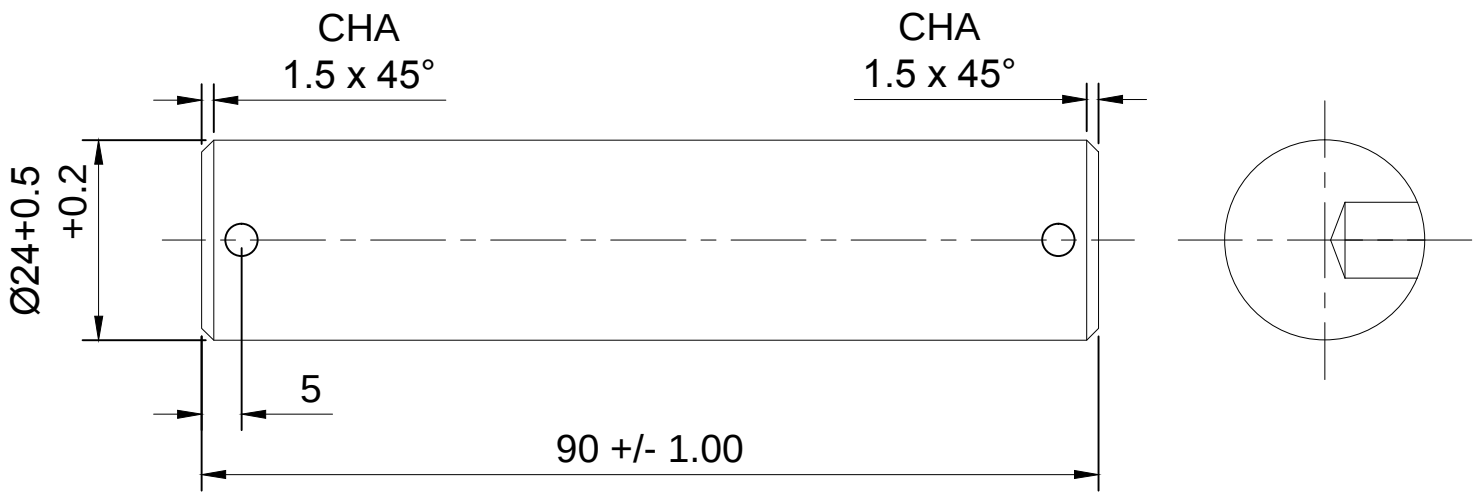


NOTE:~ MTL : EN8

Ø24 X 93L = 02 NOS (HARDENING & GRINDING)

This drawing & design is the property of NIHVA TECHNOLOGIES. Not to be sold or copied to any other concern.

TITLE: MAINTENANCE STOPPER			NIHVA TECHNOLOGIES PVT. LTD. PUNE Tel : 020 66304033 Email:- info@nihva.com Website:- www.nihva.com
	NAME	SIGN	DATE
DRAWN	PRADEEP		05.09.2018
CHECK	PRADEEP		05.09.2018
APPRD.	PRADEEP		05.09.2018
If any queries contact : design@nihva.com			
ALL DIMENSION ARE IN mm			

CLIENT -		
PROJECT - DLSD1010		
SITE LOCATION -		
DWG. NO. : NIHVA/18-19/MFG/DLSD1010/014		
SCALE: NTS	WT:	REV- 0