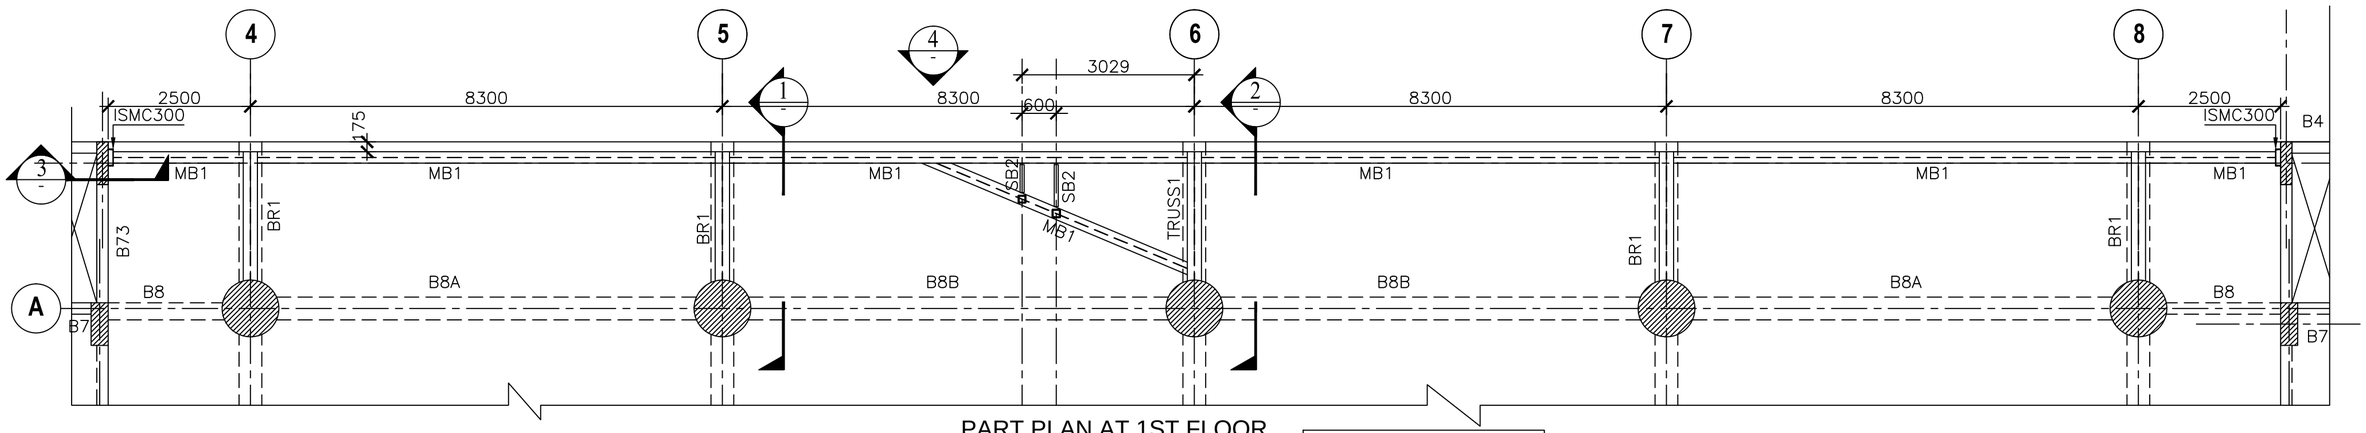

PART PLAN AT 1ST FLOOR

(SCALE 1:100)

NOTE:– *DISTANCE SHALL BE VERIFY BY DOOR VENDOR DRAWING

STEEL BEAM
SB2–TUBE 70x70x4THK.

NOTE:– LOADING CONSIDER REFER DRG. NO 62170