




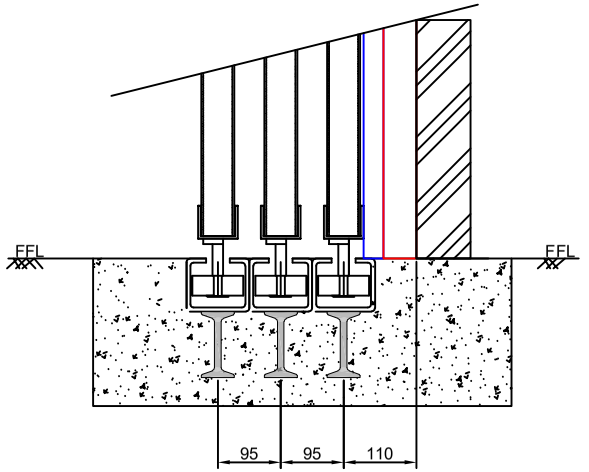

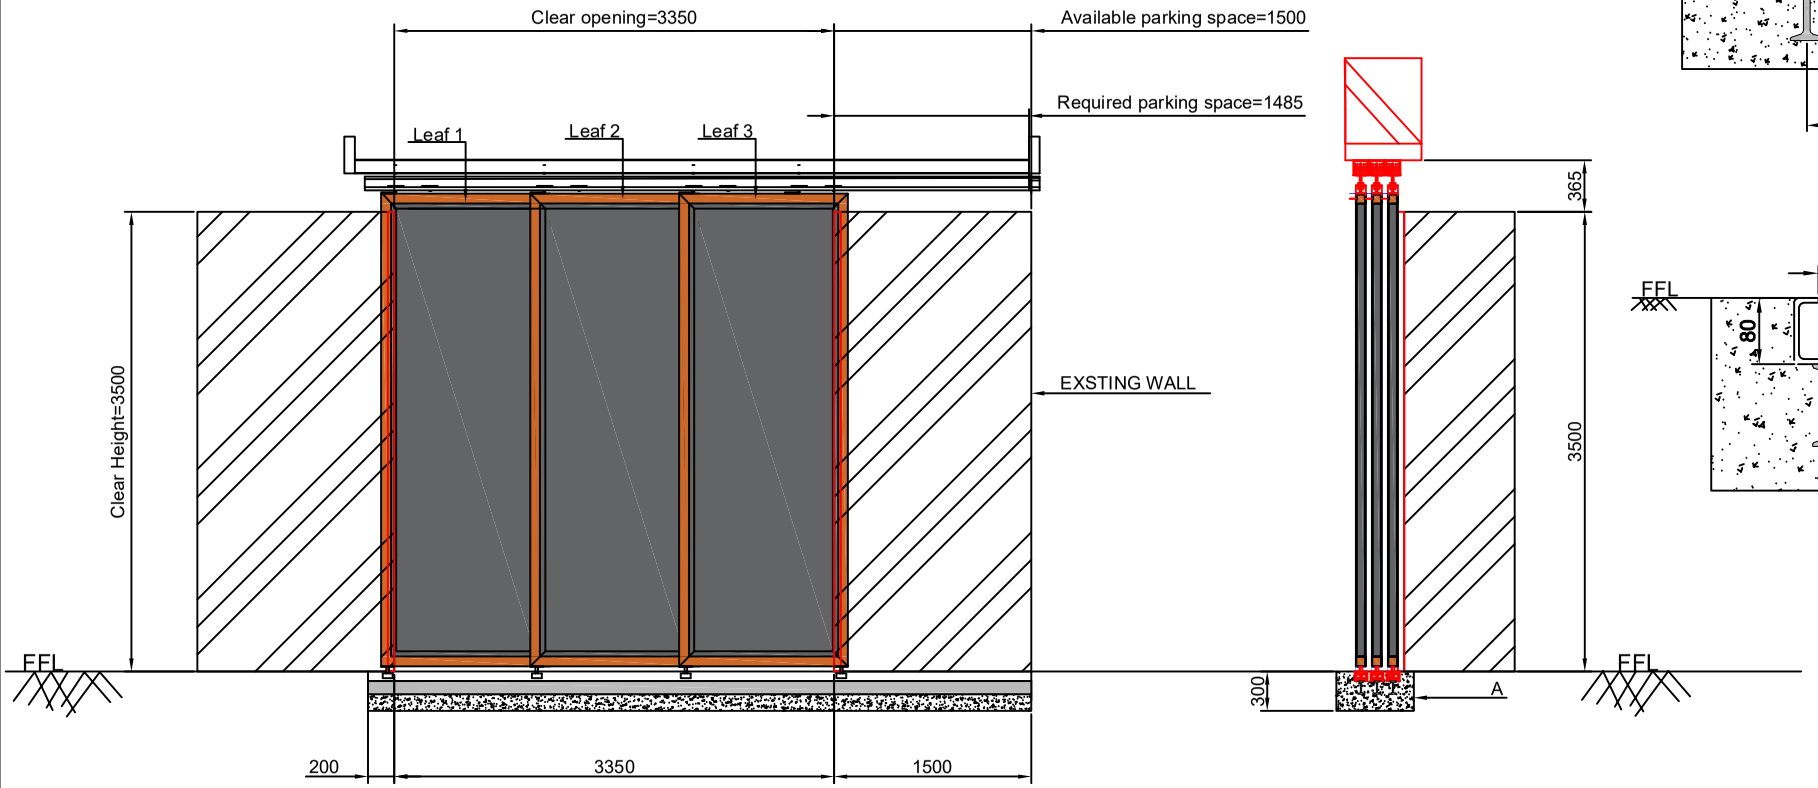

Deatil A

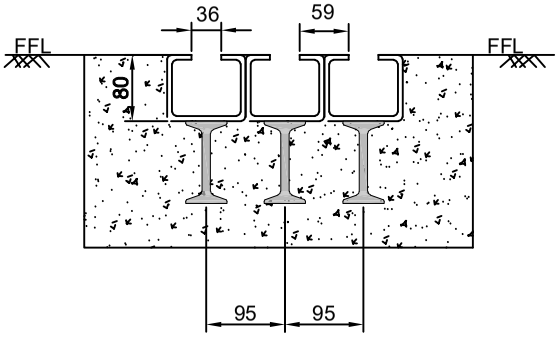

Client scope
*Roof need to be shift at top Approx 300mm *Drainage area need to be remove frome left side appox.200mm *Gutter area need to be remove *Civil foundation need to be done for tracks

Note:-

1.All dimension are in MM

2.Manufacturing,civil and installation tolerance will be ±10mm

3.Top and Bottom track should be in parallal within ±3mm

This drawing & design is the property of NIHVA TECHNOLOGIES. Not to be sold or copied to any other concern.

TITLE:-3LEAF RIGHT SIDE
CRM-04

NIHVA
NIHVA TECHNOLOGIES PVT. LTD.
NIHVA TECHNOLOGIES PVT. LTD. PUNE
Tel : 020 66304033
Email:- info@nihva.com
Website:- www.nihva.com

	NAME	DATE	SIGN
DRAWN	SUJATA	26/04/2022	
CHECK	M.SUTAR	26/04/2022	
APPRD.	V.TARAK	26/04/2022	

CLIENT - LESTECH			
LOCATION - POSCO MANGAON			
PRODUCT - SLIDING DOOR			
If any queries contact : design@nihva.com	DWG NO:-NIHVA/22-23/CLT/0018		REV- 0
ALL DIMENSION ARE IN mm	SCALE: NTS	SCALE:-- 1:1	SHEET: 01 OF 01

Rev No.	Revision	Date	Revised By