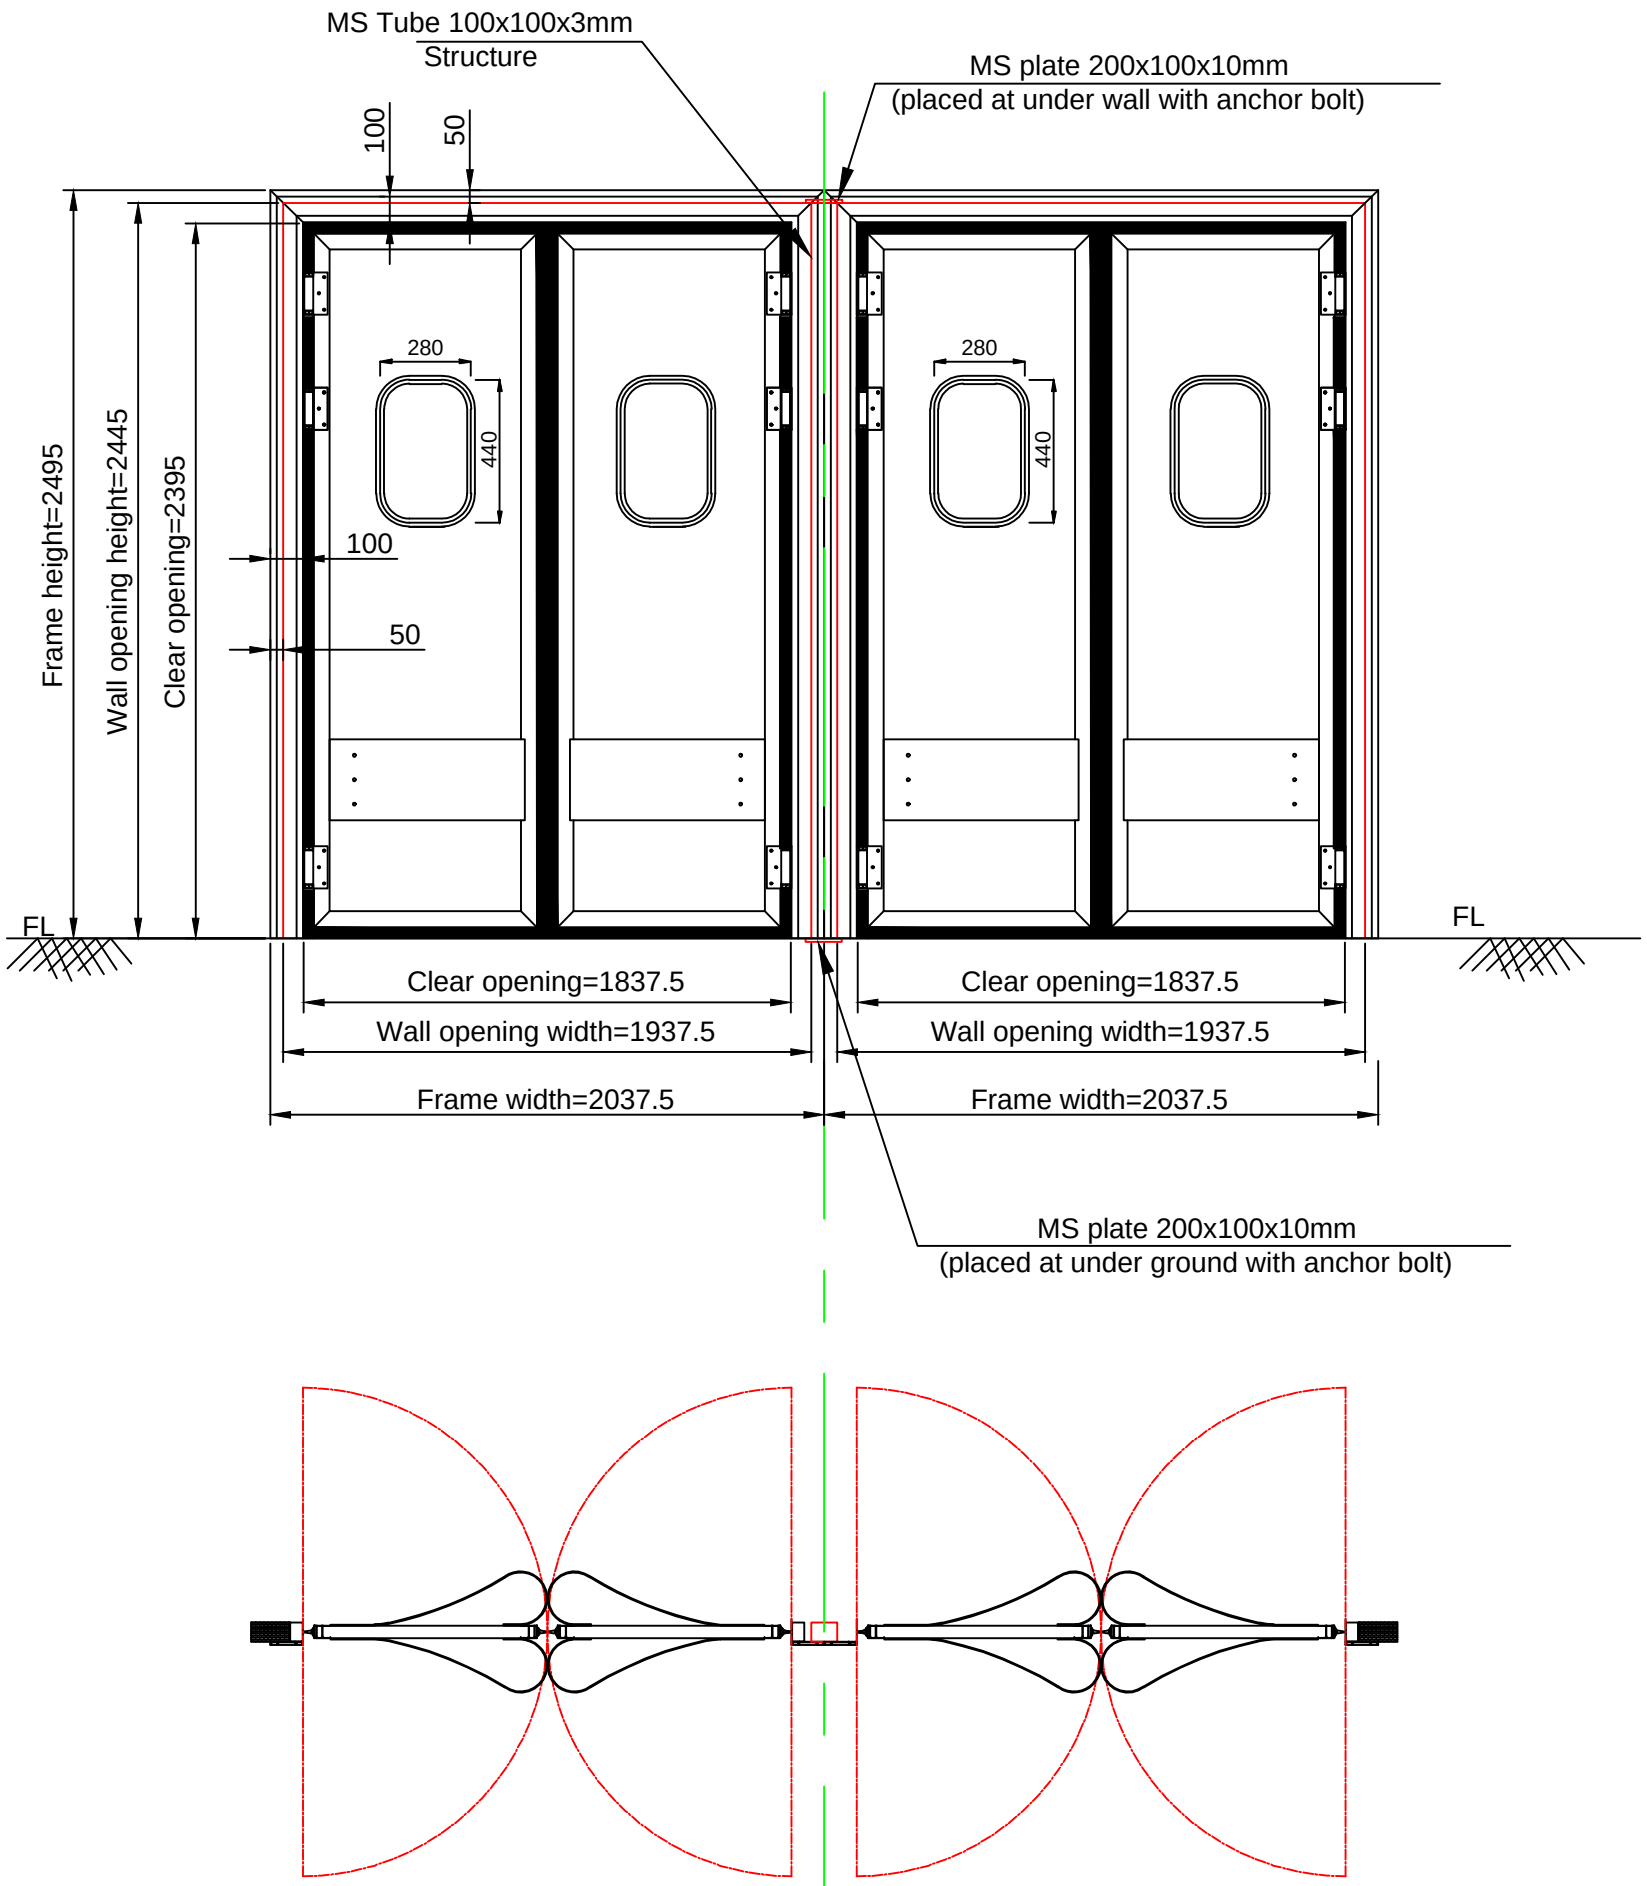

LEAF FINISH : PE / PCGI
LEAF THICKNESS : 40 MM
HINGES MOC : DOUBLE ACTION STAINLESS STEEL
VIEW WINDOW : 1 UNIT ON EACH LEAF
VIEW WINDOW HEIGHT : 440 MM
VIEW WINDOW WIDTH : 280 MM
VIEW WINDOW POSITION FROM FFL : 1500 MM

Note:

1.All dimension are in mm

2.All Civil work and structure will be in client scope

3.Structure place at the front side(same line in existing wall)

Rev No.	Revision	Date	Revised By

This drawing & design is the property of NIHVA TECHNOLOGIES. Not to be sold or copied to any other concern.

TITLE:- NIHVA Make NFF3 Flip Flap Door

	NAME	DATE	SIGN
DRAWN	G.P	26-03-2022	
CHECK	P.J	26-03-2022	
APPRD.	A.K.	26-03-2022	

NIHVA TECHNOLOGIES PVT. LTD.
NIHVA TECHNOLOGIES PVT. LTD. PUNE
Tel : 020 66304033
Email:- info@nihva.com
Website:- www.nihva.com

If any queries contact : design@nihva.com

ALL DIMENSION ARE IN mm

CLIENT - NIHVA TECHNOLOGIES

LOCATION - PUNE

PRODUCT - FLIP FLAP DOOR

DWG NO:-NIHVA/21-22/VDR/062 | REV- 00

SCALE: NTS | SCALE:-- 1:1 | SHEET: 01 OF 01