


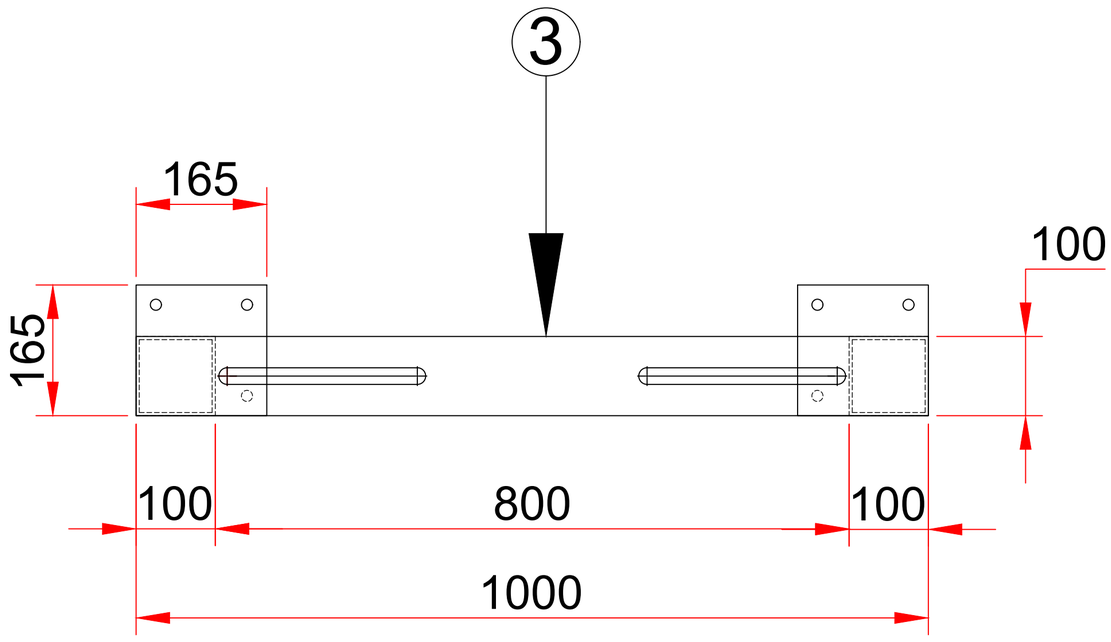


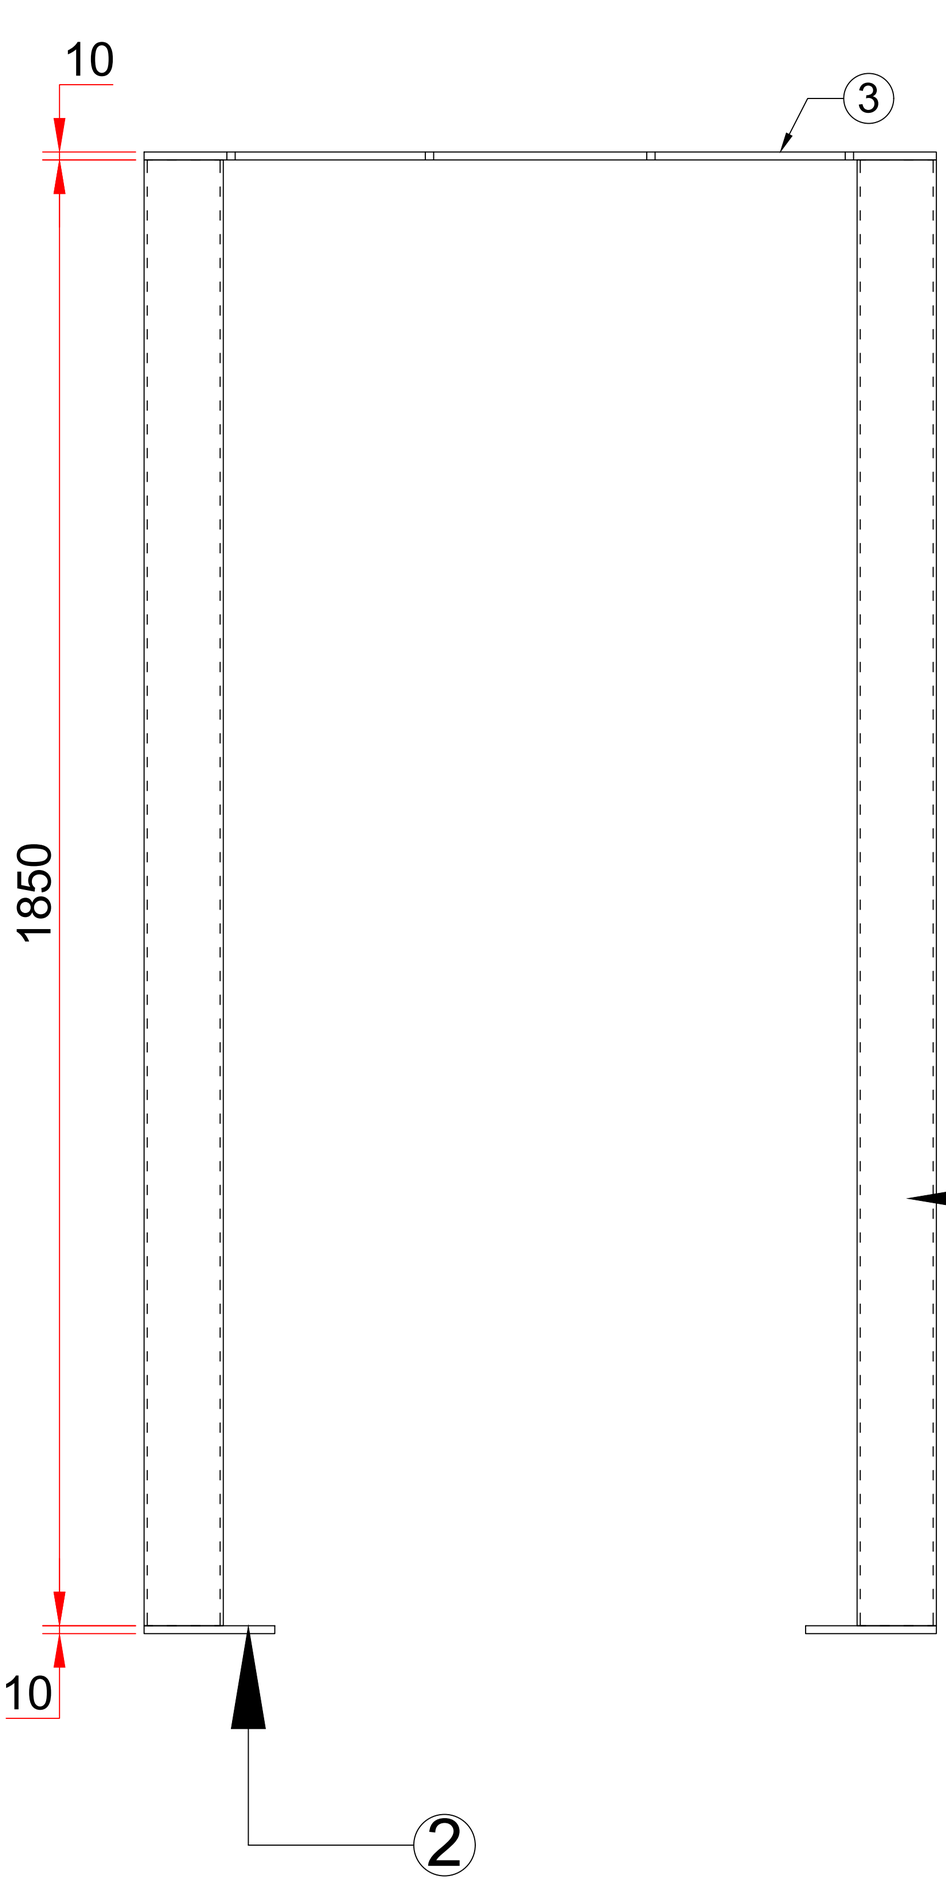

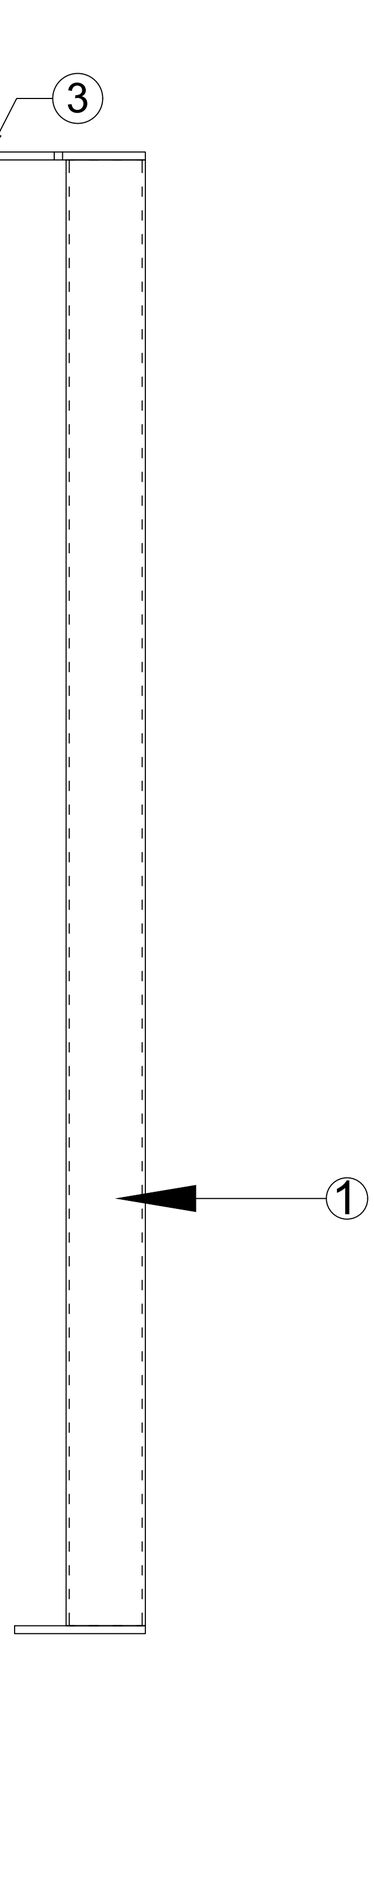

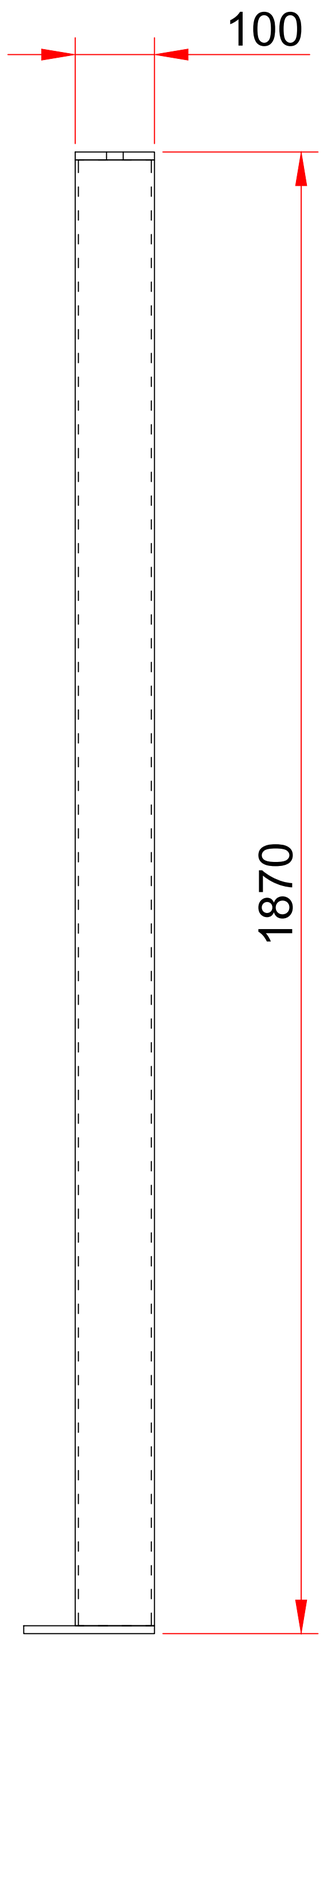

BOM FOR POST			
SL NO.	DESCRIPTION	SPECIFICATION	QTY
1	MS SQ. TUBE	100X100X5X1850L	2 NOS
2	POST SUPPORT PLATE	165X165X10THK	2 NOS
3	ROLLER SUPPORT PLATE	1000X100X10THK	1 NOS

Rev No.	Revision	Date	Revised By

This drawing & design is the property of NIHVA TECHNOLOGIES. Not to be sold or copied to any other concern.

	NAME	DATE	SIGN
DRAWN	MAHESH S.	13/08/2022	
CHECK	MAHESH S.	13/08/2022	
APPRD.	AMIT K.	13/08/2022	

TITLE:- POST

NIHVA TECHNOLOGIES PVT. LTD.
NIHVA TECHNOLOGIES PVT. LTD. PUNE
Tel : 020 66304033
Email:- info@nihva.com
Website:- www.nihva.com

CLIENT - NAVNEET EDUCATION LTD.

LOCATION - PALGHAR

PRODUCT - End Post1 | QTY:-2 NO

If any queries contact : design@nihva.com | DWG NO:-NIHVA/22-23/MFG/0063 | REV- 0

ALL DIMENSION ARE IN mm | SCALE: NTS | SCALE:-- 1:1 | SHEET: 01 OF 01