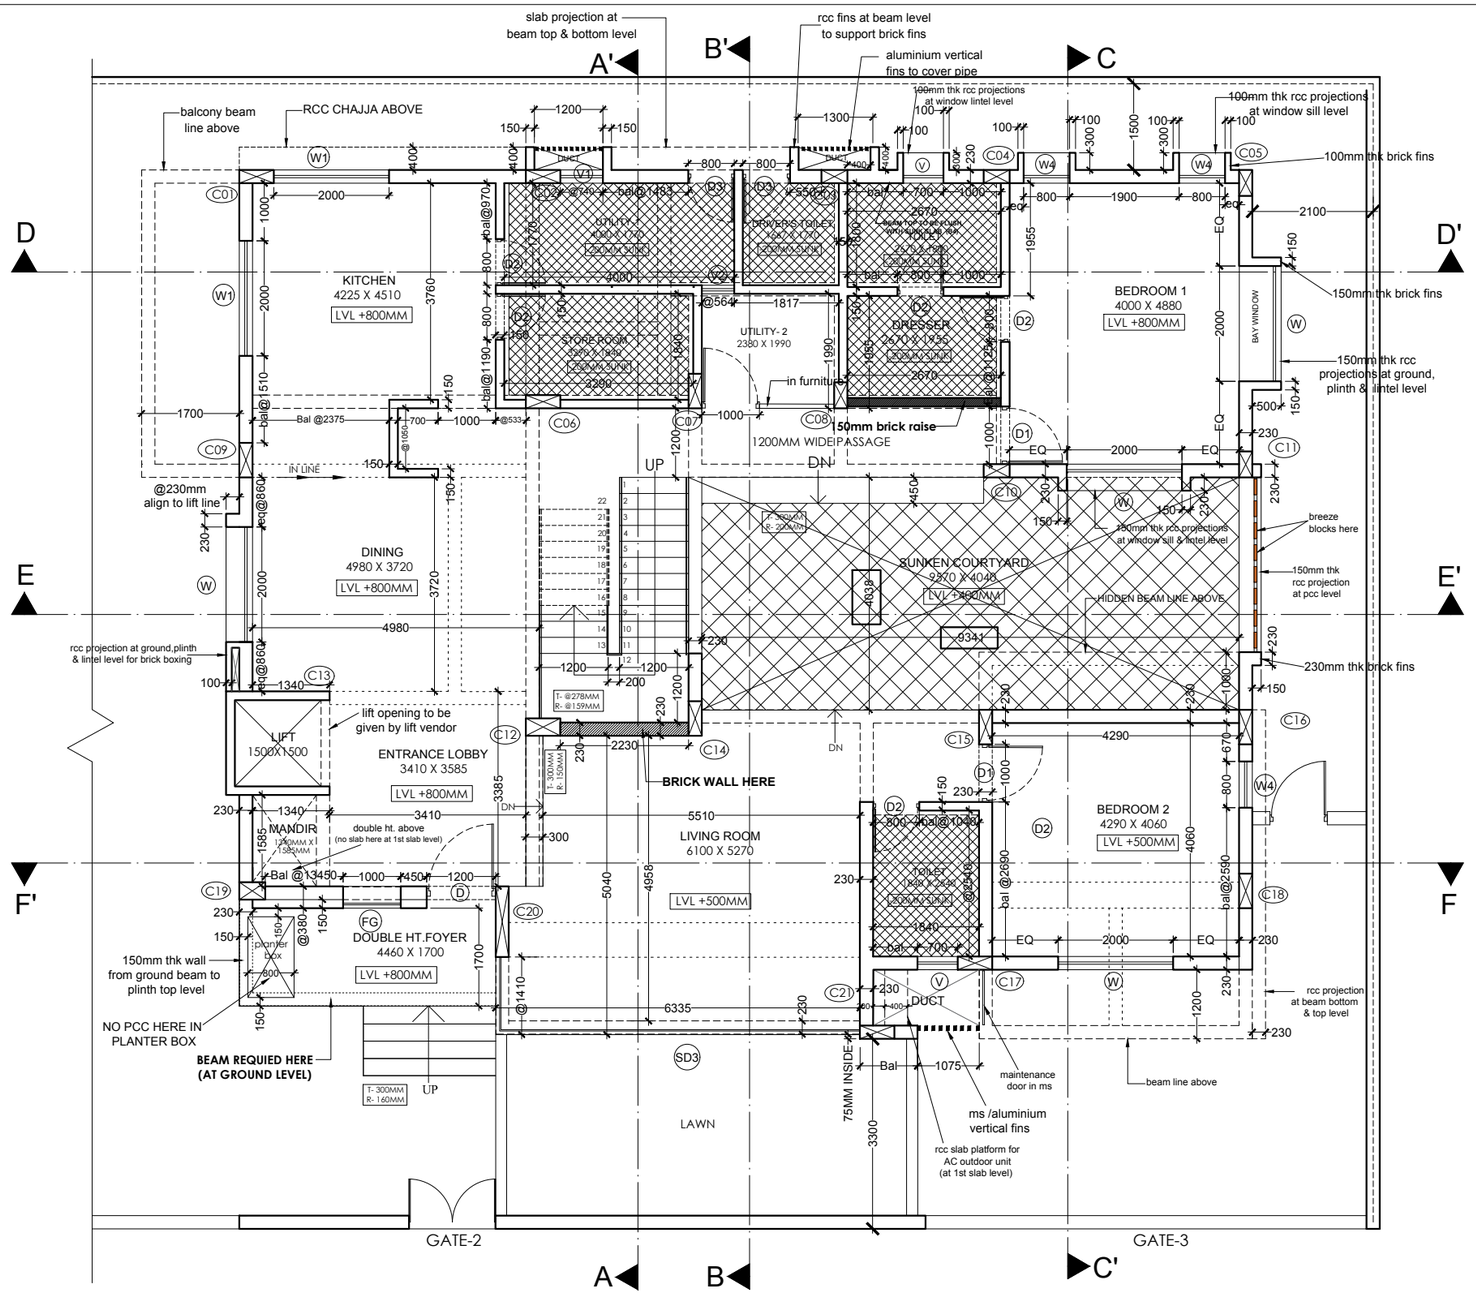


THESE DIMENSIONS ARE NET AVAILABLE AFTER PLASTER THICKNESS

SCHEDULE OF OPENING

DOOR	SIZE	LINTEL LVL
D	1200 X 2400	2400
D1	1000 X 2400	2400
D2	800 X 2400	2400
D3	800 X @2700	(upto beam bottom)
SD	3000 X 2400	2400
SD1	2000 X 2400	2400
SD2	5500 X 2400	2400
SD3	@6100 X 3000	3000

WINDOW	SIZE	SILL LVL	LINTEL LVL
W	2000 X 2000	400	2400
W1	2000 X 1200	1200	2400
W2	1000 X @2650	400	upto beam
W3	800 X 2000	400	2400
W4	800 X 1500	900	2400
V	700 X 1200	1200	2400
V1	@740 X 1200	1200	2400
V2	@564 X 1200	1200	2400
FG	1000 X @2500	400	beam bottom
FG1	1000 X @3060	beam top	beam bottom

GFC

TITLE:-	NOTES:-	DATE	02/02/2024	NORTH	
REVISED GROUND FLOOR WORKING DRAWING		DRAWN BY	RAHEEN	N	
CLIENT:-		CHKD. BY	KMM		
MR. DEEPAK AHUJA		SCALE	1:100		
AT PUNE					

www.aakasadesigns.com
ARCHITECT KUMAAR MANGWANI
studio@aakasadesigns.com
302, Balewadi -37, Balewadi, Pune- 411045