

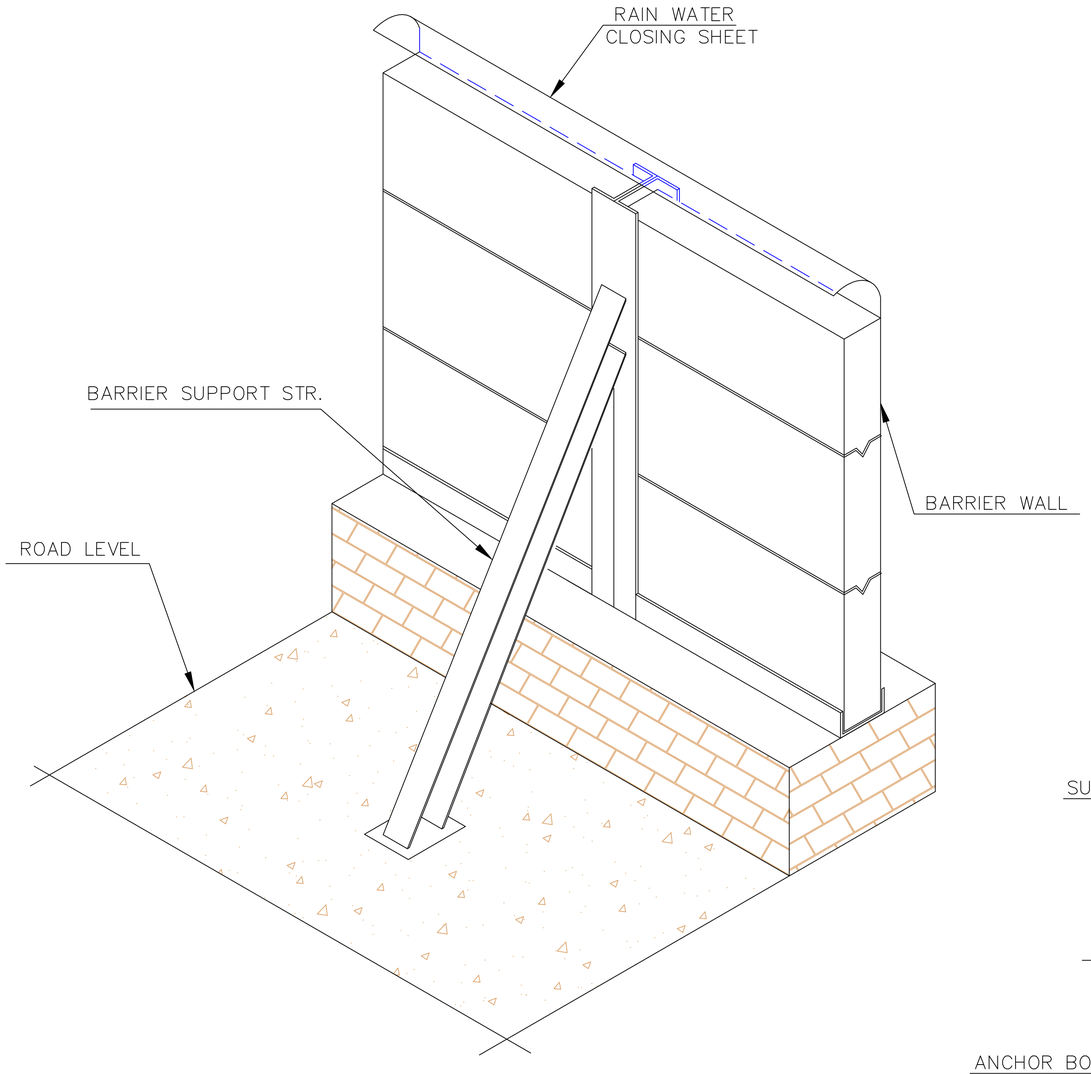



ELEVATION SECTION VIEW

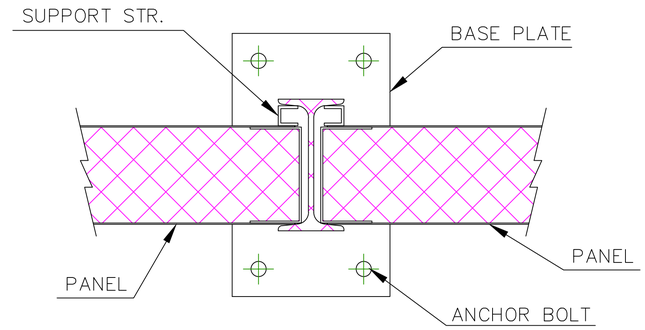


PLAN VIEW

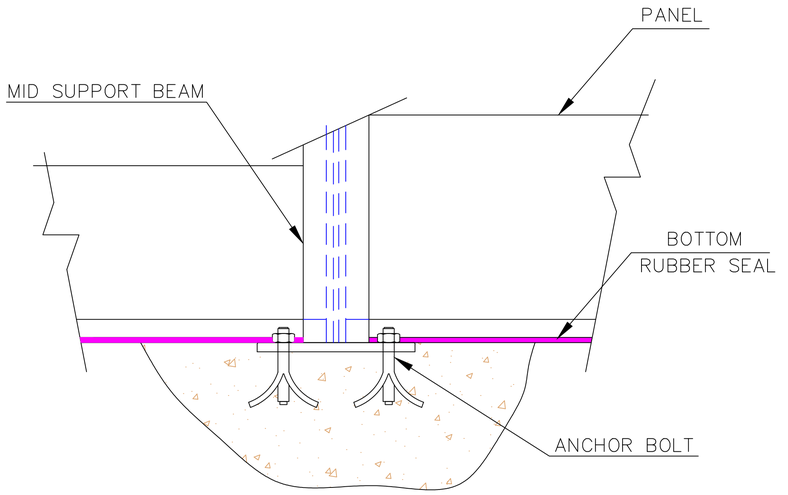

MOUNTING ARRANGEMENT

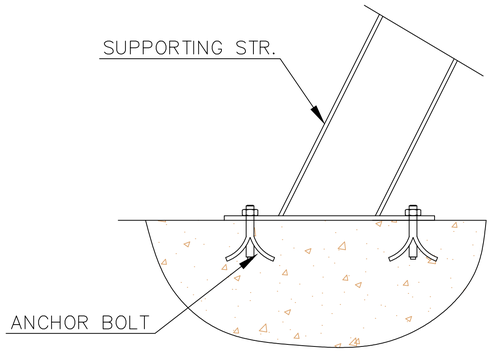

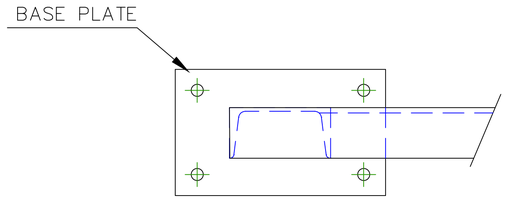

PANEL SUPPORTING STR.DETAIL

This drawing & design is the property of NIHVA TECHNOLOGIES. Not to be sold or copied to any other concern.

TITLE	SOUND BARRIER MOUNTING DETAIL		NIHVA TECHNOLOGIES PVT. LTD. PUNE Tel : 020 66304033 Email:- info@nihva.com Website:- www.nihva.com
	SIGN	DATE	
DRAWN	SURAJ	08/08/17	CLIENT -LUPIN
CHECK	SAGAR P.	08/08/17	PROJECT -
APPROVAL	SHEKHAR	08/08/17	SITE -
REV.			DWG. NO. : NIHVA/17-18/0147
If any queries contact : projects@nihva.com			SCALE: NTS / WT: / SHEET: 01 OF 01
ALL DIMENSION ARE IN mm			