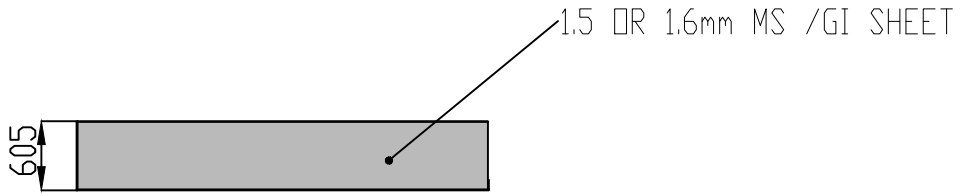

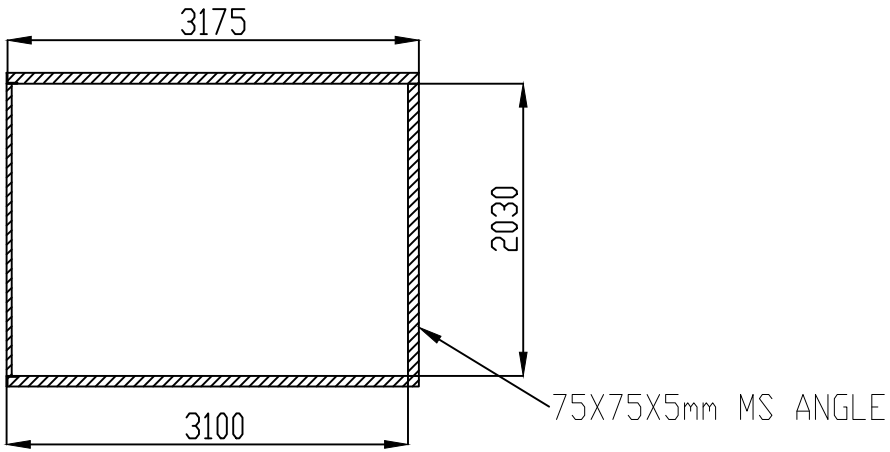

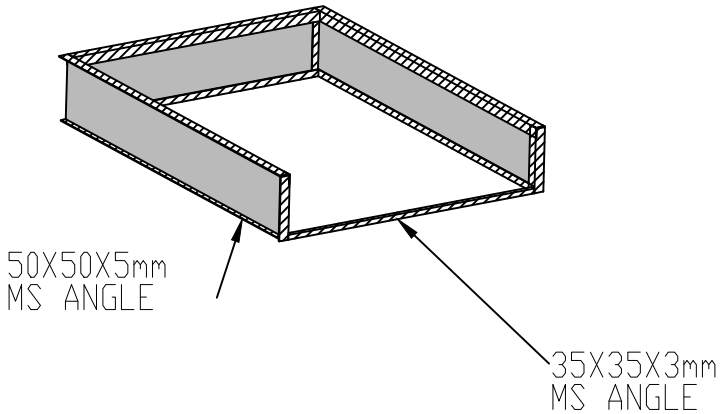

DIMENSION :

CLEAR WIDTH	CLEAR HEIGHT	QUANTITY

MATERIAL:

THICKNESS :

NIHVA TECHNOLOGIES PVT. LTD.

NIHVA TECHNOLOGIES PVT. LTD. PUNE
Email:- info@nihva.com
Website:- www.nihva.com

TITLE:

DOCK LEVELER PIT

CLIENT'S APPROVAL :

CLIENT - MW HIGH TECH PROJECTS INDIA PVT. LTD.

PROJECT -

SITE LOCATION -

DWG. NO. : NIHVA/16-17/142

SCALE: NTS	WT:	SHEET:1 OF 1
DRAWN BY: OMKAR		DATE: 15-02-2017
CHECK BY : SAGAR P.		DATE: 15-02-2017
APPROVED BY : R.K		DATE: 15-02-2017

If any queries contact : projects@nihva.com

NOTE: ALL DIMENSIONS ARE IN mm

THIS DRAWING & DESIGN IS THE PROPERTY OF NIHVA TECHNOLOGIES. NOT TO BE SOLD OR COPIED TO ANY OTHER CONCERN.