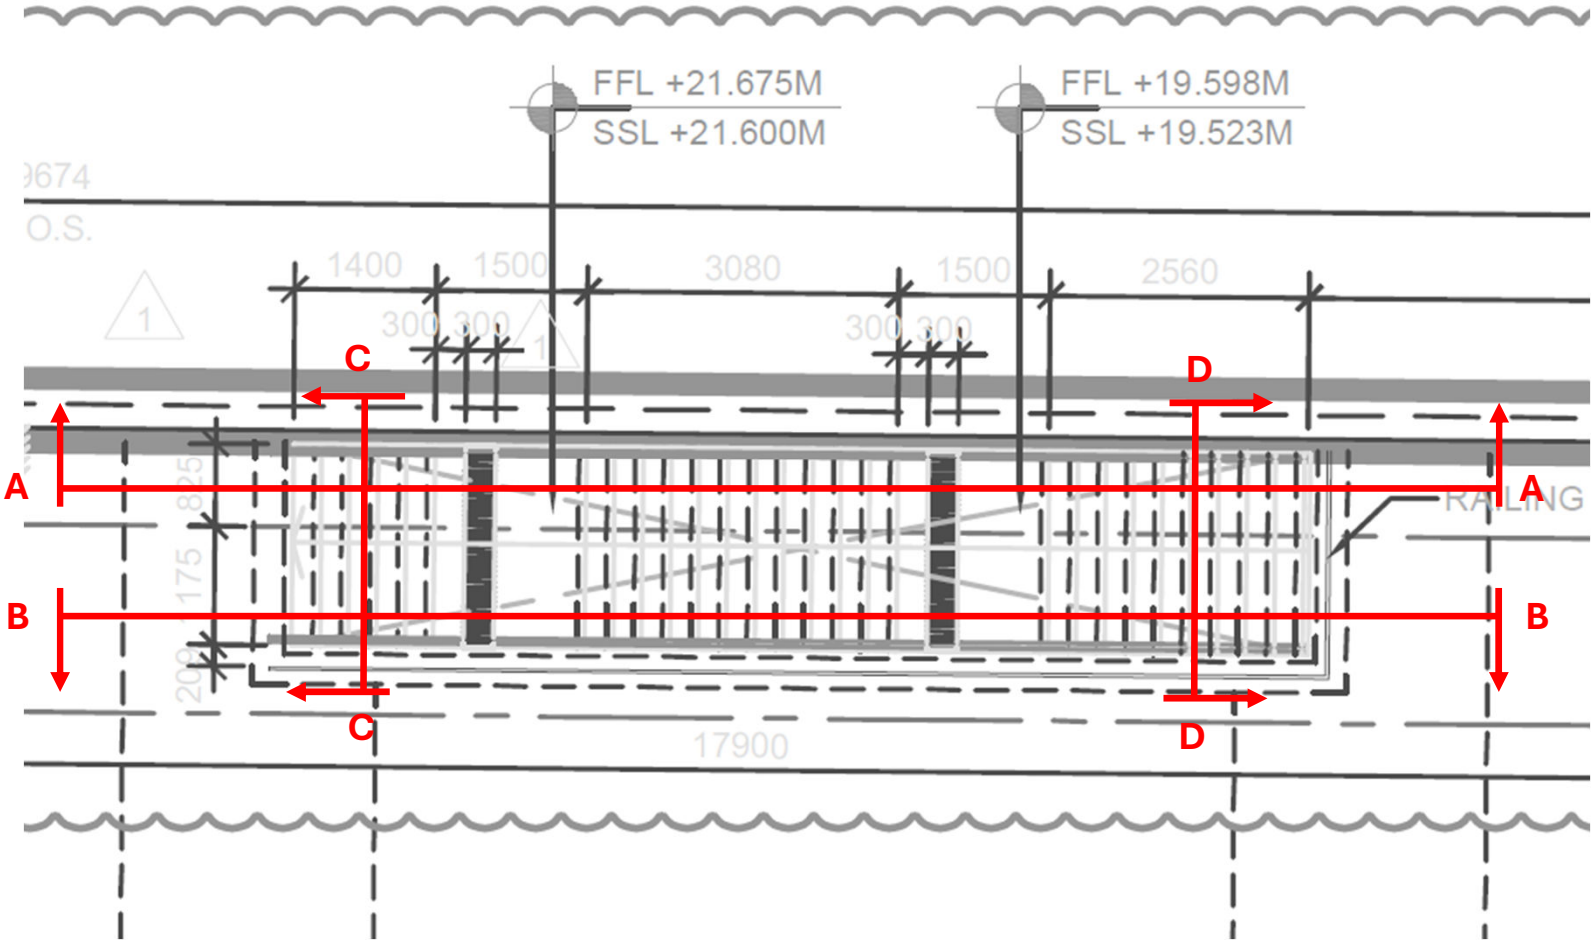
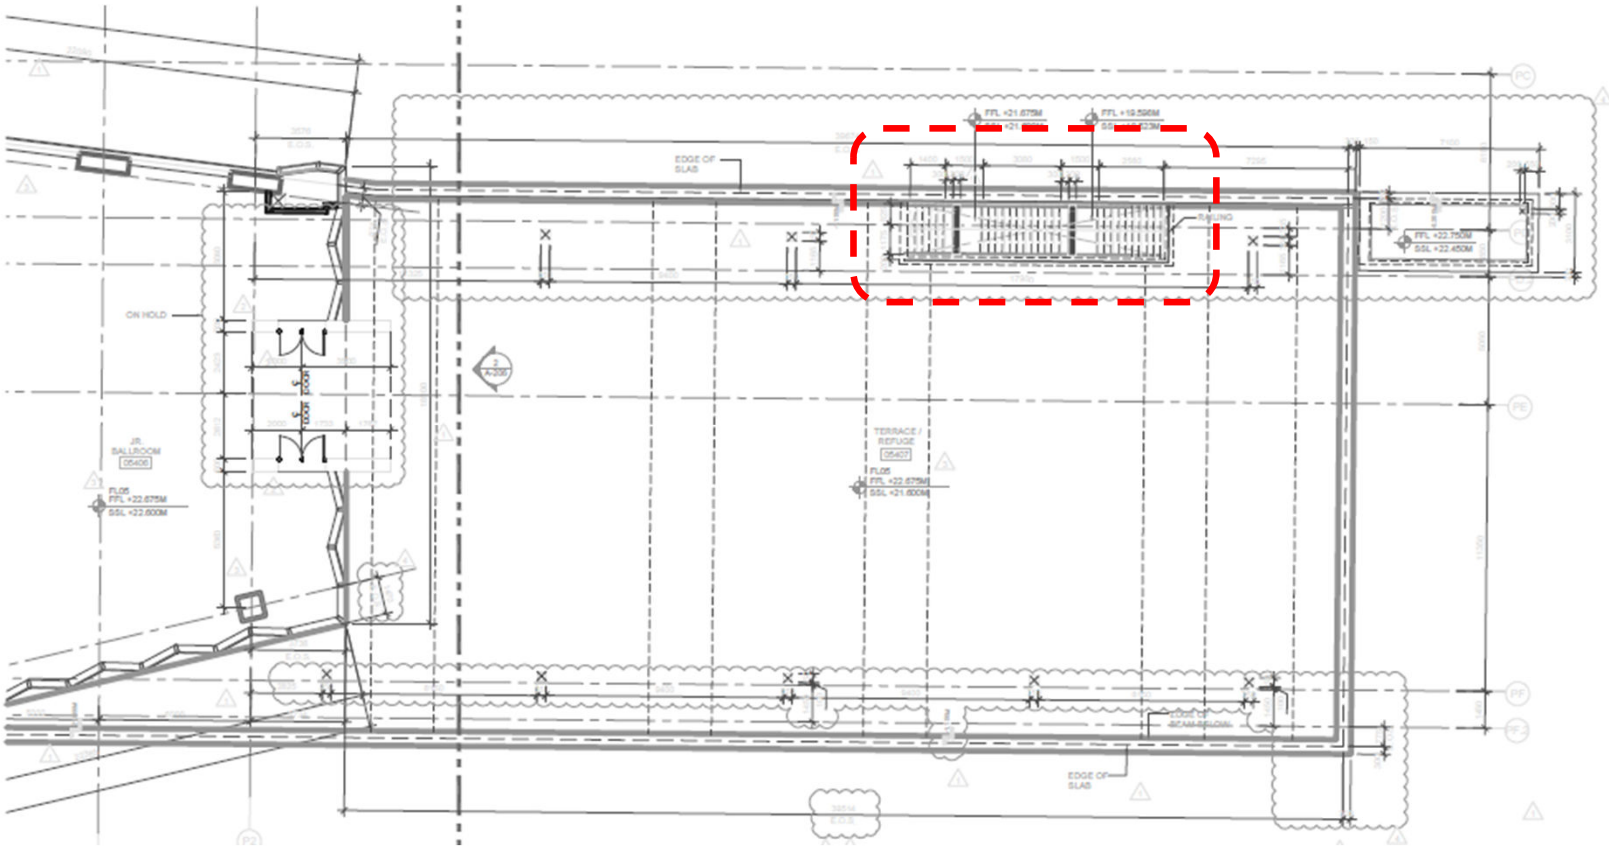

FFL +21.675M
SSL +21.600M
FFL +19.598M
SSL +19.523M
O.S.
1400
1500
3080
1500
2560
300
300
300
300
A
A
B
B
C
C
D
D
RAILING
17900


EDGE OF SLAB
RAILING
ON HOLD
JR. BALLROOM 05406
FL05 FFL +22.675M SSL +22.600M
TERRACE / REFUGE 05407
FL05 FFL +22.675M SSL +21.600M
FFL +22.750M SSL +22.450M
EDGE OF SLAB