


ELEVATION VIEW

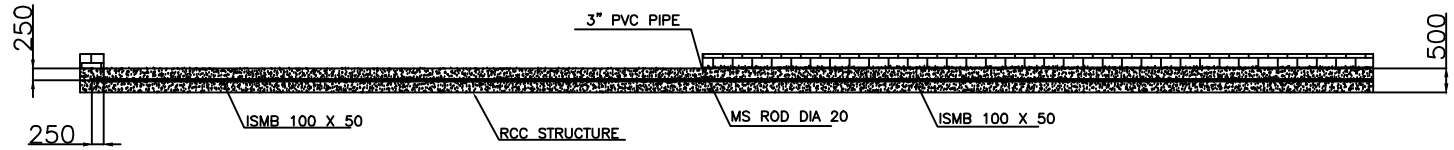

PLAN

Note-

1. All dimension are in mm.
2. All civil work is under client scope.
3. 3" PVC pipe in the foundation is in client scope
4. Power supply 3 phase 440v, 50hz.
5. Cable for power supply 2.5 sqmm 4 core
6. Cable for photocell - 1.5 sqmm 4 core

This drawing & design is the property of NIHVA TECHNOLOGIES. Not to be sold or copied to any other concern.

MOTORIZED SLIDING GATE				NIHVA TECHNOLOGIES PVT. LTD. PUNE Tel : 020 66304033 Email:- info@nihva.com Website:- www.nihva.com	
		SIGN	DATE		
DRAWN	S.B.		25/09/2021	CLIENT -M/s FUJI SILVERTECH CONCRETE P. LTD.	
CHECK	G.P.		25/09/2021	LOCATION - AURANGABAD	
APPRD.	A.K.		25/09/2021	PRODUCT - FOUNDATION DWG	
If any queries contact : projectsautomation@nihva.com				NIHVA\21-22\VDR\0236	REV- 00
ALL DIMENSION ARE IN mm				SCALE: NTS	SHEET: 01 OF 01