

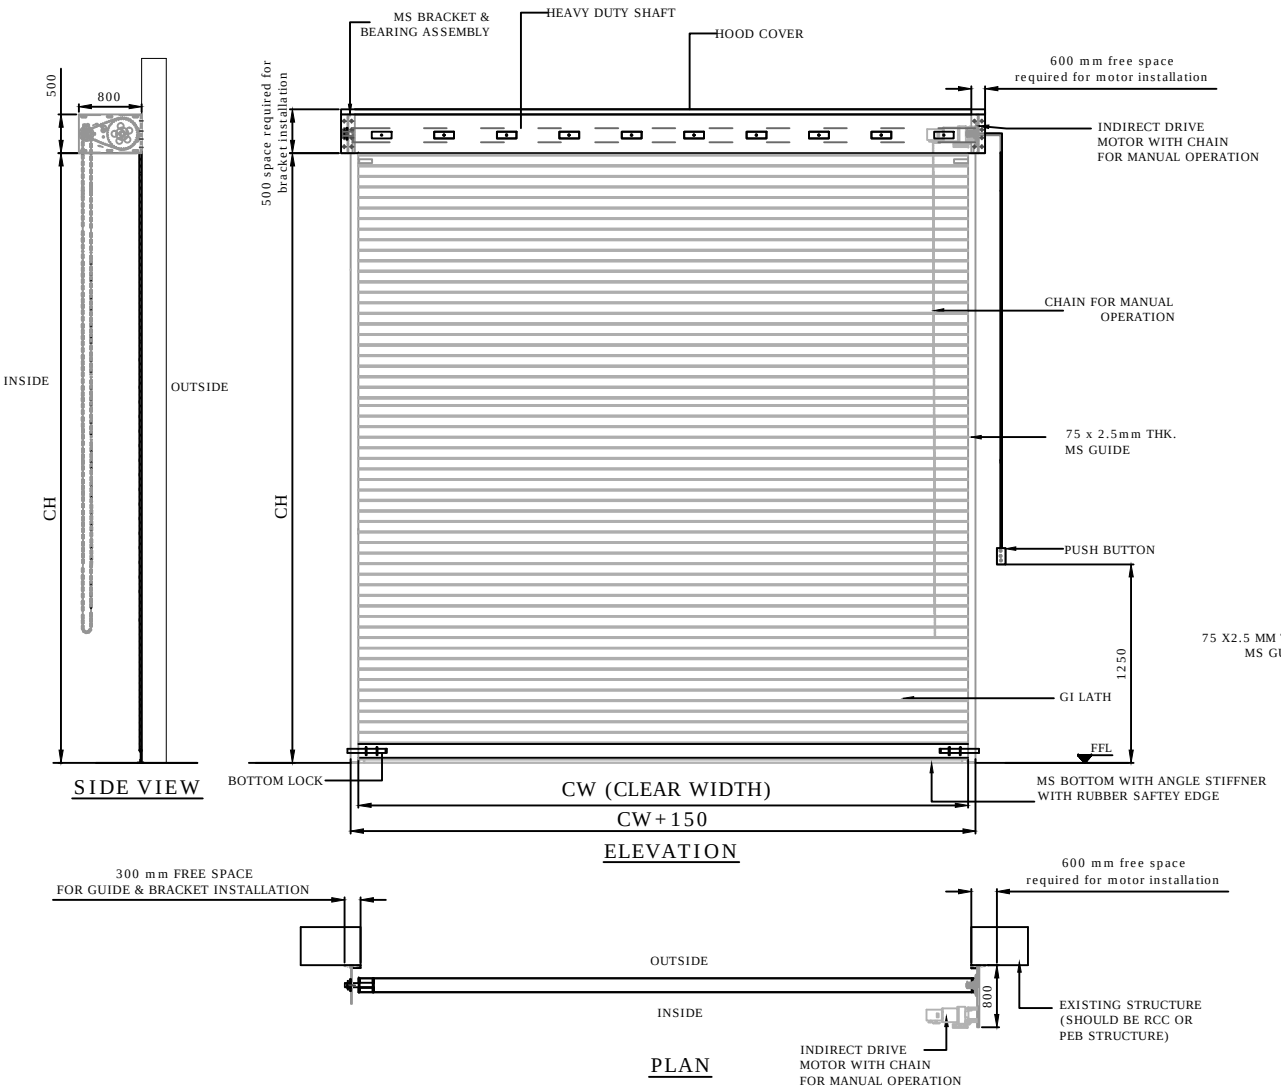


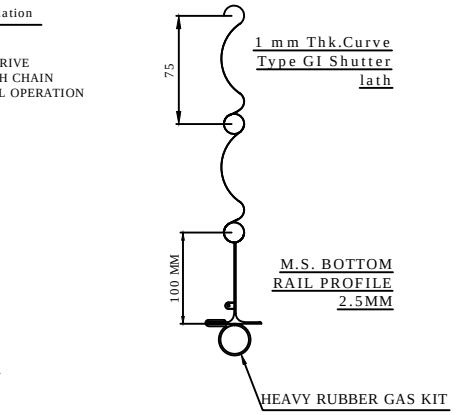

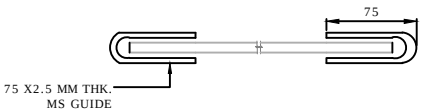

COLOR- RAL 5002 ULTRAMARINE BLUE

CLEAR WIDTH (CW)	CLEAR HEIGHT (CH)	QUANTITY
3000	3000	01 NOS

DIMENSION :

CLEAR WIDTH	CLEAR HEIGHT	QUANTITY
3000	3000	01 NOS

MATERIAL:

THICKNESS :

NOTE:
1.REQUIRED STRUCTURE FOR ROLLING SHUTTER WILL BE CLIENT'S SCOPE.
2.ONE COAT OF RED OXIDE PRIMER WILL BE GIVEN TO THE SHUTTER.
3.SINGLE PHASE. 3 CORE 1.5 SQ. CABLE REQUIRE AT SITE(CLIENT'S SCOPE).
4. COLOR OF SHUTTER WILL BE RAL 5002 ULTRAMARINE BLUE.

NIHVA TECHNOLOGIES PVT. LTD.
NIHVA TECHNOLOGIES PVT. LTD. PUNE
Email:- info@nihva.com
Website:- www.nihva.com

TITLE:

MOTORIZED ROLLING SHUTTER

CLIENT'S APPROVAL :

CLIENT - MASTPRO CONSULTING ENGINEERS PVT. LTD

PROJECT - MARS INTERNATIONALS INDIA PVT.LTD.

SITE LOCATION -PUNE.

DWG. NO. : NIHVA/17-18/0406 | REV. : 0

SCALE: NTS | WT: | SHEET:1 OF 1

		DATE	SIGN.
DRAWN	SURAJ	27-03-2018	
CHECK	OMKAR	27-03-2018	
APPRD.	SHEKHAR	27-03-2018	

If any queries contact : design@nihva.com

NOTE: ALL DIMENSIONS ARE IN mm

THIS DRAWING & DESIGN IS THE PROPERTY OF NIHVA TECHNOLOGIES. NOT TO BE SOLD OR COPIED TO ANY OTHER CONCERN.