

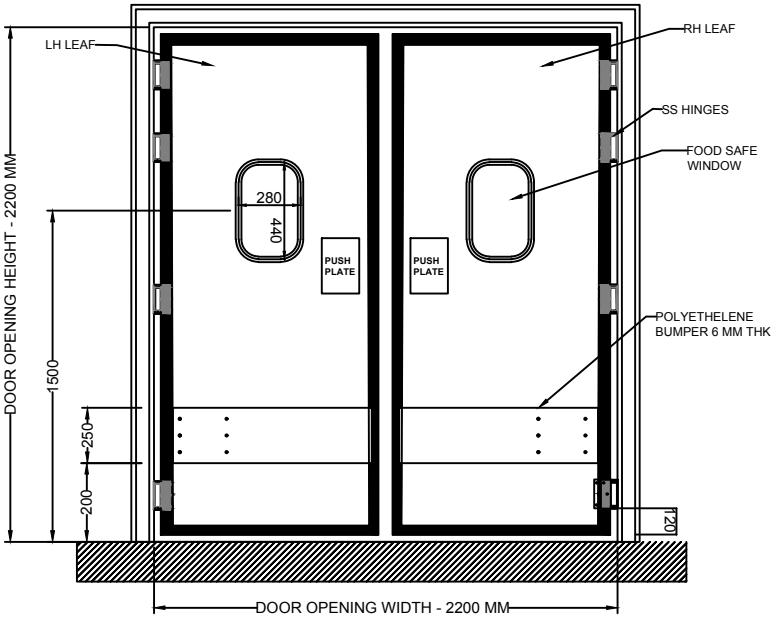


FRONT VIEW OF FLIP FLAP DOOR

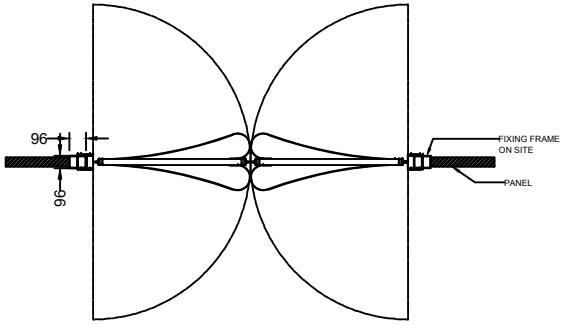

TOP VIEW OF FLIP FLAP DOOR

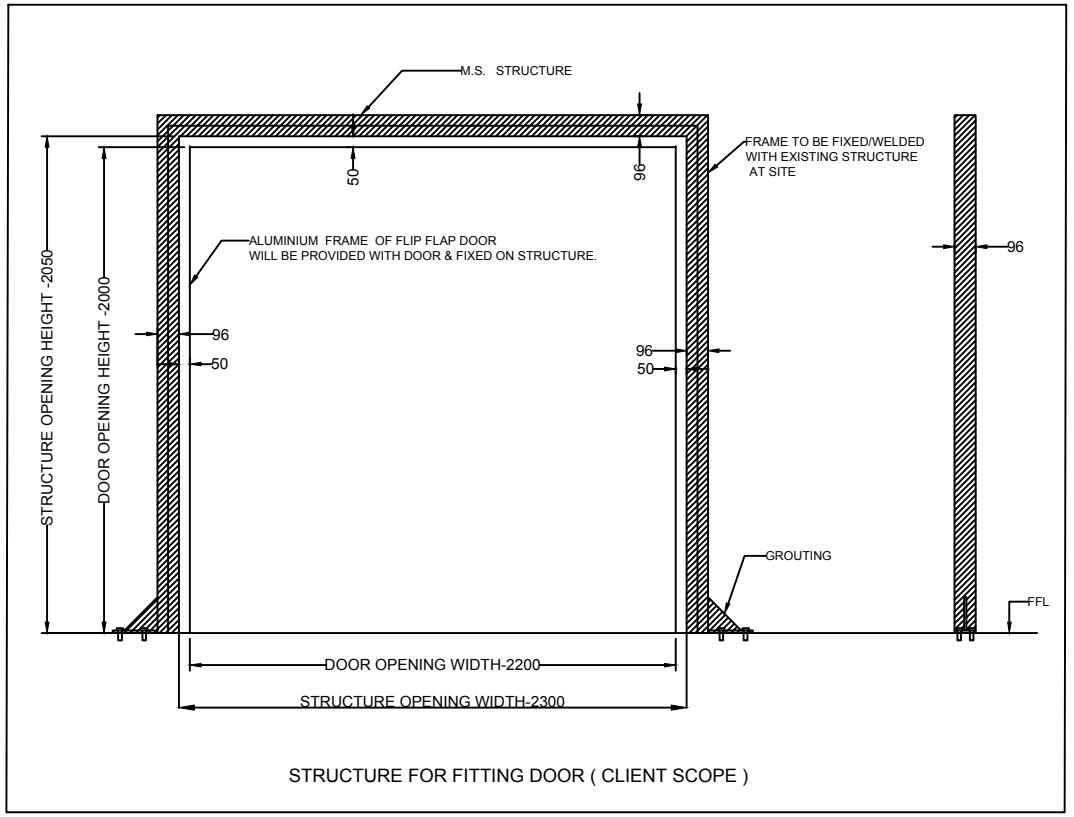

STRUCTURE FOR FITTING DOOR (CLIENT SCOPE)

R01	S.M.S.	18.2.2021	STRUCTURE DETAILS ADDED
REV NO	DRAWN	DATE	REMARK

LEAF FINISH : SS 2B FINISH (MILL FINISH)
HINGES MOC : STAINLESS STEEL
VIEW WINDOW : 1 UNIT ON EACH LEAF
VIEW WINDOW HEIGHT : 440 MM
VIEW WINDOW WIDTH : 280 MM
VIEW WINDOW POSITION FROM FFL : 1500 MM

CLEAR OPENING WIDTH	CLEAR OPENING HEIGHT	QTY	LOCATION
2200 MM	2000 MM	1 NO	

NOTES -

(1) REQUIRED STRUCTURE FOR FIXING DOOR , STRUCTURE FIXING & ALL CIVIL WORK IS IN CLIENT SCOPE .

(2) DOOR WILL BE INSTALLED AFTER READINESS OF STRUCTURE AS PER DRAWING PROVIDED.

(3) REQUIRED STRUCTURE OPENING FOR FLIP FLAP DOOR 2200(W) X2000(H) IS 2300(W)X2050(H).

This drawing & design is the property of NIHVA TECHNOLOGIES. Not to be sold or copied to any other concern.

TITLE FLIP FLAP DOOR 2200X2000

NIHVA TECHNOLOGIES PVT. LTD.

NIHVA TECHNOLOGIES PVT. LTD. PUNE
Tel : 020 66304033
Email:- info@nihva.com
Website:- www.nihva.com

	NAME	SIGN	DATE
DRAWN	S.M.S.		15.2.2021
CHECK	S.M.S.		15.2.2021
APPRD.			

CLIENT - TRANS ENGINEERS INDIA PVT LTD

PROJECT - MARS INTERNATIONAL INDIA PVT LTD

SITE LOCATION - PUNE

If any queries contact : projectsupport@nihva.com

DWG. NO. : NIHVA/20-21/0160/RO1 REV- R01

ALL DIMENSION ARE IN mm

SCALE: NTS WT: SHEET: