


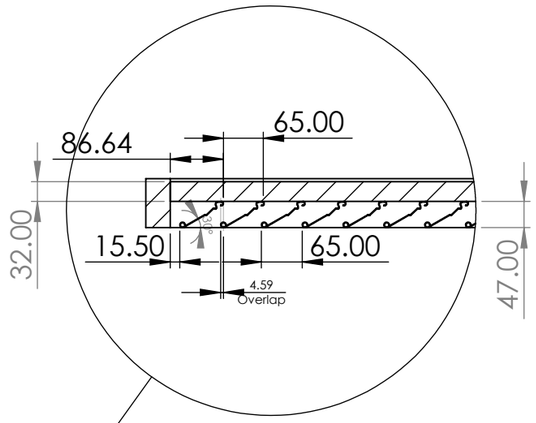


DETAIL G
SCALE 1 : 10

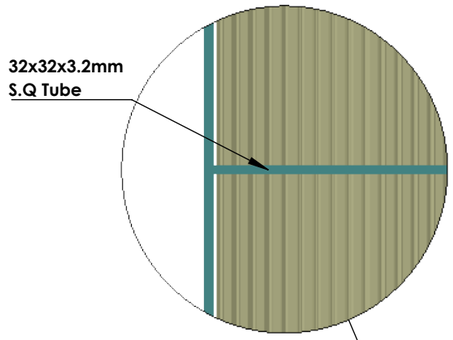


DETAIL H
SCALE 1 : 25

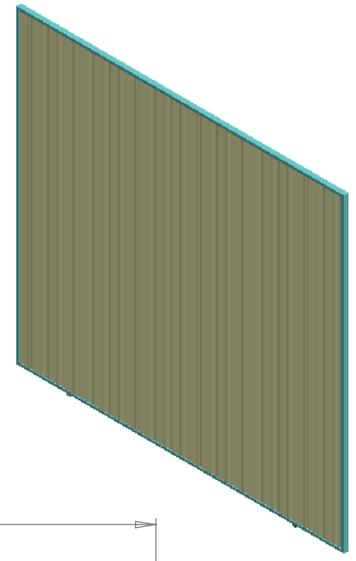

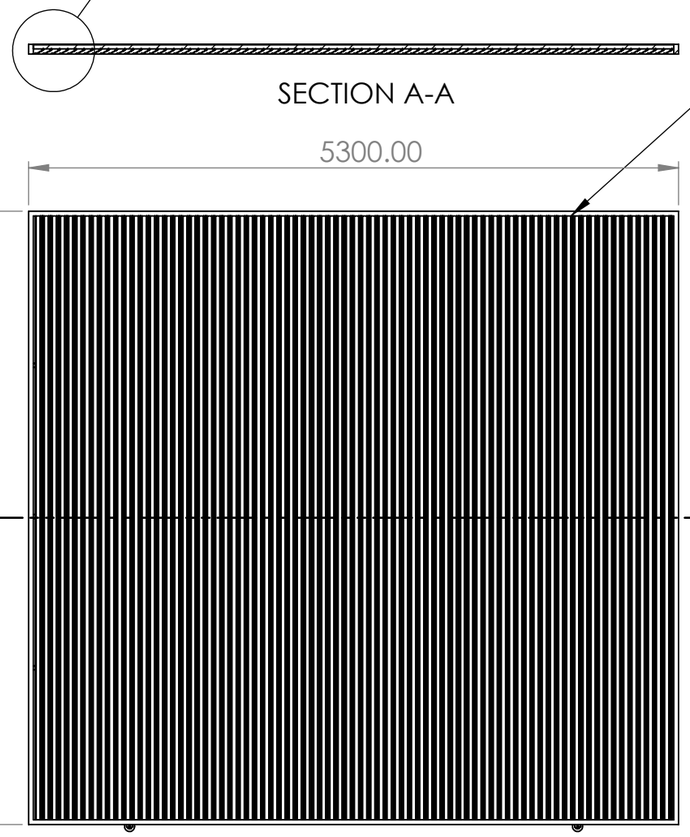

SECTION A-A

80X40X2.6mm
(Outer Tube)

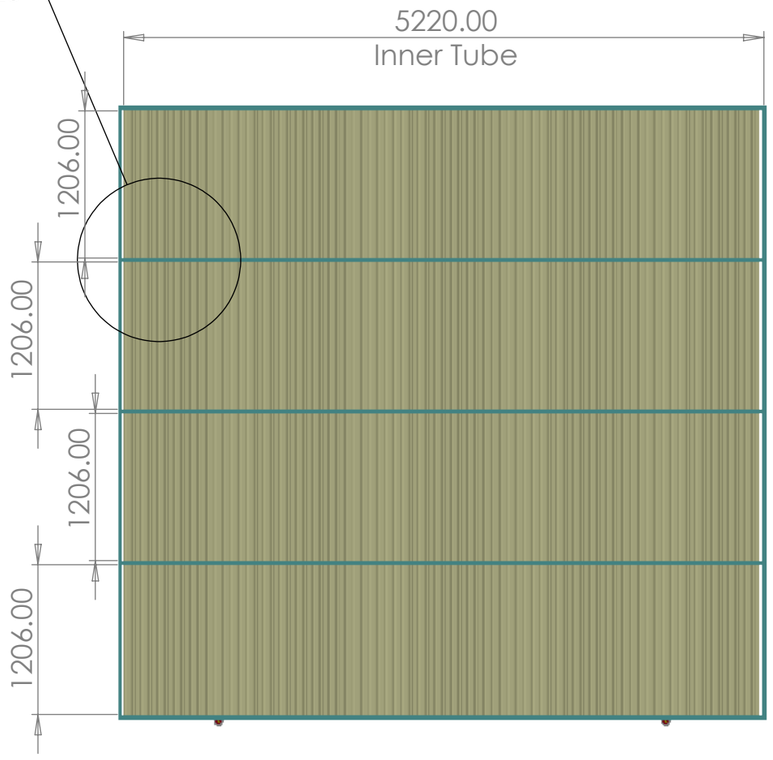

TITLE - SLIDING LEAF				NIHVA TECHNOLOGIES PVT.LTD.PUNE Website - www.nihva.com
	NAME	SIGNATURE	DATE	CLIENT - **PANCHSHIL PRIVILEGE.**
DRAWN	**S.J**		**28.02.2024**	PRODUCT - **Manual Sliding Gate For DG Substation**
CHK'D	**A.K**		**28.02.2024**	SITE LOCATION - **Kharadi, Pune**
APPV'D	**V.T**		**28.02.2024**	QTY - 14
if any queries contact - supportautomation@nihva.com				DWG NO - NIHVA/22-23/00XX / REVISION -
ALL DIMENSION ARE IN mm			A3	SCALE - / SHEET 1 OF 1