
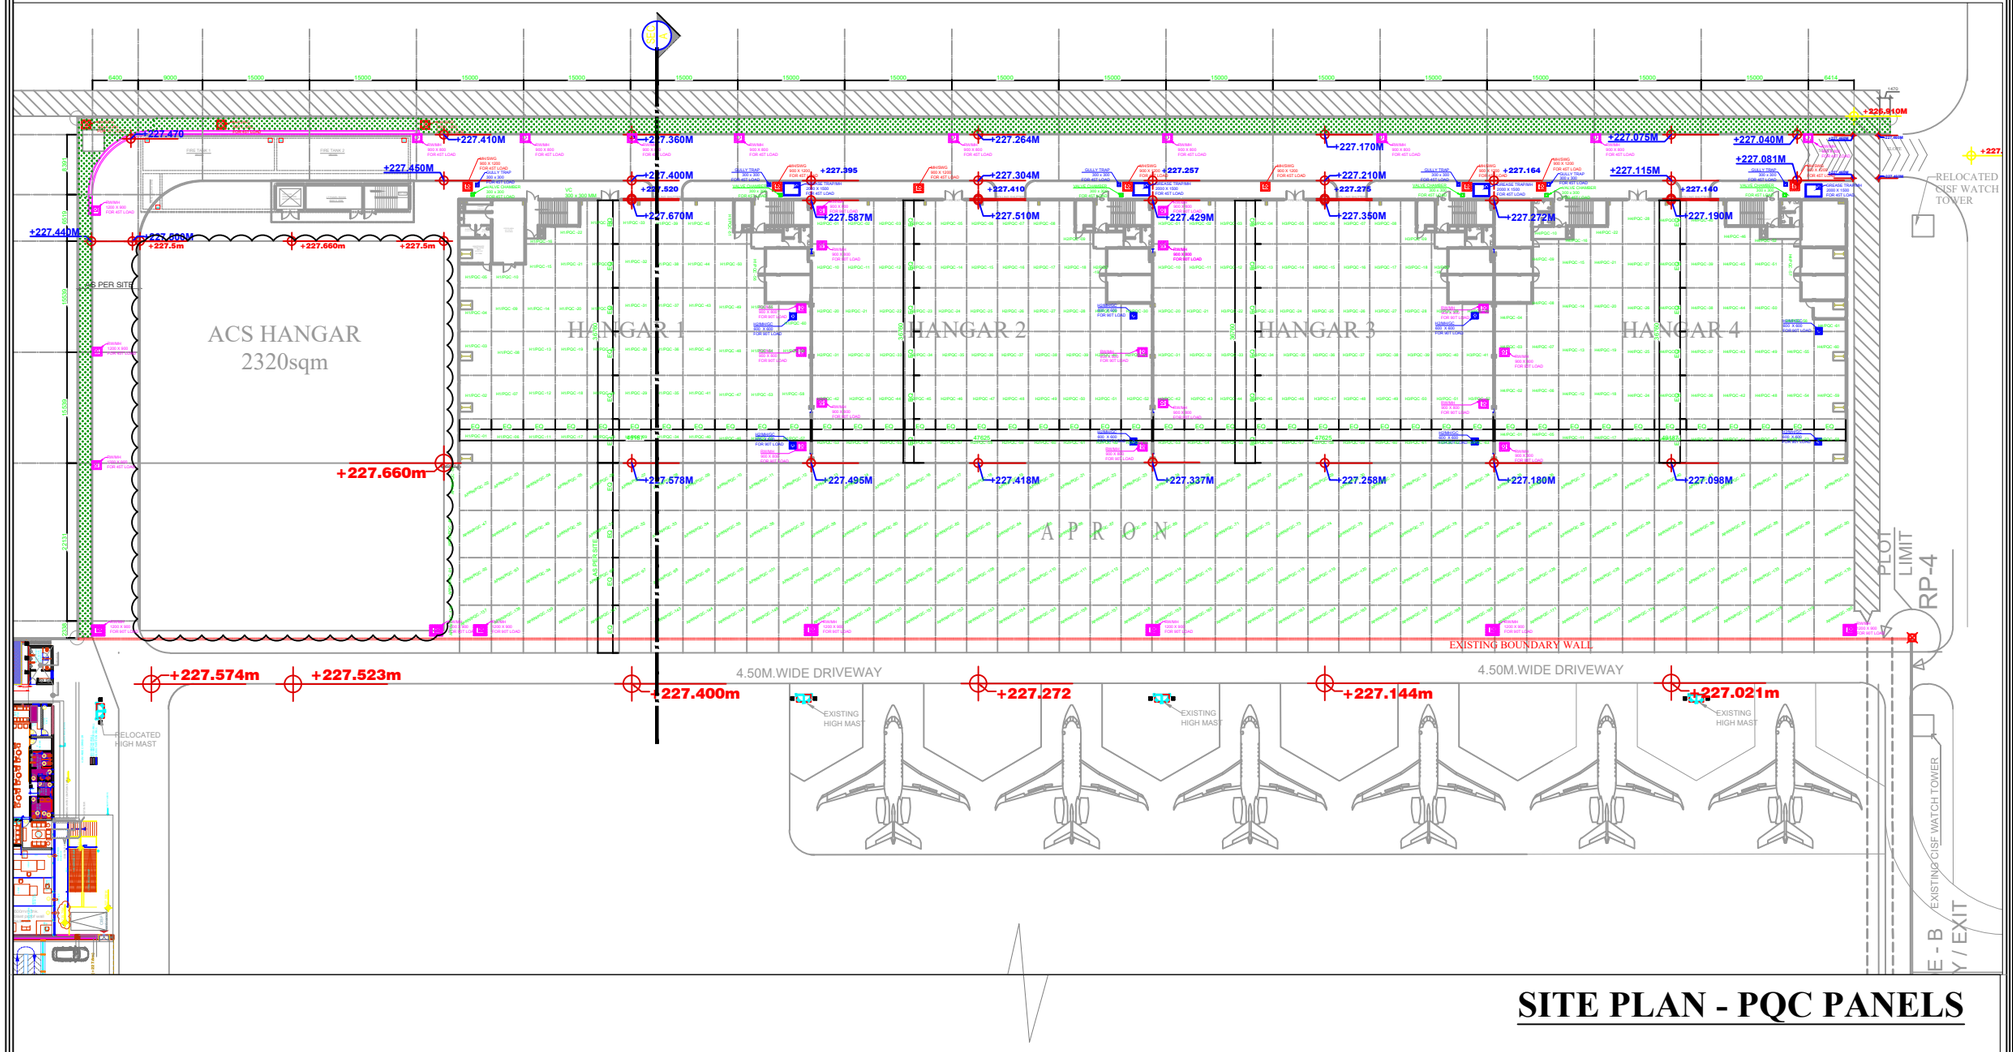


SITE PLAN - PQC PANELS

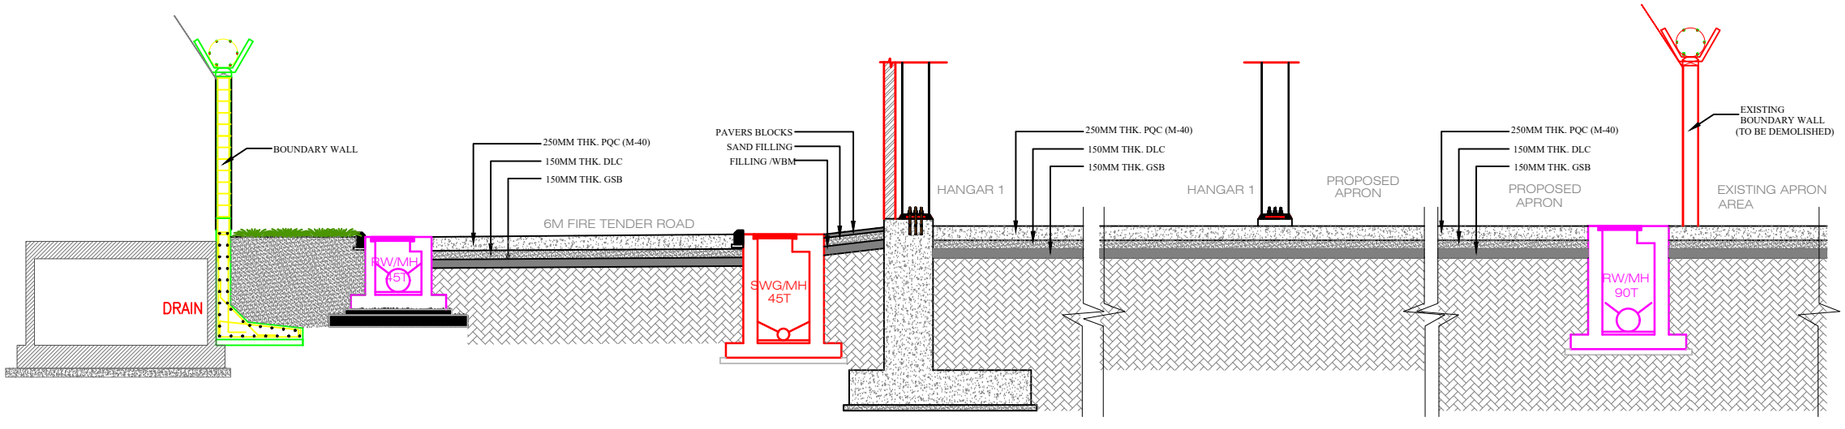


SECTION A-A


GENERAL NOTES

1. Do not scale the drawing.
2. All Drawings should be read in conjunction with relevant Other Drawings.
3. Any Discrepancy or Ambiguity in drawings should be brought to the Architect's notice immediately prior to Construction at Site.
4. All Dimensions and levels are in mm unless noted otherwise.
5. All Dimensions are from unfinished to unfinished levels unless otherwise specified.
6. Any irregularities in Construction which occurs as a result of discrepancy between Architecture, Structure, MEP, other drawings, which have not been brought to the Architects notice prior to execution shall become the responsibility of the Contractor.
7. Supervision if specifically asked would be provided but responsibility regarding correct & sound Construction shall solely rest with Contractor/Builder.
8. All relevant samples to be approved by architect prior to procurement.

SPECIAL NOTES

1. This design is based on the Data / Information provided by the Client regarding the work already executed at Site.
2. This design is based on an assumption that the design / calculation of already constructed part is as per the Codes and Best practices.
3. M/s AT Technolegal Combine Pvt. Ltd. holds no responsibility regarding the design and quality of work already executed at Site.

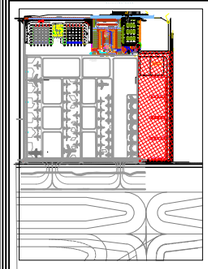

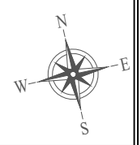

KEY PLAN :

PROJECT TITLE

CONSTRUCTION OF GA COVERED PARKING FOR AIRCRAFTS AND ANCILLARY WORKS AT GENERAL AVIATION TERMINAL, NEW DELHI

CLIENT

DELHI INTERNATIONAL AIRPORT LIMITED (GMR)

ARCHITECTS

A.T. TECHNOLEGAL COMBINE PRIVATE LIMITED
BL-63, SECTOR-116, NOIDA (UP)
MOBILE: +91-9999717558, +91-8285110902
E-MAIL: ATTLCPL@GMAIL.COM

DRAWING TITLE

SITE PLAN - PQC PANELS

ATT/2022/DIAL/GACP/AW-06

GOOD FOR CONSTRUCTION

REVISION NOTES

NO	DATE	REVISION REMARKS	SIGN

DATE	05.07.2023
SCALE	NTS
DEALT BY	GARIMA
CHECKED BY	TAPAN GOYAL

COPYRIGHT

All designs & drawings are the property of **A.T. Technolegal Combine Private Limted** and cannot be used without their written approval.