

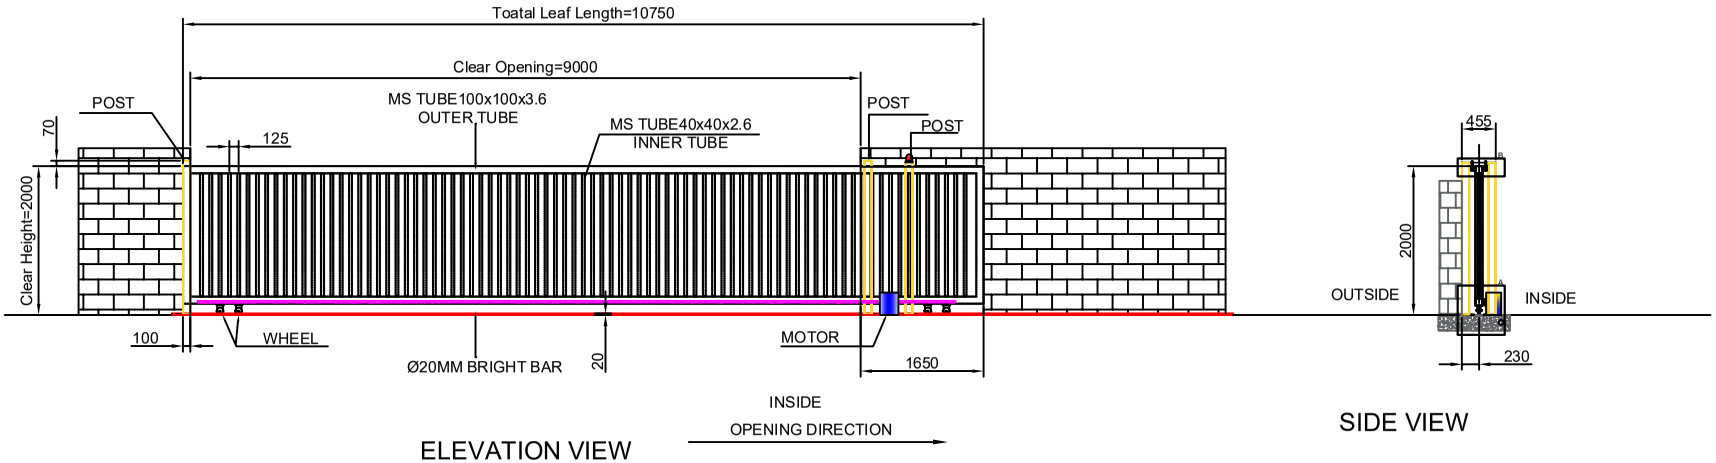


ELEVATION VIEW

SIDE VIEW

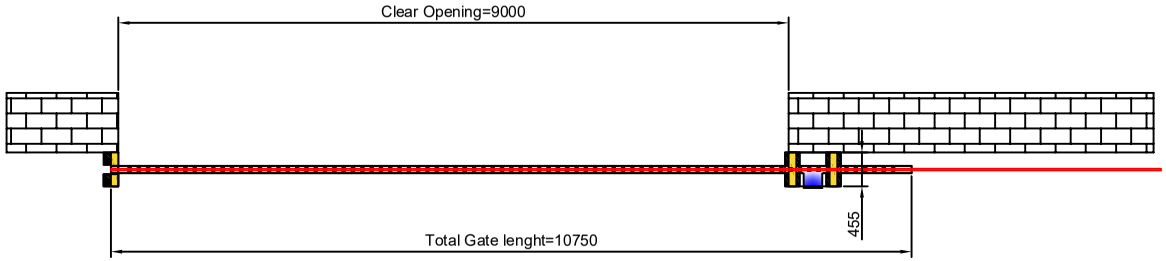

PLAN

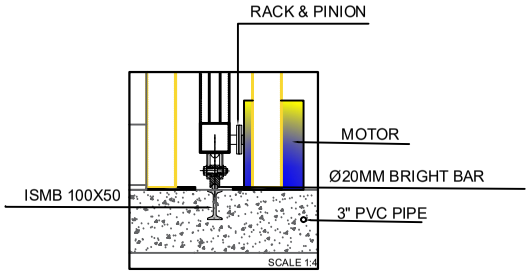


DETAIL A

Technical Specs of Motorized Sliding Gate

1. Opening length - 9000mm
2. Gate Height - 2000mm
3. Total leaf weight ≈ Approx.1134 kg
4. Parking length required - 10750+100mm
5. Outer tube size - MS SHS 100x100x3.6mm
6. Inner tube size - MS SHS 40x40x2.6mm
7. Bottom Rail - Bright bar Ø20mm
8. Post size - MS SHS 100x100x3.6mm
9. T`Safety feature - Photocell and flashing light
10. Operation - Push button from side

Note-

1. All dimension are in mm.
2. All civil work is under client scope.
3. 3" PVC pipe in the foundation to be provided by client.
4. Power supply single phase 230v, 50hz.
5. Cable for power supply 2.5 sqmm 3 core
6. Cable for photocell - 1.5 sqmm 4 core

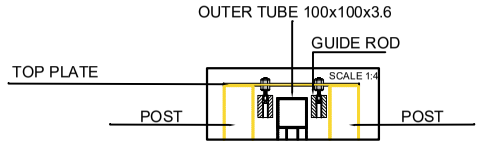

DETAIL B

This drawing & design is the property of NIHVA TECHNOLOGIES. Not to be sold or copied to any other concern.

TITLE:-MOTORISED SLIDING GATE

NIHVA TECHNOLOGIES PVT. LTD.
NIHVA TECHNOLOGIES PVT. LTD. PUNE
Tel : 020 66304033
Email:- info@nihva.com
Website:- www.nihva.com

	NAME	DATE	SIGN
DRAWN	SUJATA.B	14-10-2021	
CHECK	G.PATIL	14-10-2021	
APPRD.	A.KURHADE	14-10-2021	

If any queries contact : design@nihva.com

ALL DIMENSION ARE IN mm

CLIENT - SCON PROJECT

LOCATION -


PRODUCT - MOTORISED SLIDING GATE


DWG NO:-NIHVA\21-22\0250 | REV- 0


SCALE: NTS | SCALE:-- 1:1 | SHEET: 01 OF 01

Rev No.	Revision	Date	Revised By

CAD PATH:-

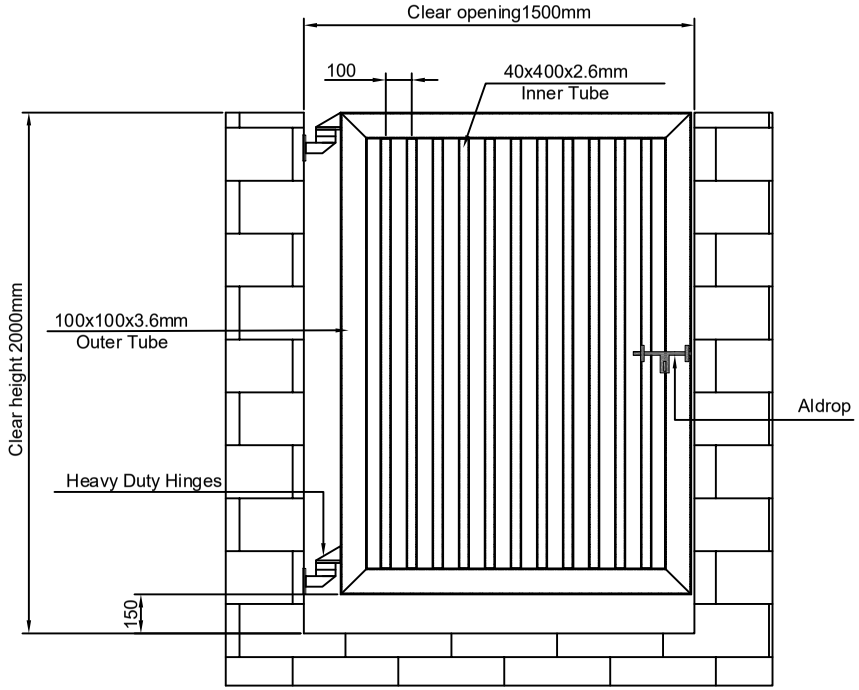

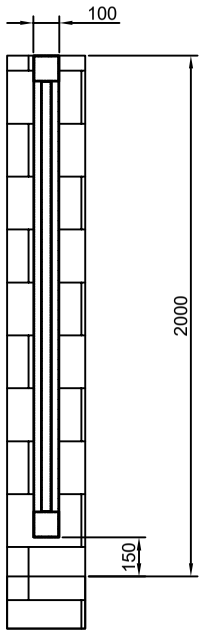

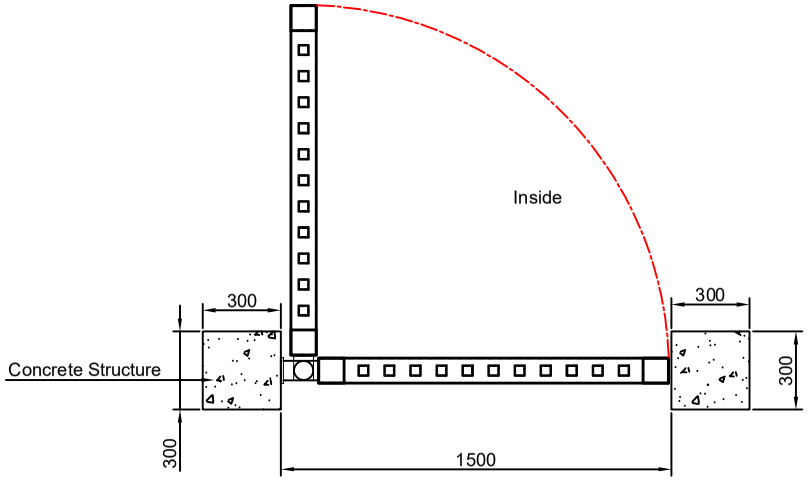

Technical Specs of Swing Gate

1. Opening Width - 1500mm
2. Gate Height - 2000mm
3. Outer tube size - MS SHS 100x100x3.6mm
4. Inner tube size - MS SHS 40x40x2.6mm
5. Total leaf weight ≈ Approx.196 kg
6. Operation - Manual

Note-

1. All dimension are in mm.
2. All civil work is under client scope.

This drawing & design is the property of NIHVA TECHNOLOGIES. Not to be sold or copied to any other concern.

TITLE:- WICKET GATE

NIHVA TECHNOLOGIES PVT. LTD.
NIHVA TECHNOLOGIES PVT. LTD. PUNE
Tel : 020 66304033
Email:- info@nihva.com
Website:- www.nihva.com

	NAME	DATE	SIGN
DRAWN	SUJATA.B	14-10-2021	
CHECK	G.PATIL	14-10-2021	
APPRD.	A.KURHADE	14-10-2021	

If any queries contact : design@nihva.com

ALL DIMENSION ARE IN mm

CLIENT -

LOCATION - SCON PROJECT

PRODUCT - WICKET GATE

DWG NO:-NIHVA\21-22\0251 | REV- 0

SCALE: NTS | SCALE:-- 1:1 | SHEET: 01 OF 01

Rev No.	Revision	Date	Revised By

CAD PATH:-