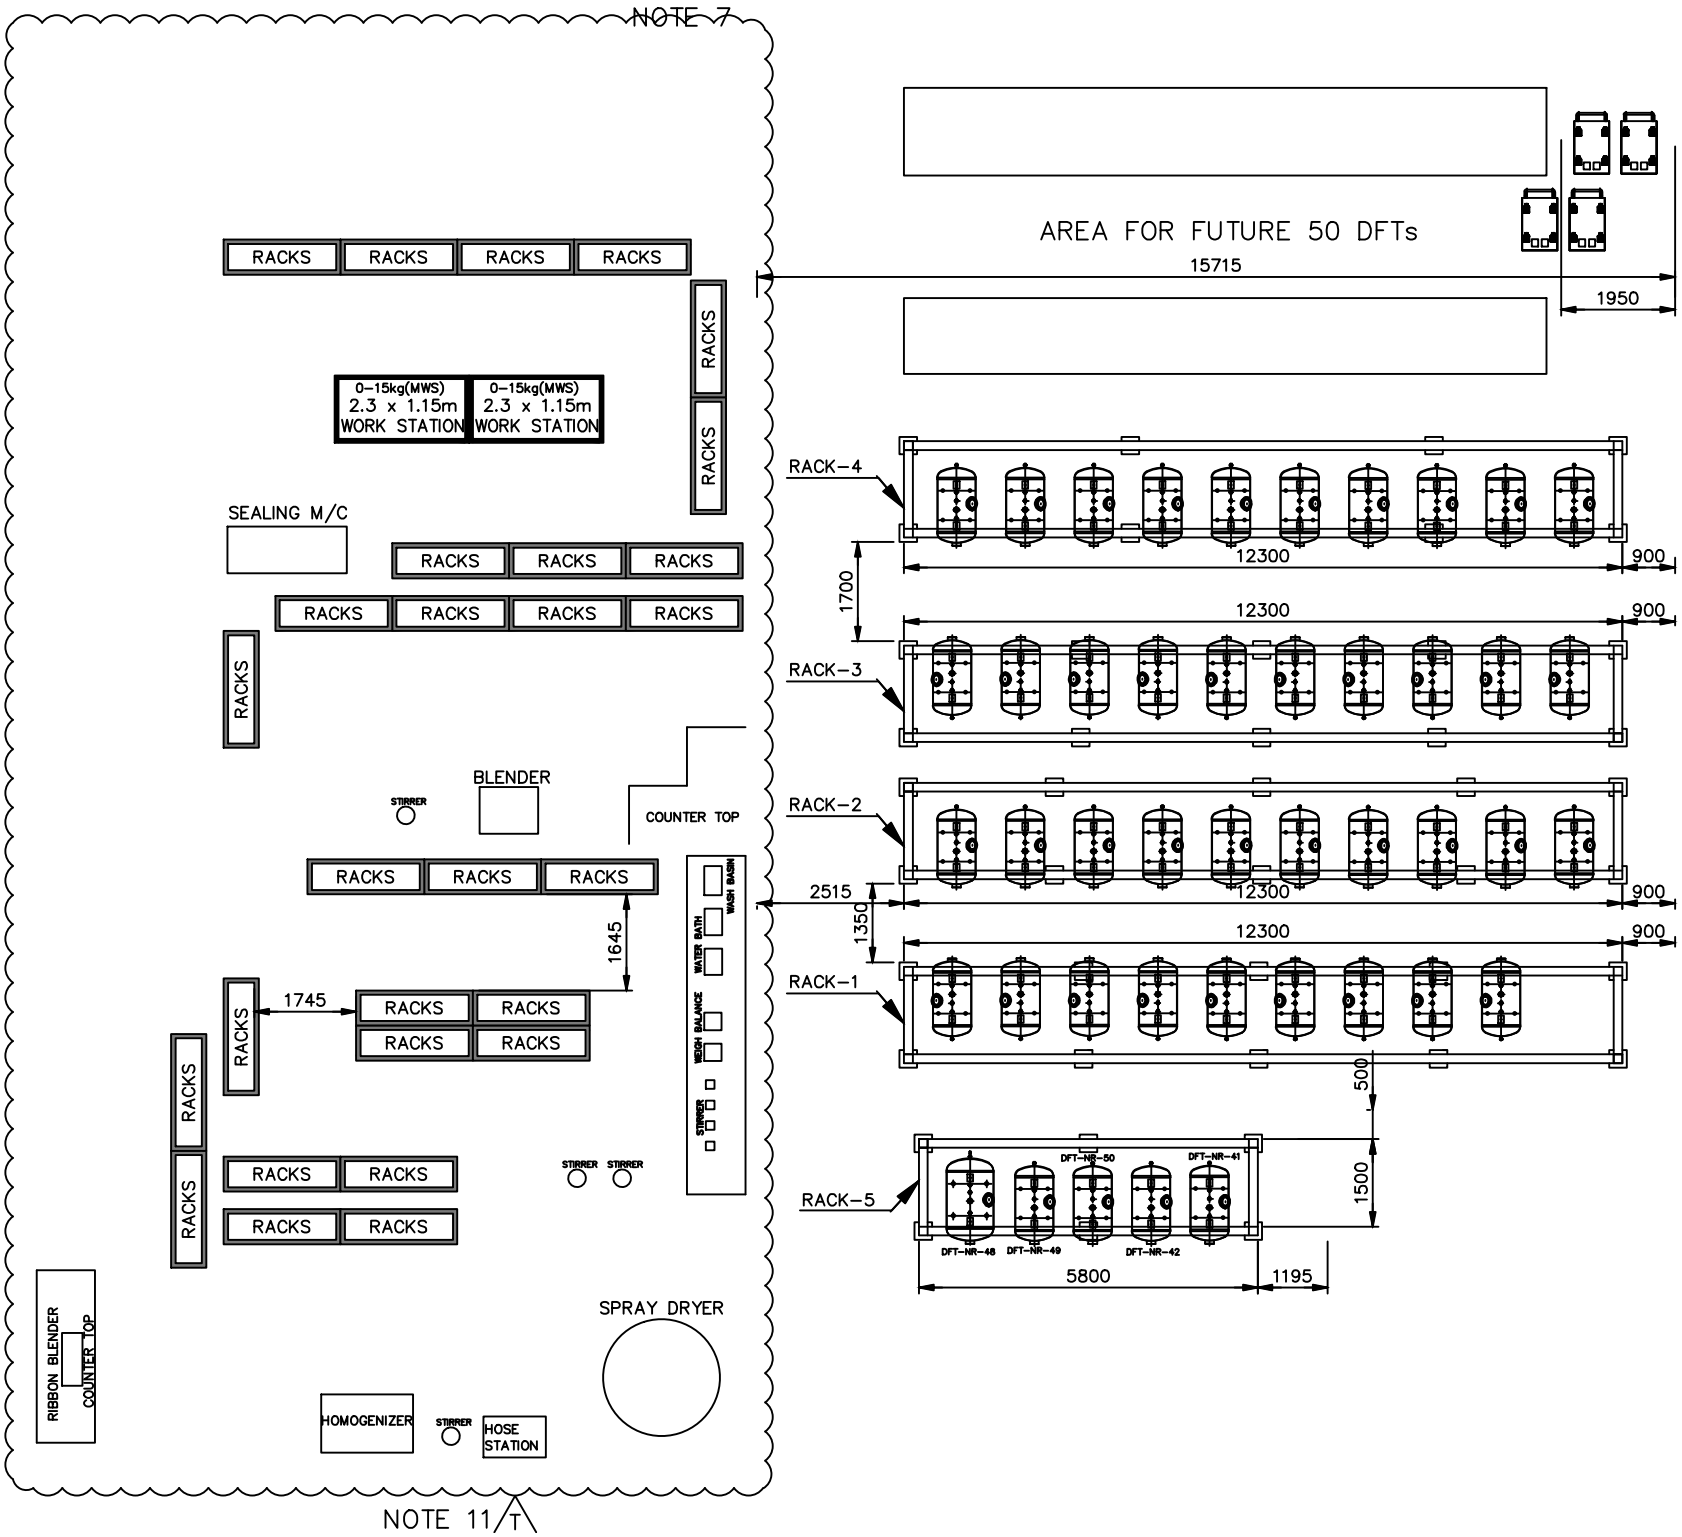

NOTE 7
AREA FOR FUTURE 50 DFTs
15715
1950
RACKS
RACKS
RACKS
RACKS
0–15kg(MWS)
2.3 x 1.15m
WORK STATION
0–15kg(MWS)
2.3 x 1.15m
WORK STATION
RACKS
RACKS
SEALING M/C
RACKS
RACKS
RACKS
RACKS
RACKS
RACKS
RACKS
BLENDER
STIRRER
COUNTER TOP
RACKS
RACKS
RACKS
1645
1745
RACKS
RACKS
RACKS
RACKS
RACKS
RACKS
RACKS
RACKS
RACKS
RACKS
STIRRER
STIRRER
WASH BASIN
WATER BATH
WEIGH BALANCE
STIRRER
RIBBON BLENDER
COUNTER TOP
HOMOGENIZER
STIRRER
HOSE STATION
SPRAY DRYER
NOTE 11
RACK–4
12300
900
1700
12300
900
RACK–3
RACK–2
2515
1350
12300
900
12300
900
RACK–1
500
1500
RACK–5
DFT–NR–50
DFT–NR–41
DFT–NR–48
DFT–NR–49
DFT–NR–42
5800
1195