



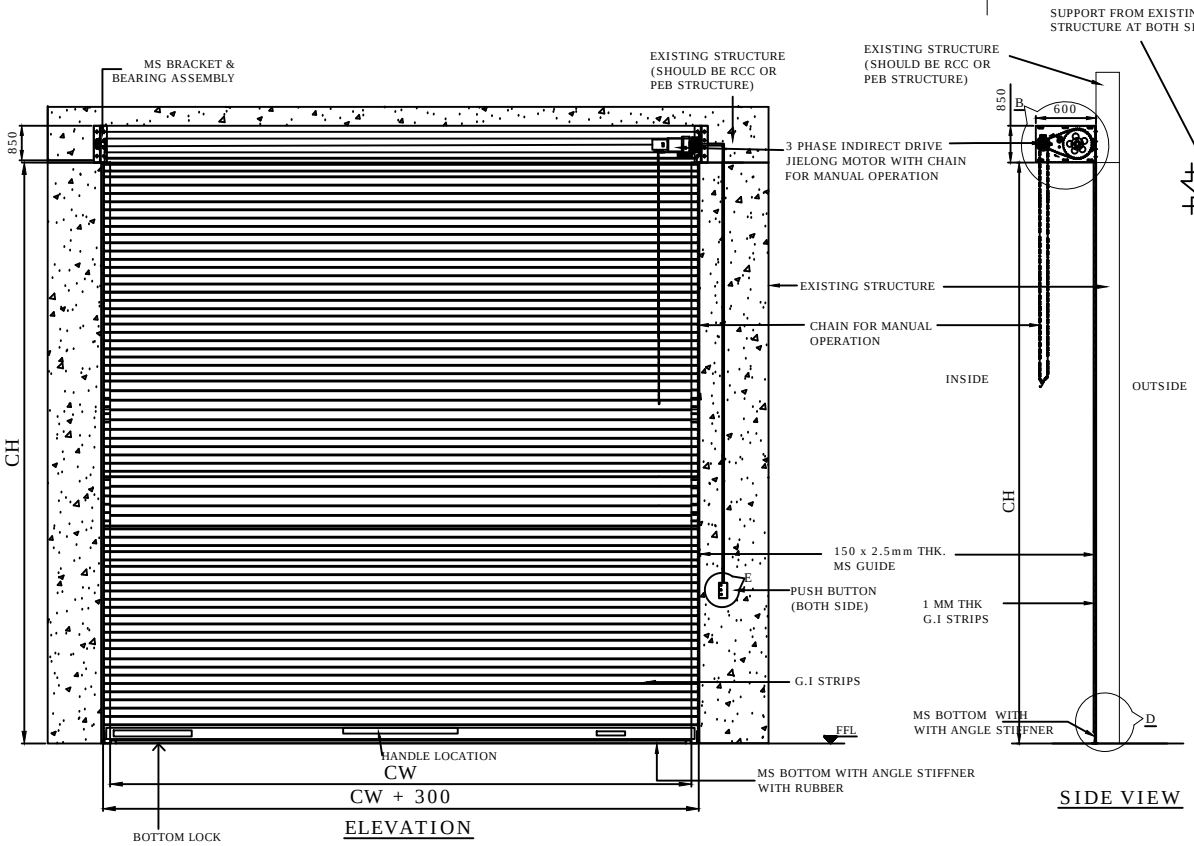


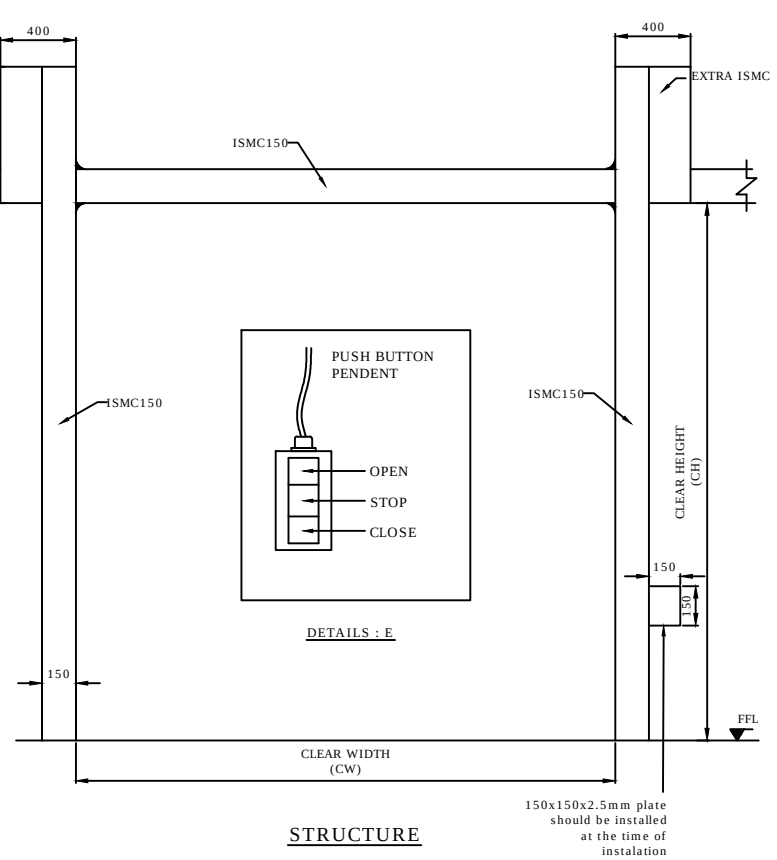


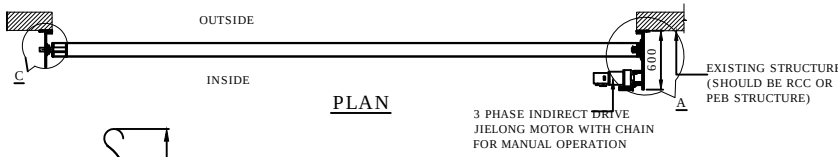

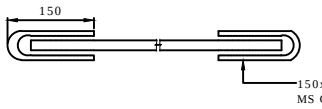


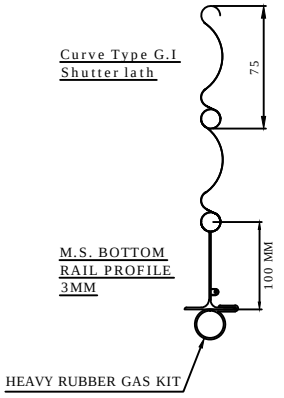

DETAILS : D

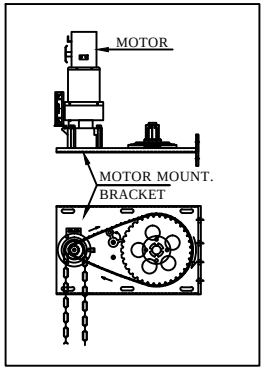

DETAILS : A & B

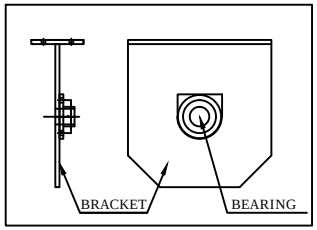

DETAILS : C

(NOTE: REQUIRED TECHANICAL STRUCTURE FOR SHUTTER IN CLIENT SCOPE)

REV NO	REV DATE	DRAWN	REMARK
R01	26.09.2019	P.V.A	1. DETAILS ADDED

CLEAR WIDTH (CW)	CLEAR HEIGHT (CH)	QUANTITY	RAL COLOR	LOCATION
4000	5000	5	PO RED	HSP
4000	5000	4	RAL - 9002	TCL - HHG

This drawing & design is the property of NIHVA TECHNOLOGIES. Not to be sold or copied to any other concern.

TITLE: MOTORIZED ROLLING SHUTTER

	NAME	SIGN	DATE
DRAWN	P.V.A		10.09.2019
CHECK	V.M.T		10.09.2019
APPRD.			

NIHVA TECHNOLOGIES PVT. LTD.
NIHVA TECHNOLOGIES PVT. LTD. PUNE
Tel : 020 66304033
Email:- info@nihva.com
Website:- www.nihva.com

CLIENT - M/S.RELIABLE CONSTROTECH ENT.

PROJECT -M/S.TATA CUMMINS PRIVATE LTD

SITE LOCATION - PHALTAN

If any queries contact : design@nihva.com

DWG. NO. : NIHVA/19-20/0087/R01 REV- R01

ALL DIMENSION ARE IN mm

SCALE: NTS WT: SHEET: