


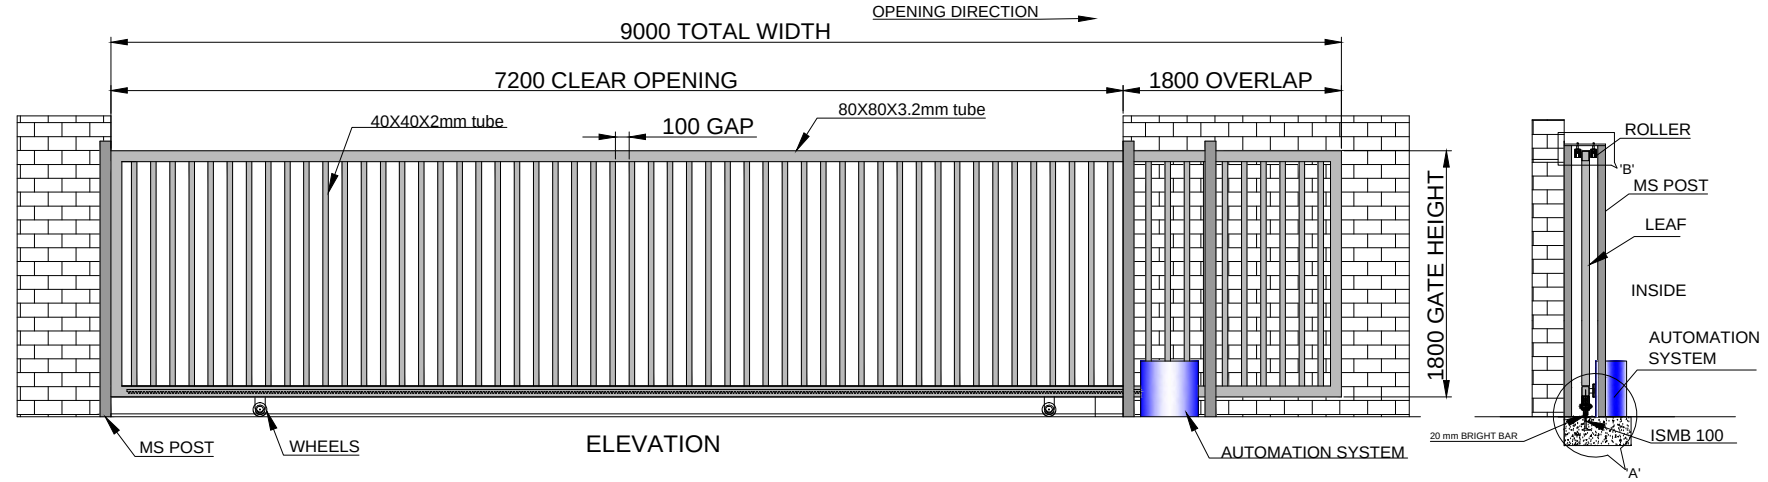


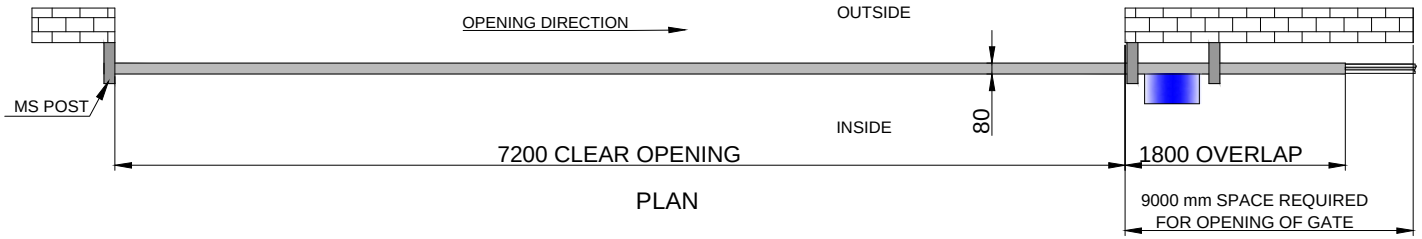

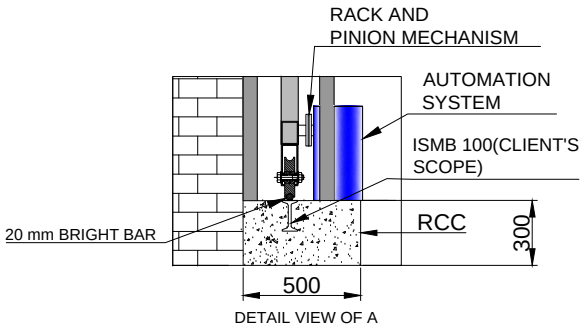

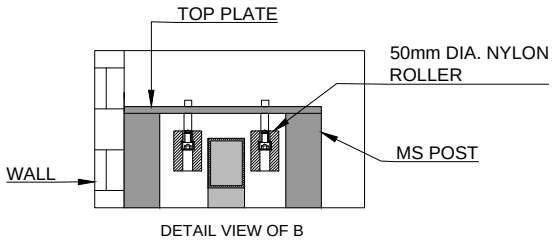

SR NO	TUBE SPECIFICATION	
1	80X80X3.2mm	OUTER FRAME
2	40X40X2mm	INNER PATTERN
3	80X80X3.2mm	FOR MS POST

TOTAL NO OF POST ARE 4.

NOTE-
1. ALL REQUIRED CIVIL WORK WILL BE IN CLIENTS SCOPE.
2. ONE COAT OF RED OXIDE & TWO COAT OF APPROVED RAL SHADE WILL BE GIVEN TO THE GATE.
3.GATE LEAF WILL BE IN TWO PARTS FOR TRANSPORTATION & WILL BE WELD TOGETHER ON SITE.

TOLERANCE- ±10mm

CLEAR WIDTH	CLEAR HEIGHT	QUANTITY	LOCATION
7200mm	1800mm	1 NOS	MAIN ENTRANCE TO COMMERCIAL & BUSINESS CENTER.

This drawing & designing is the property of NIHVA TECHNOLOGIES. Not to be sold or copied to any other concern.

TITLE
AUTOMATIC SINGLE LEAF SLIDING GATE

NIHVA TECHNOLOGIES PVT. LTD.

NIHVA TECHNOLOGIES PVT. LTD. PUNE
Tel : 020 66304033
Email:- info@nihva.com
Website:- www.nihva.com

	SIGN	DATE
DRAWN	SURAJ	17/05/17
CHECK	SAGAR P.	17/05/17
REV.		
APPROVAL	S.S	17/05/17

If any queries contact : projects@nihva.com

ALL DIMENSION ARE IN mm

CLIENT -
PROJECT -
SITE LOCATION -
DWG. NO. : NIHVA/18-19/VDR/106
SCALE: NTS | WT: | SHEET: 01 OF 01