SHUTTER SIZE:-
4000X5000:-02NOS

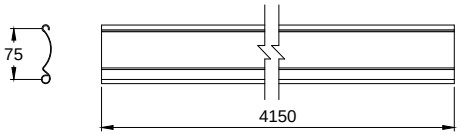

Curved slat

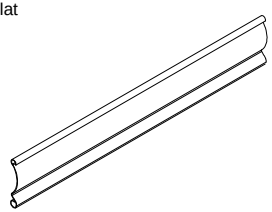

Slat profile- curved type.
Material- GI
Thickness - 1mm
Length of slats - 4150mm
Total no of slat - 320 NOS

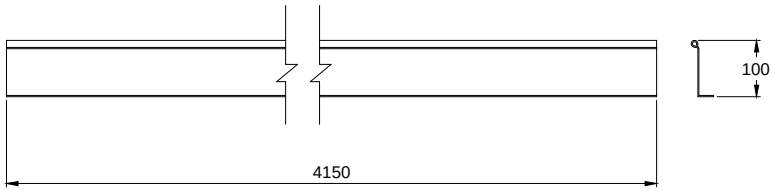

Material- MS
Thickness - 2.5mm
Length of bottom profile - 4150mm
Quantity- 04 Nos.

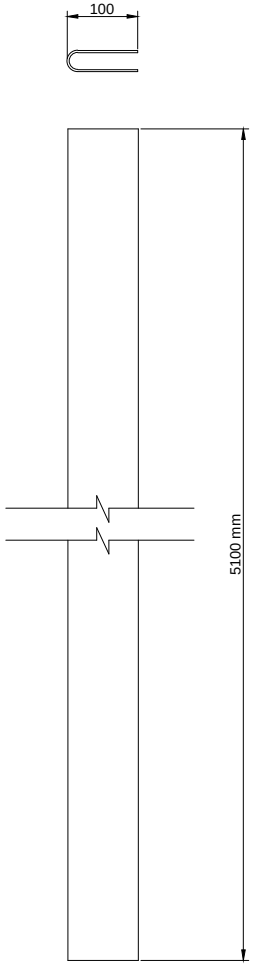

Material- MS
Thickness - 3mm
Length of guide - 5100mm
Quantity- 08 Nos.

This drawing & designing is the property of NIHVA TECHNOLOGIES. Not be sold or copy to any other concern.

TITLE				
GUIDE,BOTTOM & SLAT				
	NAME	SIGN	DATE	
DRAWN	SURAJ		11.09.2018	CLIENT -
CHECKED	P.A		11.09.2018	PROJECT -
APPROVAL	P.A		11.09.2018	SITE -
If any queries contact : design@nihva.com				DWG. NO. : NIHVA/18-19/VDR/121 / REV:- 0
ALL DIMENSION ARE IN mm				SCALE: NTS / WT: / SHEET: 01 OF 01

NIHVA TECHNOLOGIES PVT. LTD.
NIHVA TECHNOLOGY PVT. LTD. PUNE
Tel : 020 66304033
Email:- info@nihva.com
Website:- www.nihva.com