


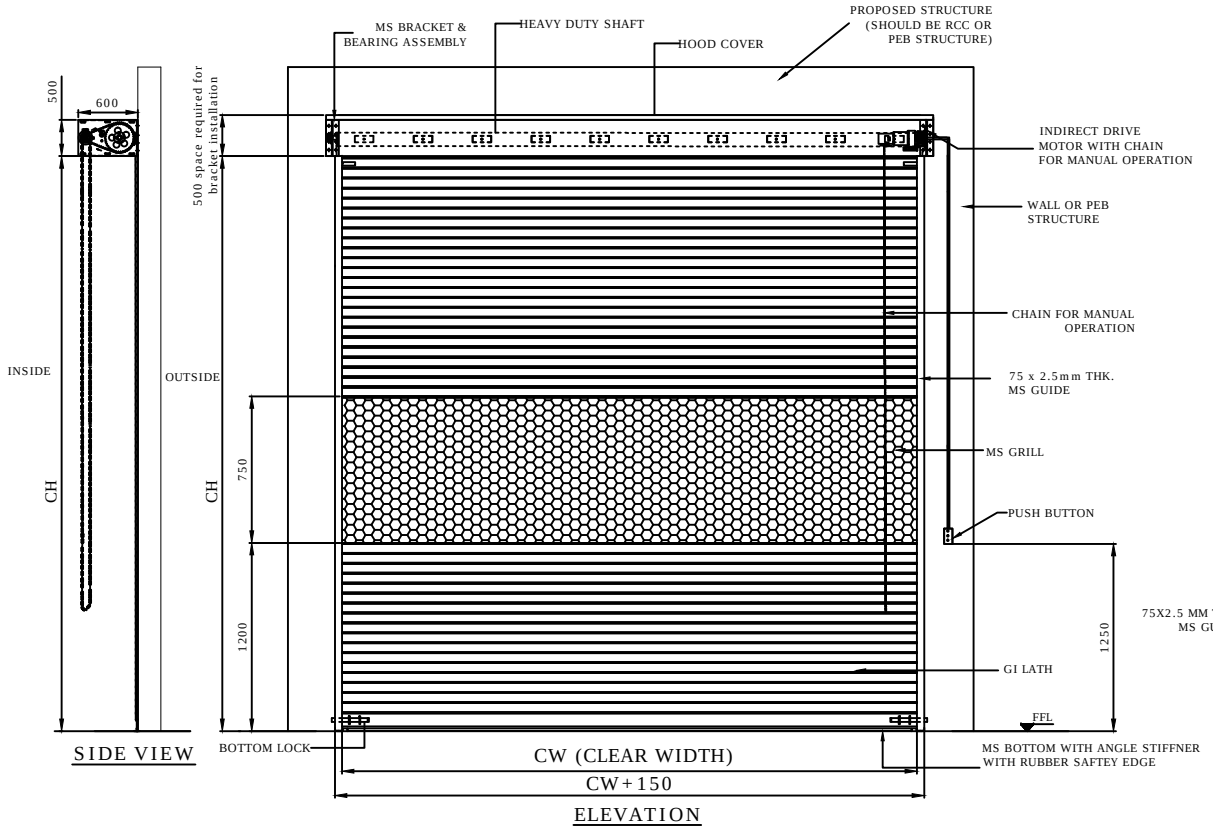


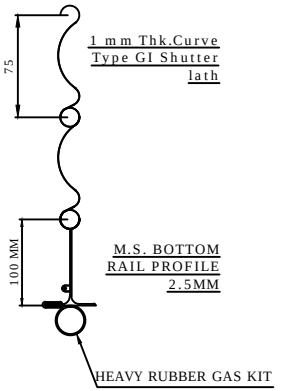

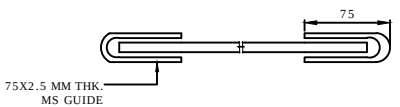

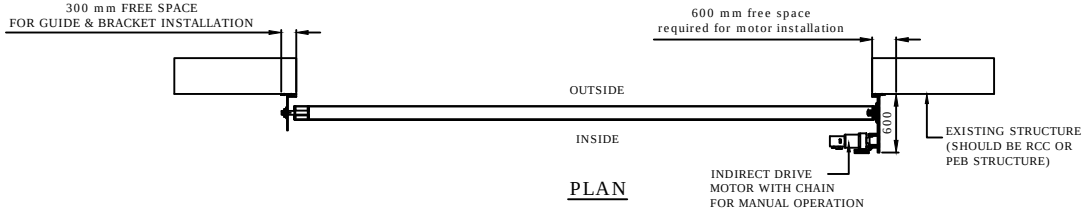

CLEAR WIDTH (CW)	CLEAR HEIGHT (CH)	QUANTITY	LOCATION
3500	3000	01 NOS	ELECTRICAL SUBSTATION FACTORY AREA
3000	3000	01 NOS	ELECTRICAL SUBSTATION FACTORY AREA
2500	3000	01 NOS	RAW WATER TANK & WTP PUMP HOUSE

DIMENSION :

CLEAR WIDTH	CLEAR HEIGHT	QUANTITY
3500	3000	01 NOS
3000	3000	01 NOS
2500	3000	01 NOS

MATERIAL:

THICKNESS :

NOTE:
1.REQUIRED STRUCTURE FOR ROLLING SHUTTER WILL BE CLIENT'S SCOPE.
2.ONE COAT OF RED OXIDE PRIMER WILL BE GIVEN TO THE SHUTTER.
3.SINGLE PHASE. 3 CORE 1.5 SQ. CABLE REQUIRE AT SITE(CLIENT'S SCOPE)
4. FOR FINAL FINISH CLIENT SHOULD CONFIRM RAL COLOR SHADE.

NIHVA TECHNOLOGIES PVT. LTD.
NIHVA TECHNOLOGIES PVT. LTD. PUNE
Email:- info@nihva.com
Website:- www.nihva.com

TITLE:

MOTORIZED ROLLING SHUTTER

CLIENT'S APPROVAL :

CLIENT - TATA PROJECT

PROJECT - ALSTOM

SITE LOCATION - MADHEPURA,BIHAR

DWG. NO. : NIHVA/17-18/0010/R01

SCALE: NTS	WT:	SHEET:1 OF 1

DRAWN BY: SURAJ	DATE: 04-05-2017
CHECK BY : SAGAR P.	DATE: 04-05-2017
APPROVED BY : R.K	DATE: 04-05-2017

If any queries contact : projects@nihva.com

NOTE: ALL DIMENSIONS ARE IN mm

THIS DRAWING & DESIGN IS THE PROPERTY OF NIHVA TECHNOLOGIES. NOT TO BE SOLD OR COPIED TO ANY OTHER CONCERN.