
ASSA ABLOY

GENERAL DRAWING RR3000IS□

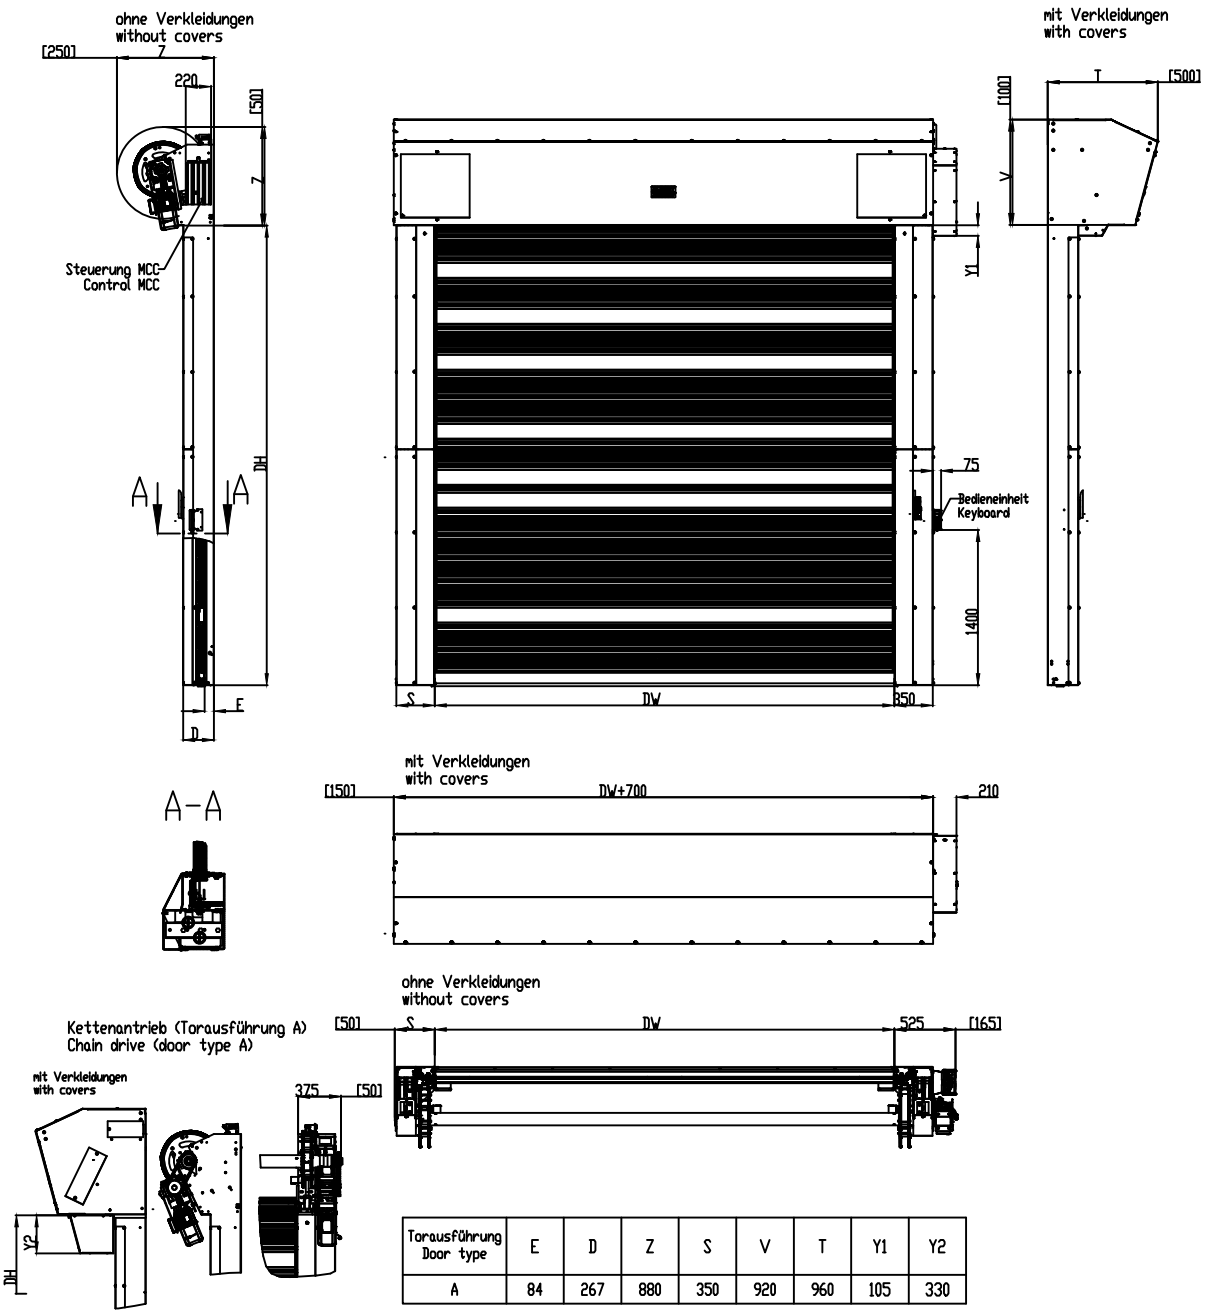

Torausführung Door type	E	D	Z	S	V	T	Y1	Y2
A	84	267	880	350	920	960	105	330

DOOR DIMENSION			
SR NO	DW	DH	QUANTITY
1	3000	3500	2

This drawing & design is the property of NIHVA TECHNOLOGIES. Not to be sold or copied to any other concern.

TITLE

HSD RR3000IS□

CLIENT APPROVAL

ALL DIMENSION ARE IN mm

	SIGN	DATE
DRAWN	OMKAR	07/11/17
CHECK	SHEKHAR	07/11/17
APPRD.	SHEKHAR	07/11/17
Ref. No.		
REV.		
MFG		

NIHVA TECHNOLOGIES PVT. LTD.

NIHVA TECHNOLOGIES
PVT. LTD. PUNE
Tel : 020 66304033
Email:- info@nihva.com
Website:- www.nihva.com

CLIENT - FERRERO INDIA PVT. LTD.

PROJECT -

SITE - BARAMATI

DWG. NO. - NIHVA/17-18/0263 | REV- 0

SCALE: NTS | WT: | SHEET: 01 OF 01

If any queries contact : projects@nihva.com