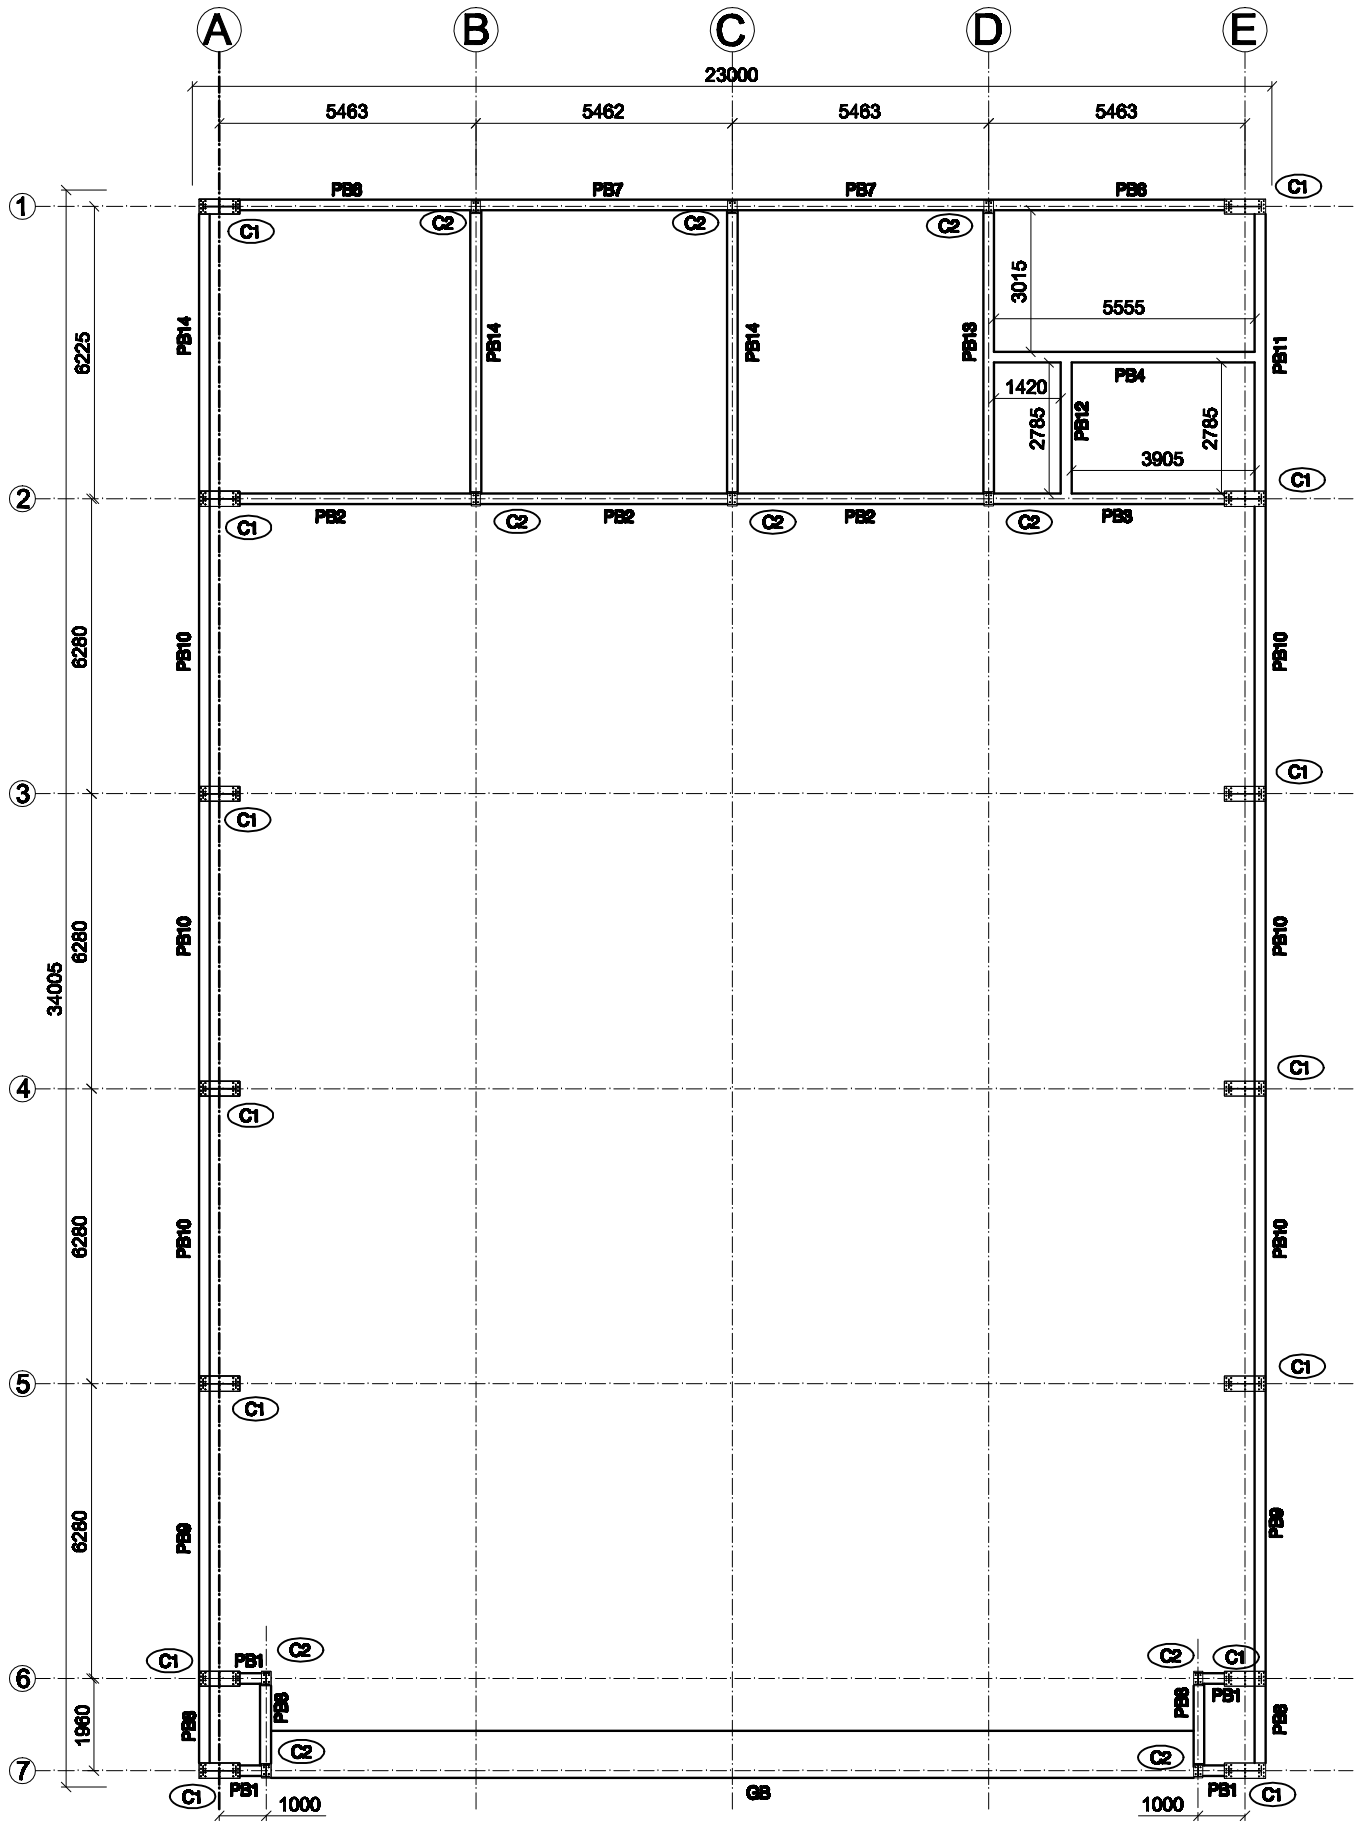


INDEX PLAN

KEY PLAN :-

LEGEND :-

- REINFORCED CONCRETE
- 230MM THK BRICK WALL
- STRUCTURAL GLAZING

N

GENERAL NOTES :

ALL DIMENSIONS ARE IN MILLIMETRES AND ARE UNFINISHED DIMENSIONS UNLESS OTHERWISE SPECIFIED.

ALL LEVELS ARE IN METRES AND ARE UNFINISHED LEVELS UNLESS OTHERWISE SPECIFIED.

DO NOT SCALE DRAWINGS, ONLY WRITTEN DIMENSIONS SHALL BE FOLLOWED, ANY DISCREPANCIES NOTED SHALL BE BROUGHT TO THE NOTICE OF THE ARCHITECT PRIOR TO EXECUTION.

SCHEDULE OF JOINERY

TYPE	DESCRIPTION	SIZE	NO.

STRUCTURAL NOTES :

S.B.C. OF SOIL CONSIDERED 25T/M2

REV.	DESCRIPTION	DATE	BY	CHD.
R0	ISSUED FOR APPROVAL	03-04-18	CMF	SSF

AMENDMENT

GRAPHIC SCALE: 0 0.5M 2M 4M / 0.5M 0 1M 3M 5M

ARCHITECT

CLIENT:

HANGER
AT PUNE

PROJECT LOCATION:

PUNE

DRAWING TITLE:

PLINTH BEAM DETAILS

SCALE : NTS	DRAWN : SRK	R2
DATE : 06.09.2018	CHKD : SRK	
PROJECT ID: 1718-AI-052-PEB		DRAWING NO: PB: 01

Astre Infra Private Limited
imagine and its done
691, Bemciel Indl. Estate,
Khanapur Rd.
Udyambag, Belgaum- 590008.
www.astreinfra.com

THESE DRAWINGS ARE UNDER COPYRIGHT AND ARE THE PROPERTY OF ASTRE INFRA PVT. LTD.. NONE OF THE DRAWINGS AND RELATED DOCUMENTS CAN BE REPRODUCED, COPIED IN WHOLE OR IN PART WITHOUT PRIOR APPROVED, WRITTEN CONSENT OF ASTRE INFRA PVT.LTD. ALL DRAWINGS AND RELATED DOCUMENTS ARE LENT ON A FIDUCIARY BASIS AND MUST BE RETURNED TO ASTRE INFRA PVT.LTD. WHICH IT HAS BEEN LOANED, AFTER FULFILLING THE PURPOSE OF ISSUE THE DRAWINGS SHALL BE RETURNED TO ASTRE INFRA PVT.LTD.