


PROPOSED PLAN LAYOUT

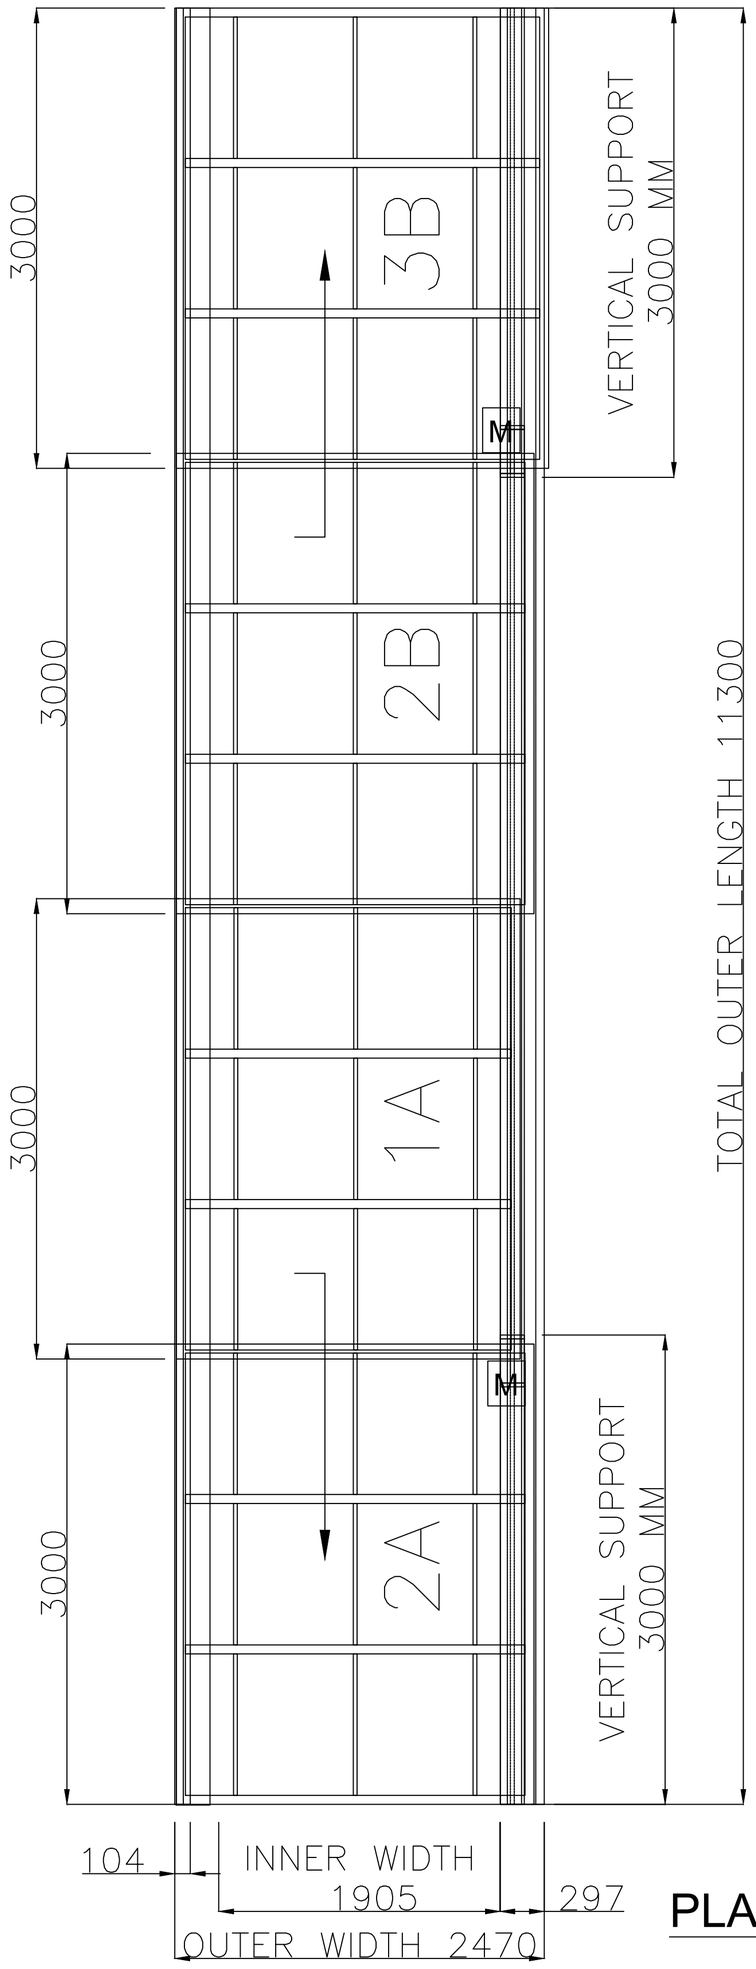

PLAN

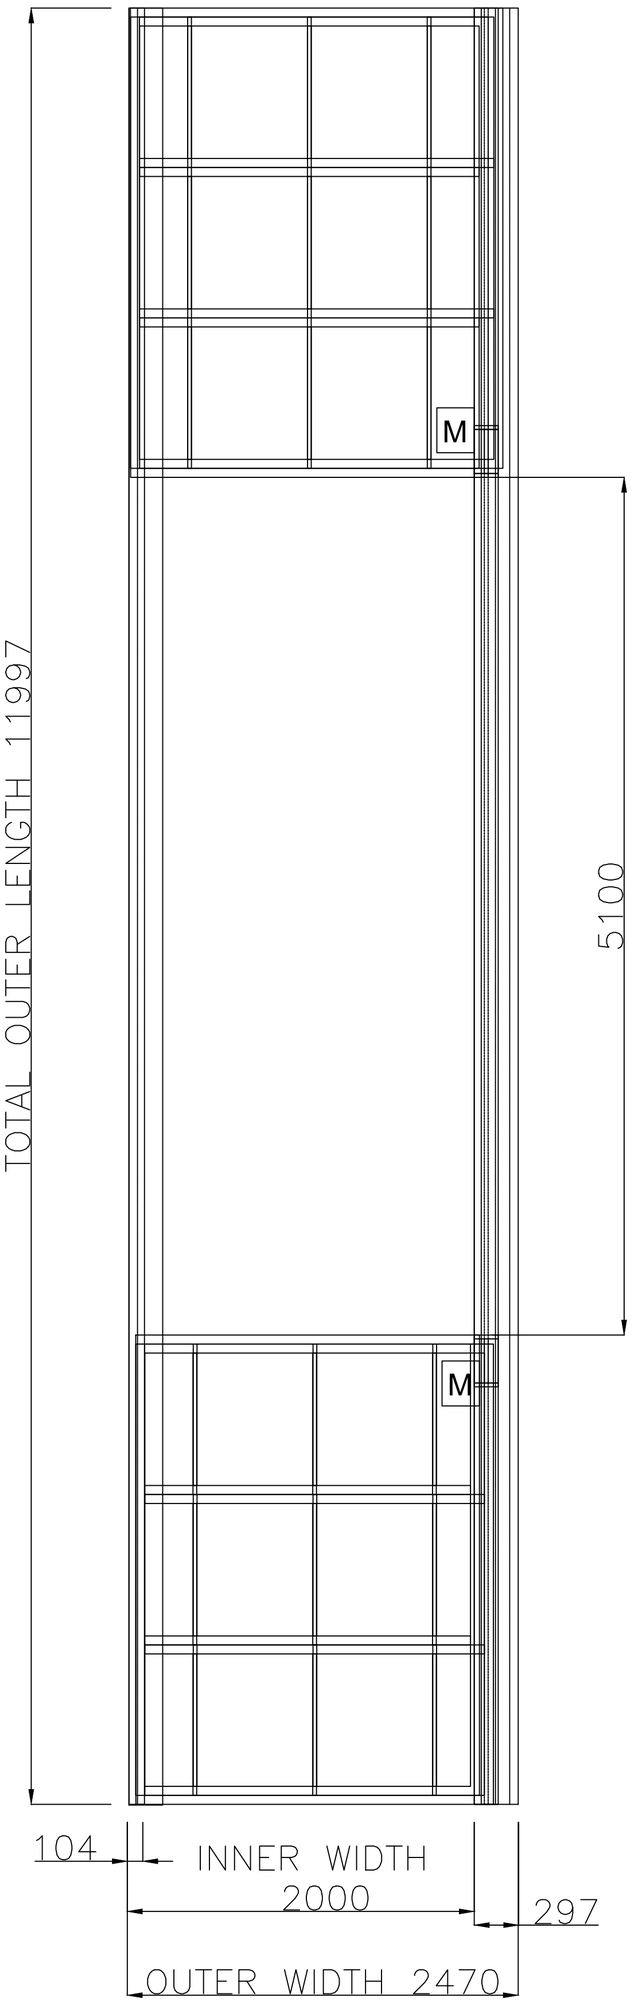

PLAN

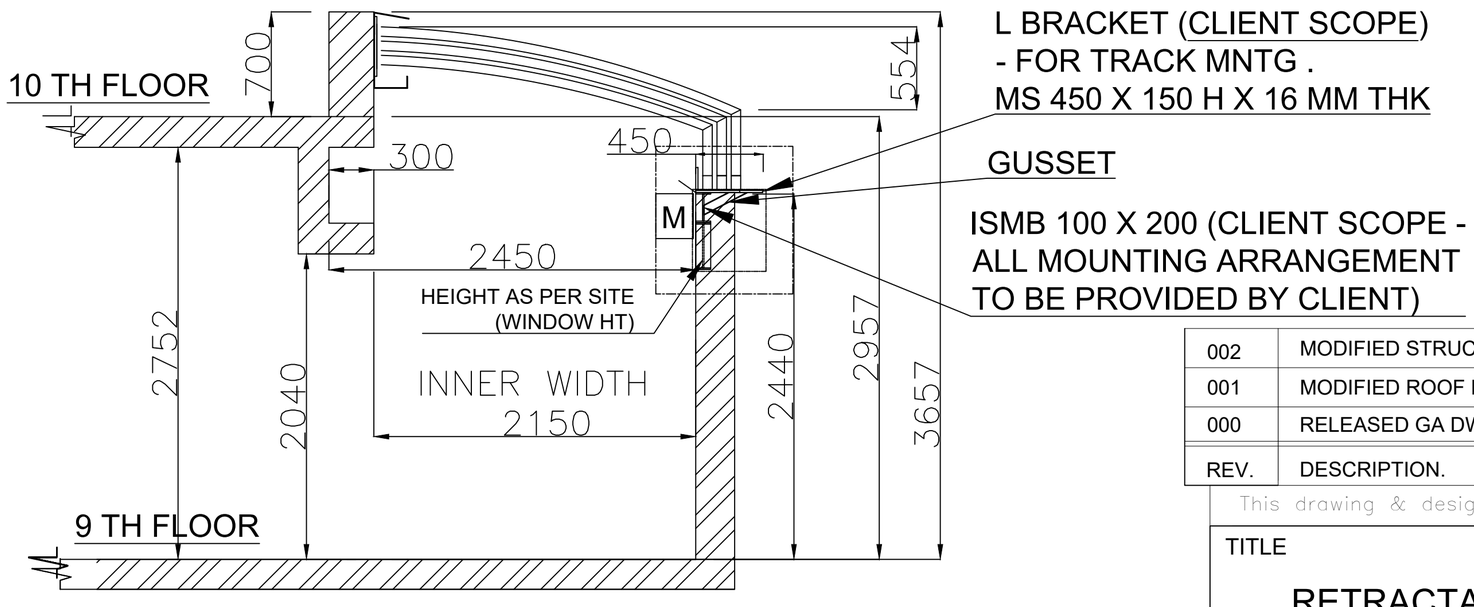

SECTION VIEW

REV.	DESCRIPTION.	REVISED BY	SIGN	DATE
002	MODIFIED STRUCTURE PER CLIENT CHANGES	MAHESH S.		08.12.22
001	MODIFIED ROOF PER SITE VISIT CHANGES & STRUCTURE	MAHESH S.		24.11.22
000	RELEASED GA DWG FOR APPROVAL	MAHESH S.		19.11.22

This drawing & design is the property of NIHVA TECHNOLOGIES. Not to be sold or copied to any other concern.

TITLE

RETRACTABLE ROOF

NIHVA TECHNOLOGIES PVT. LTD.
NIHVA TECHNOLOGIES PVT. PUNE
Tel : 020 66304033
Email:- info@nihva.com
Website:- www.nihva.com

	NAME	SIGN	DATE
DRAWN	MAHESH S.		19.11.22
CHECK	MAHESH S.		19.11.22
APPRD.	VIJAY T.		19.11.22

CLIENT - MR. SAMEER MEHTA

PROJECT - RETRACTABLE ROOF

SITE LOCATION- JAMUNA NIKETAN

If any queries contact : projectsautomation@nihva.com

NIHVA\22-23\00XX

REV- 0

ALL DIMENSION ARE IN mm

SCALE: NTS

SHEET: 01 OF 01

REV.	DESCRIPTION.	REVISED BY	SIGN	DATE
002	MODIFIED STRUCTURE PER CLIENT CHANGES	MAHESH S.		08.12.22
001	MODIFIED ROOF PER SITE VISIT CHANGES & STRUCTURE	MAHESH S.		24.11.22
000	RELEASED GA DWG FOR APPROVAL	MAHESH S.		19.11.22