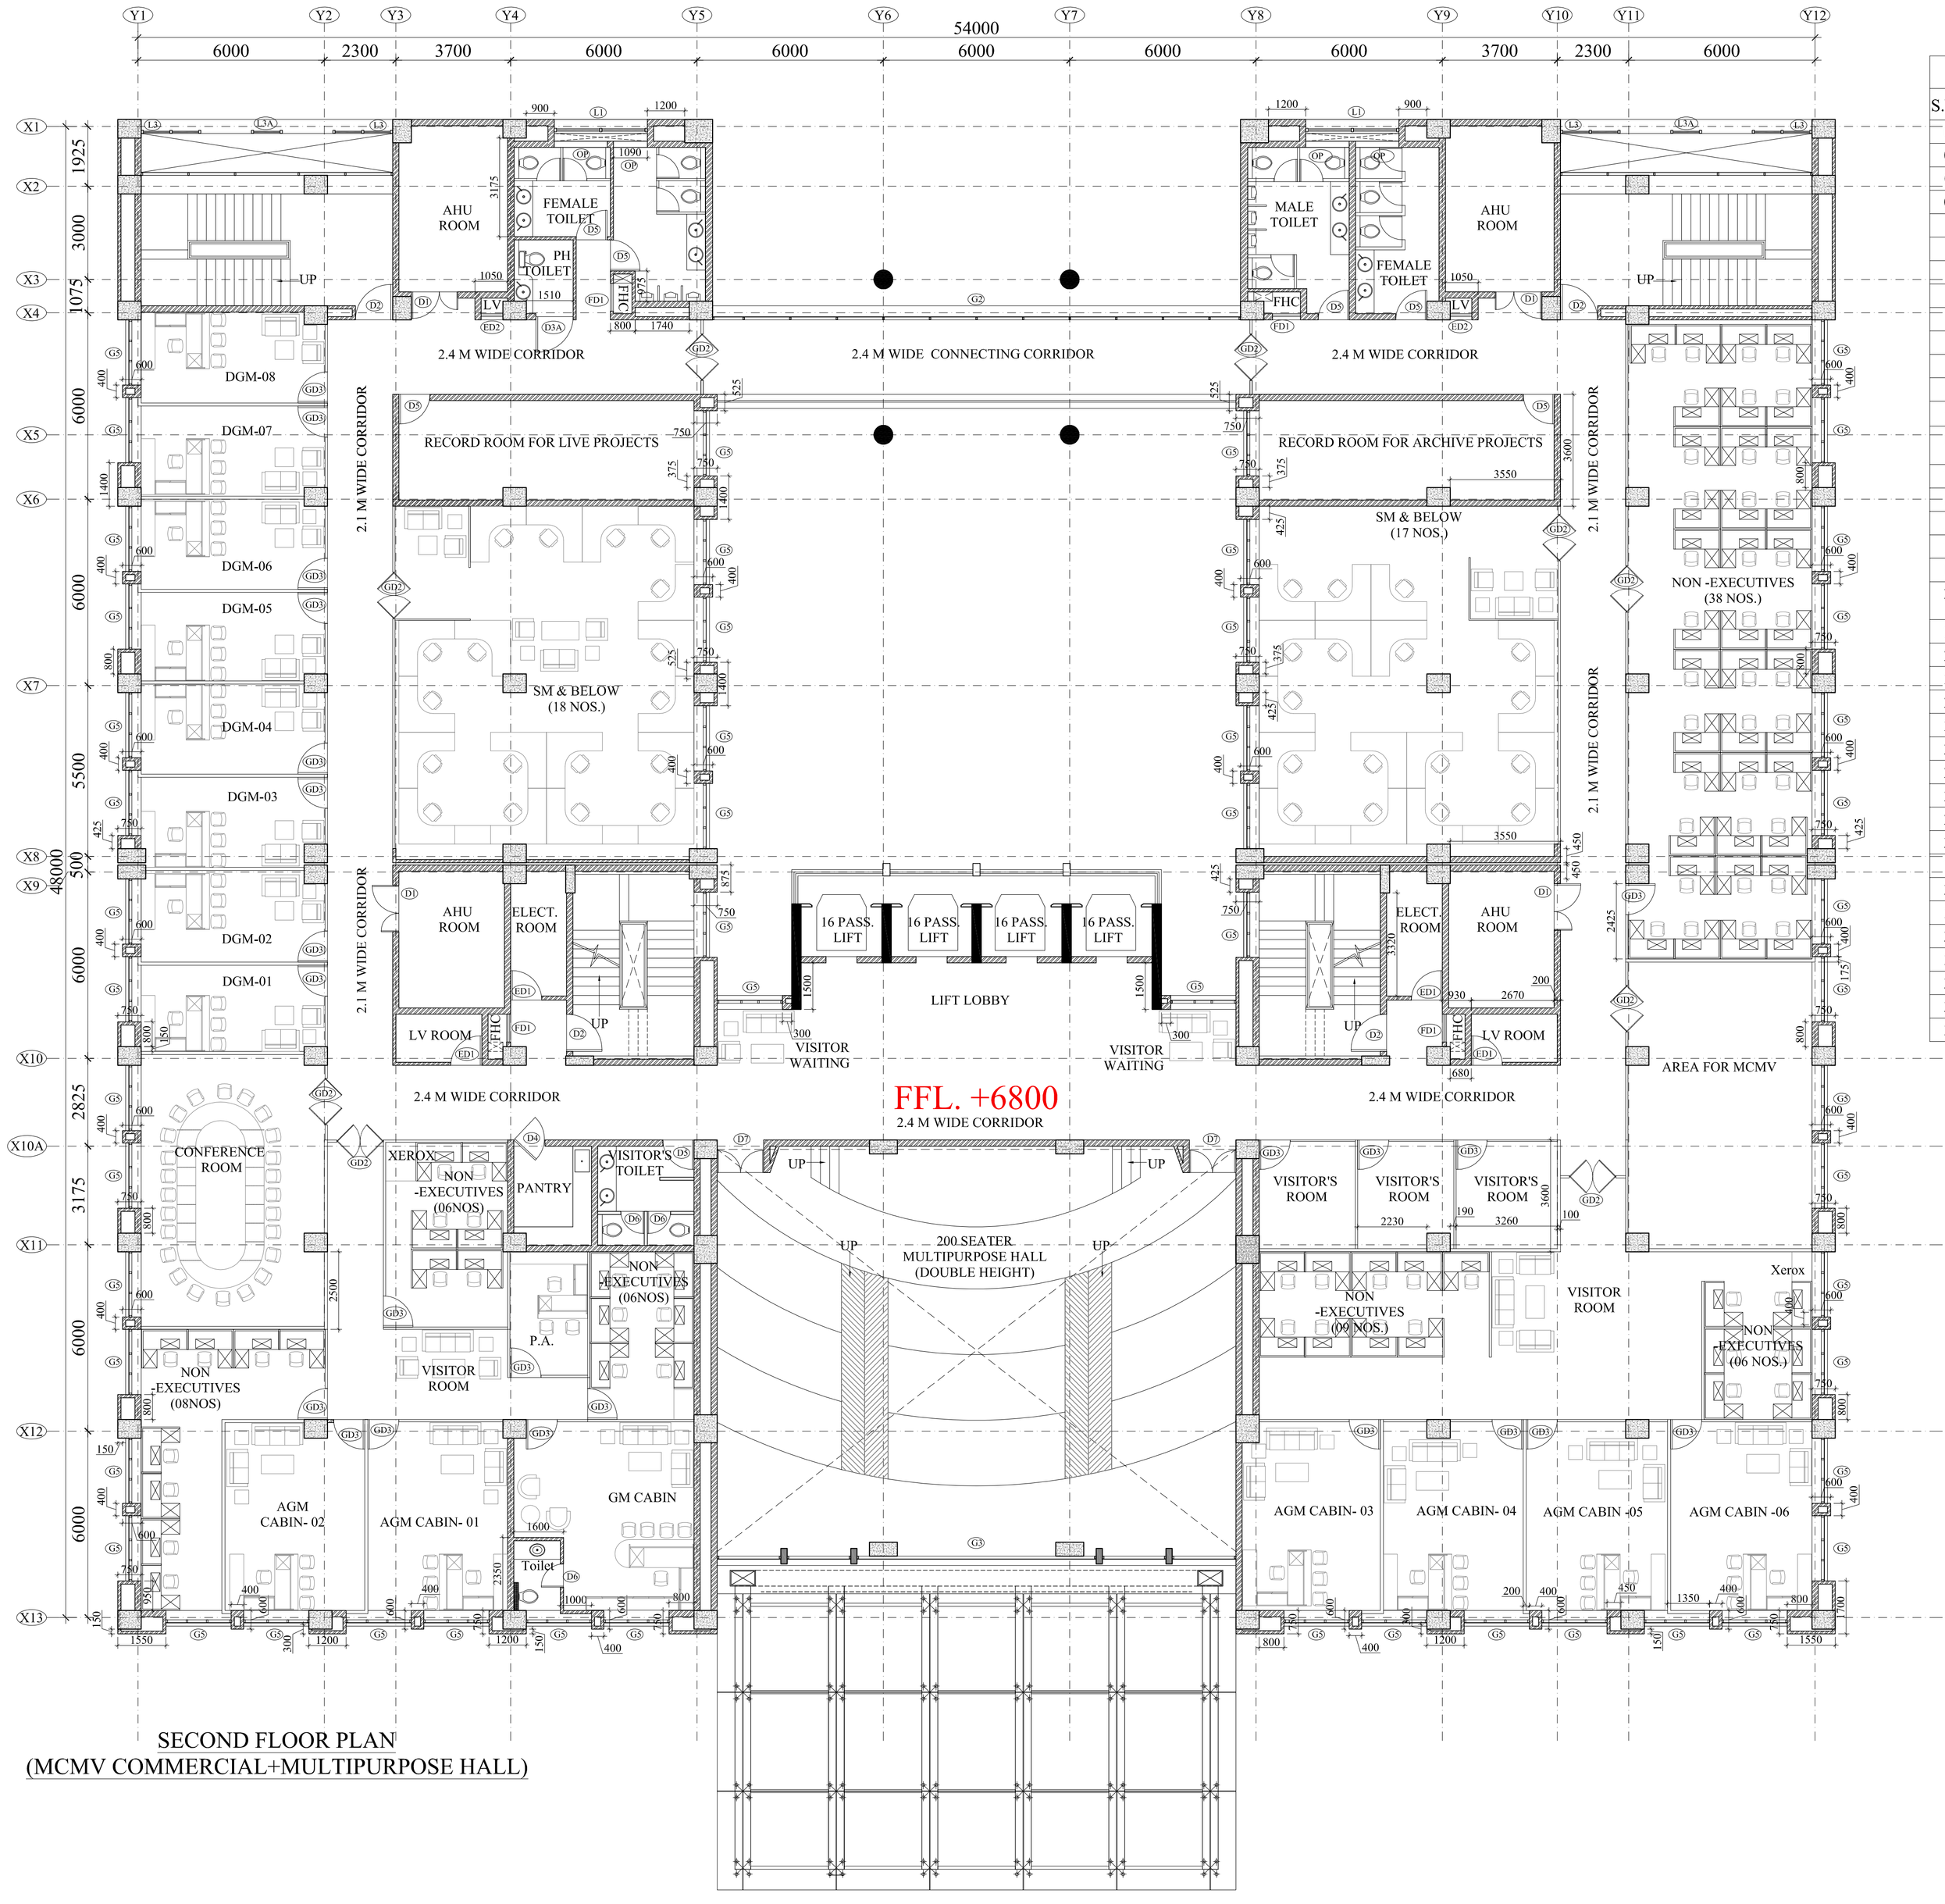


SECOND FLOOR PLAN
(MCMV COMMERCIAL+MULTIPURPOSE HALL)

DOOR-WINDOW OPENING SCHEDULE

S.NO.	TYPE	WIDTH	CILL	LINTEL	DISCRIPTION
01	D1	1500	-------	2400	A.H.U. DOOR
02	D2	1200	-------	2400	STAIRCASE DOOR
03	D3	1200	-------	2400	KITCHEN DOOR
04	D3A	1200	-------	2400	PH TOILET DOOR
05	D4	1000	-------	2400	Swing Door w/vision Panel
06	D5	1000	-------	2400	Door for Toilet,Record etc.
07	D6	750	-------	2100	Attached TOILET DOOR
08	D7	2000	-------	2400	ACOUSTICAL DOOR
09	ED1	1200	-------	2400	ELECTRICAL DOOR
10	ED2	750	100	2100	ELECTRICAL DOOR
11	ED3	2000	-------	2400	ELECTRICAL DOOR
12	FD1	900	100	2100	FHC DOOR
13	GD1	1800	-------	2400	SLIDING Glass Door
14	GD2	1500	-------	2400	Double Panel Swing Glass Door
15	GD3	1000	-------	2400	GLASS DOOR
16	GD4	1000	-------	2400	SWING GLASS DOOR
17	GD5	1200	-------	2400	GLASS DOOR
18	GD5A	1200	-------	2400	SWING GLASS DOOR
19	GD6	1150	-------	2400	SWING GLASS DOOR
20	GD7	1800	-------	2400	AUTOMATIC SLIDING DOOR
21	L1	3000	100	B.O.B.	ALUMINIUM LOUVERS
22	L2	1800	100	B.O.B.	ALUMINIUM LOUVERS
23	L3	1000	100	B.O.B.	ALUMINIUM LOUVERS
24	L3A	2000	100	B.O.B.	ALUMINIUM LOUVERS
25	L4	17000	100	B.O.B.	ALUMINIUM LOUVERS
26	G1	16700	--------	AS/ELE.	Double heightGLAZING
27	G1A	16700	--------	AS/ELE.	Double heightGLAZING
28	G2	17000	--------	AS/ELE	GLAZING
29	G2A	17000	--------	AS/ELE	GLAZING
30	G3	16700	--------	AS/ELE	Triple height GLAZING
31	G4	8100	--------	AS/ELE	GLAZING
32	G5	2100	--------	AS/ELE	GLAZING
33	G5A	2100	--------	AS/ELE	GLAZING
34	G6	1900	--------	AS/ELE	GLAZING
35	G7	4600	--------	AS/ELE	GLAZING
36	G8	2100	--------	AS/ELE	GLAZING
37	G8A	2100	--------	AS/ELE	GLAZING
38	OP	As/Plan	-------	B.O.B.	OPENING

THIS DRAWING IS THE PROPERTY OF THE DESIGN ASSOCIATES INC. AND SHALL NOT BE COPIED OR USED IN ANY MANNER WITHOUT PRIOR PERMISSION.

KEY PLAN

NOTES:

1. ALL DIMENSIONS ARE IN MM.
2. ALL DIMENSIONS ARE TO BE READ AND NOT MEASURED.
3. ALL LEVELS ARE IN METERS.
4. GRID DIMENSIONS AND PLOT LINES ARE TO BE STRICTLY ADHERED TO.
5. ALL LEVELS INCLUDING FLOOR LEVELS, CILL & LINTEL LEVELS, LANDING LEVELS, PARAPET HEIGHT/ LEVELS, LEVELS OF HORIZONTAL PROJECTION & BANDS INCLUDING ANY SURFACE FEATURES INDICATED IN THE DRAWINGS ARE TO BE STRICTLY ADHERED TO.
6. IN CASE OF ANY DISCREPANCY BETWEEN ANY DRAWING, ARCHITECT HAS TO BE INFORMED PRIOR TO ANY EXECUTION.

MARK	DATE	DESCRIPTION
R2		REVISION
R1		REVISION
GFC		GOOD FOR CONSTRUCTION
AC		ADVANCE COPY

OWNER-

GOA SHIPYARD LIMITED
(A Govt. of India Undertaking)
VASCO DA GAMA, GOA, 403802
contactus@goashipyard.com
TEL.No: - (0832) 251252-56, 2512359
FAX No: -(0091-832) 2514232, 2512148

EXECUTING AGENCY-

NBCC (INDIA) LIMITED
(Formerly National Buildings Construction Limited
(A Government of India Enterprise)
NBCC Bhawan, Lodhi Road
New Delhi - 110 003, India
Telephone No : 011 - 24367314 - 17, 24367573
Fax : 011 - 24366995

ARCHITECTS-
DESIGN ASSOCIATES INC.
ARCHITECTURE
A - 163, Sector - 136,
Noida - Greater Noida Expressway,
Noida - 201301, Phone no: 0120-2428600/30
e-mail: matinder.sharma@designassociates.in

MECHANICAL CONSULTANT-
DESIGN CENTER CONSULTING ENGINEERS, NEW DELHI

ELECTRICAL CONSULTANT-
DESIGN CENTER CONSULTING ENGINEERS, NEW DELHI

PLUMBING CONSULTANT-
DESIGN CENTER CONSULTING ENGINEERS, NEW DELHI

STRUCTURE CONSULTANT-
LKT ENGINEERING CONSULTANTS LTD.
10/49, Subhash Nagar,New Delhi-110027
Phone:+011-45565818,Tel/Fax:+011-25126129
info@lktengineering.com
http://www.lktengineering.com

PROJECT-
CONSTRUCTION OF MCMV OFFICE BUILDING AT GOA SHIPYARD, GOA


DRAWING TITLE-
SECOND FLOOR PLAN

DRAWING PURPOSE-
TENDER DRAWING

JOB NO. -	DWG. REF. NO.-	DATE-
538	----------	----------
SCALE-	REVISION-	DATE OF ISSUE-
1:110	----------	21.12.16

DWG. NO.-
538/GSL/TD/AR/154

	SHEET SIZE-	SHEET NO-
	A1	----------
	DRAWN BY-	CHECKED BY-
	RAJEEV	MATINDER

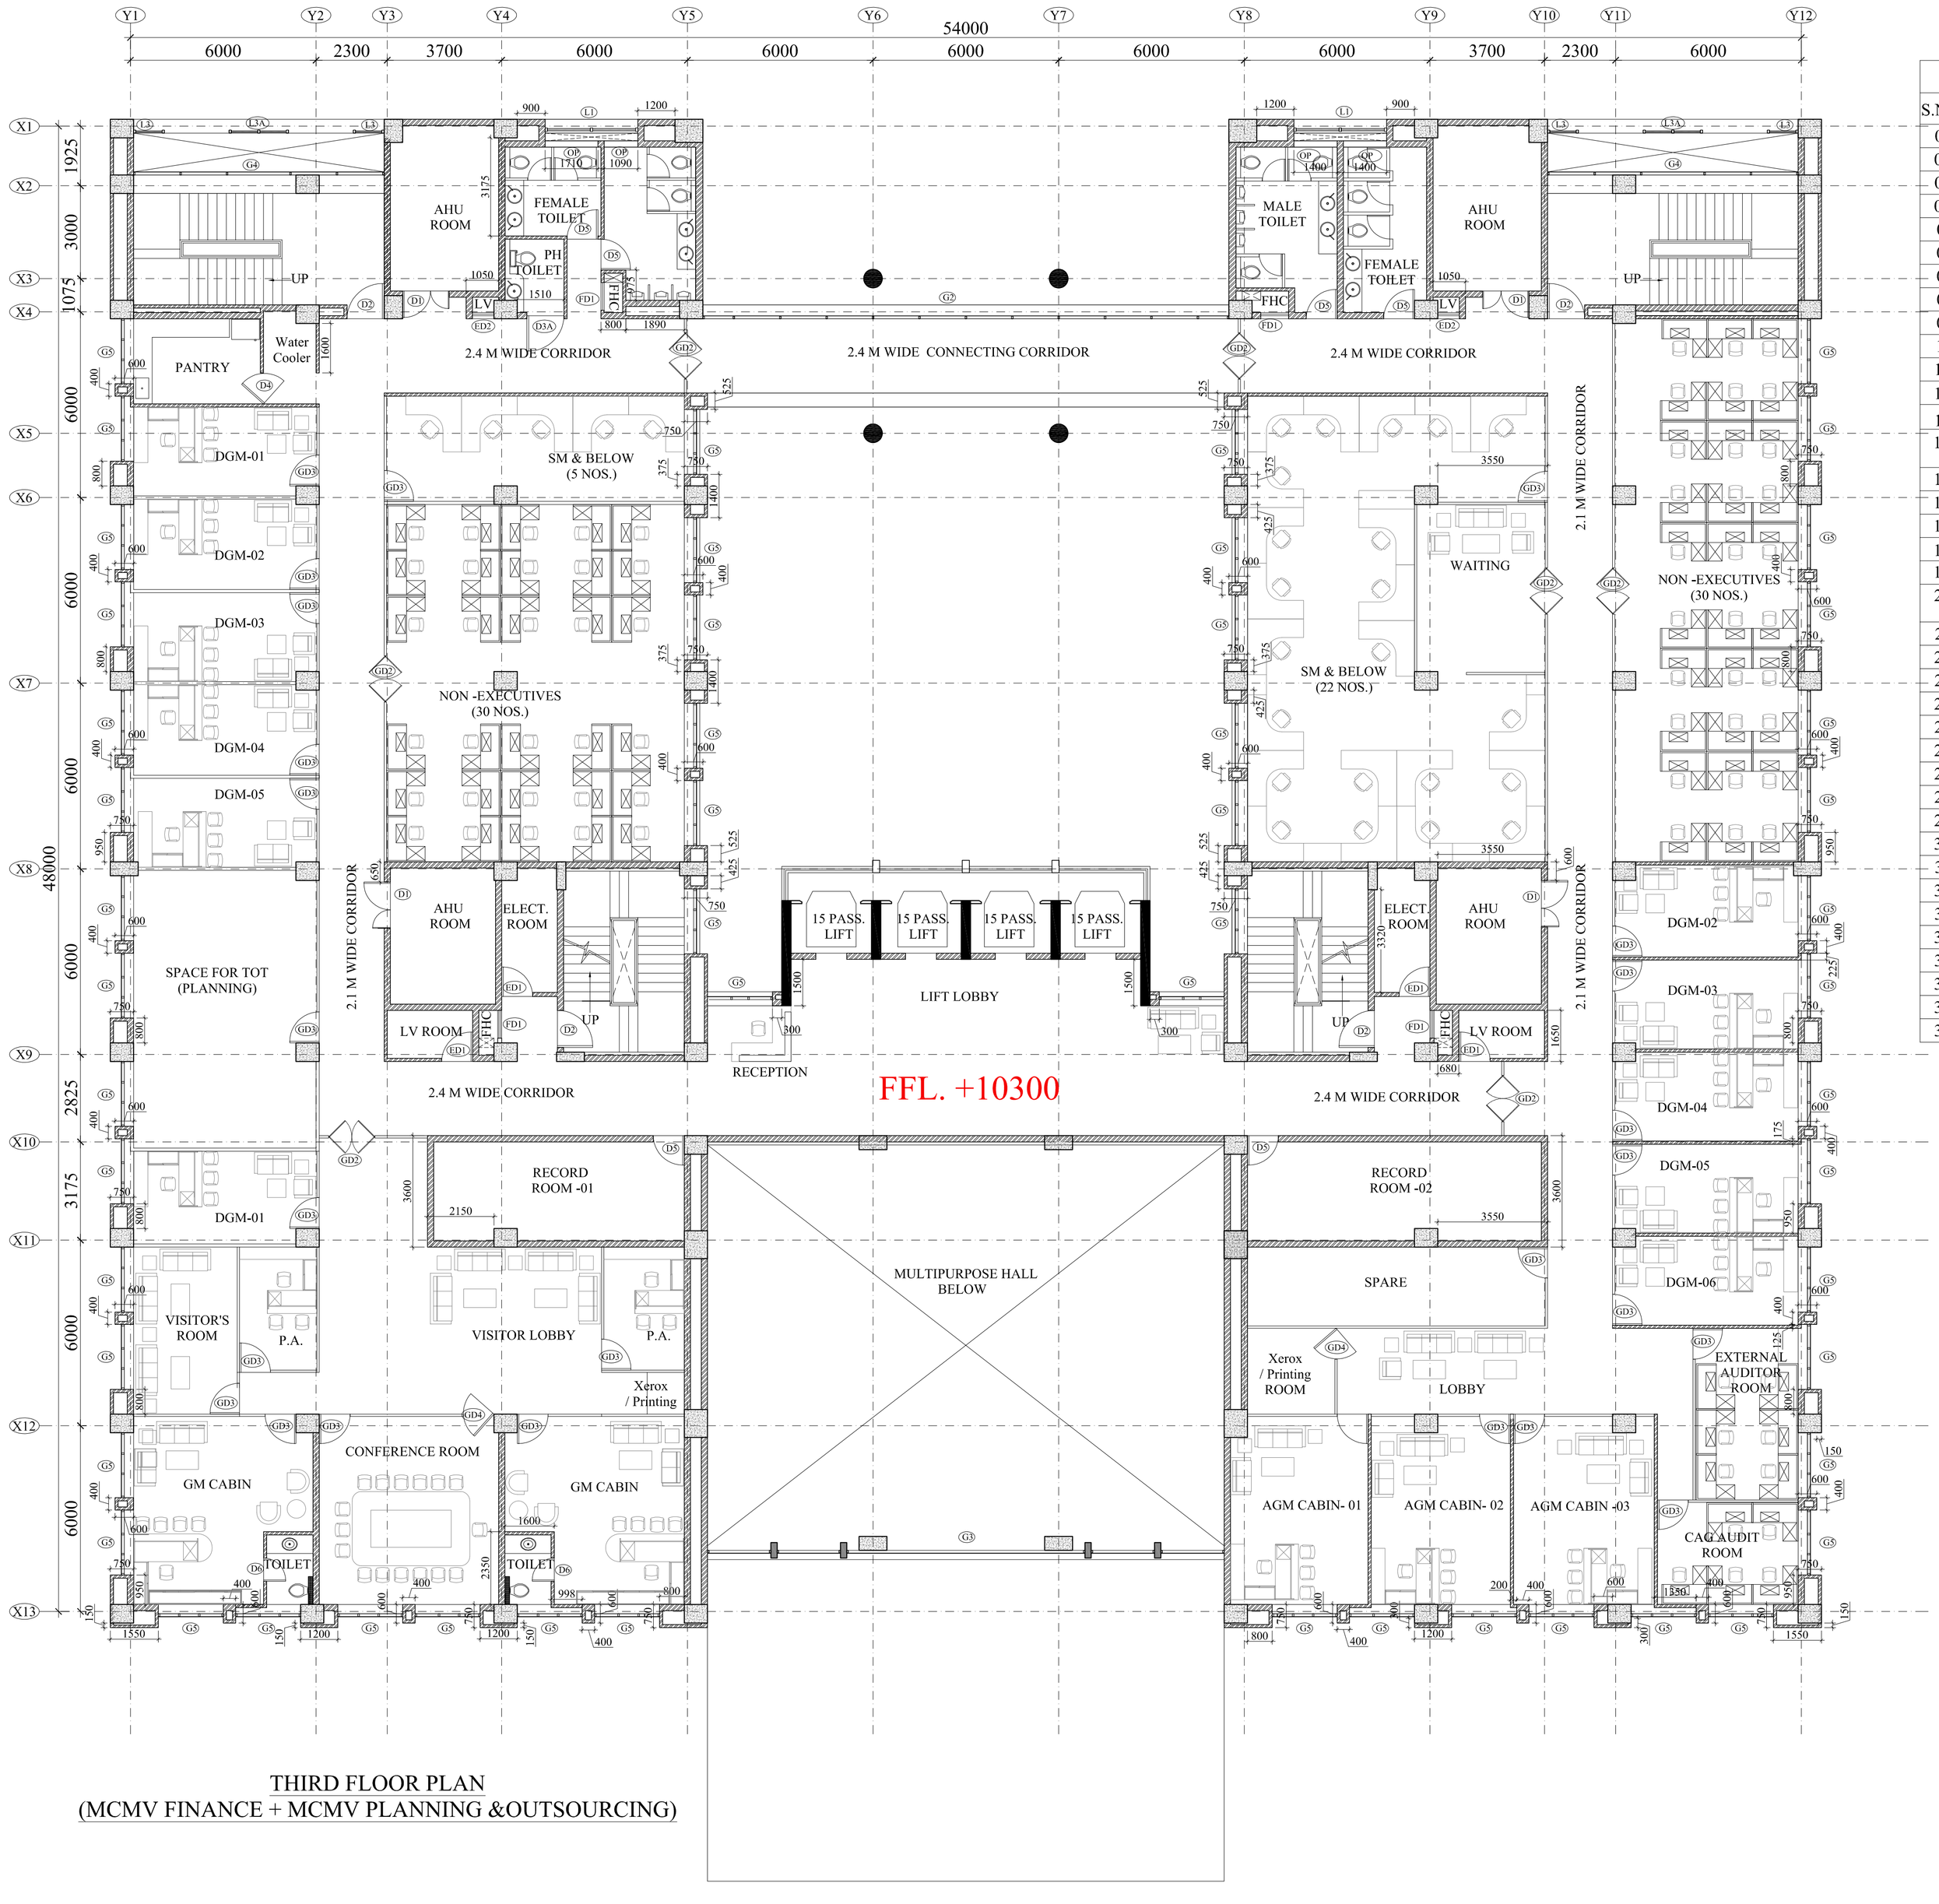

THIRD FLOOR PLAN
(MCMV FINANCE + MCMV PLANNING &OUTSOURCING)

DOOR-WINDOW OPENING SCHEDULE

S.NO.	TYPE	WIDTH	CILL	LINTEL	DISCRIPTION
01	D1	1500	-------	2400	A.H.U. DOOR
02	D2	1200	-------	2400	STAIRCASE DOOR
03	D3	1200	-------	2400	KITCHEN DOOR
04	D3A	1200	-------	2400	PH TOILET DOOR
05	D4	1000	-------	2400	Swing Door w/vision Panel
06	D5	1000	-------	2400	Door for Toilet,Record etc.
07	D6	750	-------	2100	Attached TOILET DOOR
08	D7	2000	-------	2400	ACOUSTICAL DOOR
09	ED1	1200	-------	2400	ELECTRICAL DOOR
10	ED2	750	100	2100	ELECTRICAL DOOR
11	ED3	2000	-------	2400	ELECTRICAL DOOR
12	FD1	900	100	2100	FHC DOOR
13	GD1	1800	-------	2400	SLIDING Glass Door
14	GD2	1500	-------	2400	Double Panel Swing Glass Door
15	GD3	1000	-------	2400	GLASS DOOR
16	GD4	1000	-------	2400	SWING GLASS DOOR
17	GD5	1200	-------	2400	GLASS DOOR
18	GD5A	1200	-------	2400	SWING GLASS DOOR
19	GD6	1150	-------	2400	SWING GLASS DOOR
20	GD7	1800	-------	2400	AUTOMATIC SLIDING DOOR
21	L1	3000	100	B.O.B.	ALUMINIUM LOUVERS
22	L2	1800	100	B.O.B.	ALUMINIUM LOUVERS
23	L3	1000	100	B.O.B.	ALUMINIUM LOUVERS
24	L3A	2000	100	B.O.B.	ALUMINIUM LOUVERS
25	L4	17000	100	B.O.B.	ALUMINIUM LOUVERS
26	G1	16700	--------	AS/ELE.	Double heightGLAZING
27	G1A	16700	--------	AS/ELE.	Double heightGLAZING
28	G2	17000	--------	AS/ELE	GLAZING
29	G2A	17000	--------	AS/ELE	GLAZING
30	G3	16700	--------	AS/ELE	Triple height GLAZING
31	G4	8100	--------	AS/ELE	GLAZING
32	G5	2100	--------	AS/ELE	GLAZING
33	G5A	2100	--------	AS/ELE	GLAZING
34	G6	1900	--------	AS/ELE	GLAZING
35	G7	4600	--------	AS/ELE	GLAZING
36	G8	2100	--------	AS/ELE	GLAZING
37	G8A	2100	--------	AS/ELE	GLAZING
38	OP	As/Plan	--------	B.O.B.	OPENING

THIS DRAWING IS THE PROPERTY OF THE DESIGN ASSOCIATES INC. AND SHALL NOT BE COPIED OR USED IN ANY MANNER WITHOUT PRIOR PERMISSION.

KEY PLAN

NOTES:

1. ALL DIMENSIONS ARE IN MM.
2. ALL DIMENSIONS ARE TO BE READ AND NOT MEASURED.
3. ALL LEVELS ARE IN METERS.
4. GRID DIMENSIONS AND PLOT LINES ARE TO BE STRICTLY ADHERED TO.
5. ALL LEVELS INCLUDING FLOOR LEVELS, CILL & LINTEL LEVELS, LANDING LEVELS, PARAPET HEIGHT/ LEVELS, LEVELS OF HORIZONTAL PROJECTION & BANDS INCLUDING ANY SURFACE FEATURES INDICATED IN THE DRAWINGS ARE TO BE STRICTLY ADHERED TO.
6. IN CASE OF ANY DISCREPANCY BETWEEN ANY DRAWING, ARCHITECT HAS TO BE INFORMED PRIOR TO ANY EXECUTION.

MARK	DATE	DESCRIPTION
R2		REVISION
R1		REVISION
GFC		GOOD FOR CONSTRUCTION
AC		ADVANCE COPY

OWNER-

GOA SHIPYARD LIMITED
(A Govt. of India Undertaking)
VASCO DA GAMA, GOA, 403802
contactus@goashipyard.com
TEL.No: -(0832) 251252-56, 2512359
FAX No: -(0091-832) 2514232, 2512148

EXECUTING AGENCY-

NBCC (INDIA) LIMITED
(Formerly National Buildings Construction Limited
(A Government of India Enterprise)
NBCC Bhawan, Lodhi Road
New Delhi - 110 003, India
Telephone No : 011 - 24367314 - 17, 24367573
Fax : 011 - 24366995

ARCHITECTS-

DESIGN ASSOCIATES INC.
A - 163, Sector - 136,
Noida - Greater Noida Expressway,
Noida - 201301, Phone no: 0120-2428600/30
e-mail: matinder.sharma@designassociates.in

MECHANICAL CONSULTANT-
DESIGN CENTER CONSULTING ENGINEERS, NEW DELHI

ELECTRICAL CONSULTANT-
DESIGN CENTER CONSULTING ENGINEERS, NEW DELHI

PLUMBING CONSULTANT-
DESIGN CENTER CONSULTING ENGINEERS, NEW DELHI

STRUCTURE CONSULTANT-
LKT ENGINEERING CONSULTANTS LTD.
19/49, Sukhsagar,New Delhi-110027
Phone:+011-45565818,Tel/Fax:+011-25126129
info@lktengineering.com
http:\\www.lktengineering.com

PROJECT-
CONSTRUCTION OF MCMV OFFICE BUILDING AT GOA SHIPYARD, GOA


DRAWING TITLE-
THIRD FLOOR PLAN

DRAWING PURPOSE-
TENDER DRAWING

JOB NO. -	DWG. REF. NO.-	DATE-
538	----------	----------
SCALE-	REVISION-	DATE OF ISSUE-
1:110	----------	03.01.17

DWG. NO.-
538/GSL/TD/AR/155

	SHEET SIZE-	SHEET NO-
	A1	05
	DRAWN BY-	CHECKED BY-
	RAJEEV	MATINDER

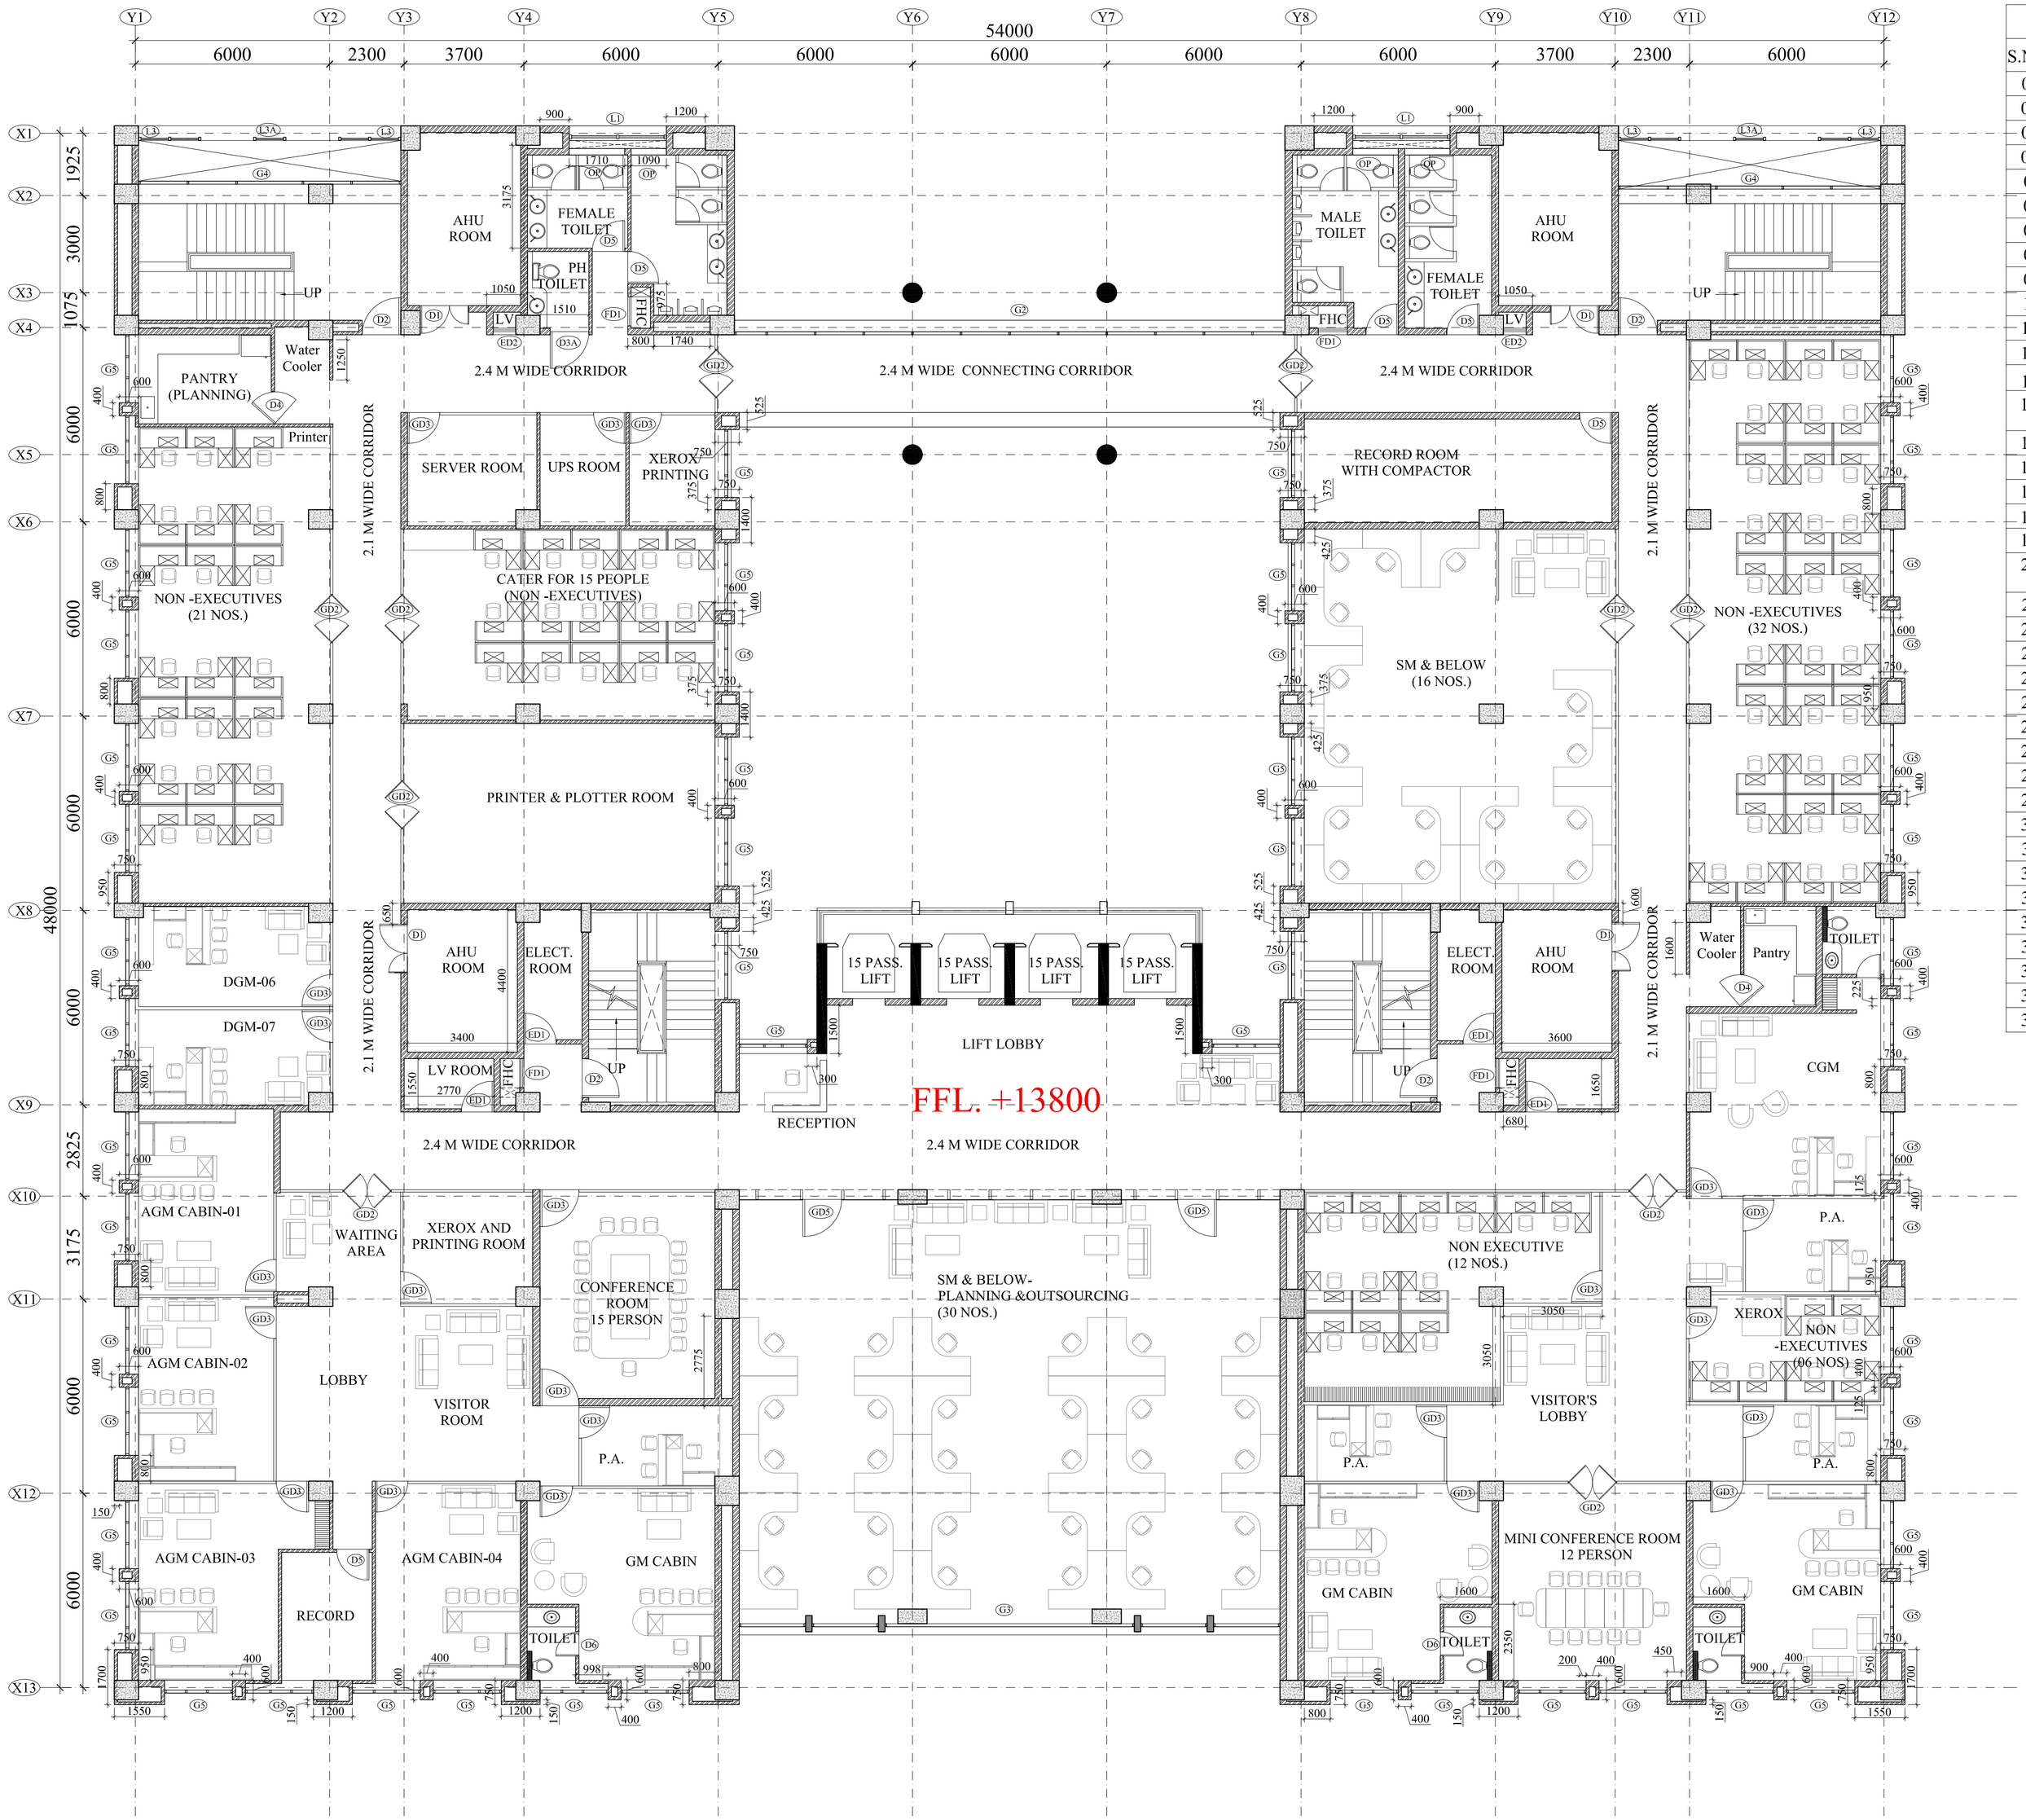

FOURTH FLOOR PLAN
(MCMV TECHNICAL SERVICES+ MCMV PLANNING)

DOOR-WINDOW OPENING SCHEDULE

S.NO.	TYPE	WIDTH	CILL	LINTEL	DISCRIPTION
01	D1	1500	-------	2400	A.H.U. DOOR
02	D2	1200	-------	2400	STAIRCASE DOOR
03	D3	1200	-------	2400	KITCHEN DOOR
04	D3A	1200	-------	2400	PH TOILET DOOR
05	D4	1000	-------	2400	Swing Door w/vision Panel
06	D5	1000	-------	2400	Door for Toilet,Record etc.
07	D6	750	-------	2100	Attached TOILET DOOR
08	D7	2000	-------	2400	ACOUSTICAL DOOR
09	ED1	1200	-------	2400	ELECTRICAL DOOR
10	ED2	750	100	2100	ELECTRICAL DOOR
11	ED3	2000	-------	2400	ELECTRICAL DOOR
12	FD1	900	100	2100	FHC DOOR
13	GD1	1800	-------	2400	SLIDING Glass Door
14	GD2	1500	-------	2400	Double Panel Swing Glass Door
15	GD3	1000	-------	2400	GLASS DOOR
16	GD4	1000	-------	2400	SWING GLASS DOOR
17	GD5	1200	-------	2400	GLASS DOOR
18	GD5A	1200	-------	2400	SWING GLASS DOOR
19	GD6	1150	-------	2400	SWING GLASS DOOR
20	GD7	1800	-------	2400	AUTOMATIC SLIDING DOOR
21	L1	3000	100	B.O.B.	ALUMINIUM LOUVERS
22	L2	1800	100	B.O.B.	ALUMINIUM LOUVERS
23	L3	1000	100	B.O.B.	ALUMINIUM LOUVERS
24	L3A	2000	100	B.O.B.	ALUMINIUM LOUVERS
25	L4	17000	100	B.O.B.	ALUMINIUM LOUVERS
26	G1	16700	--------	AS/ELE.	Double heightGLAZING
27	G1A	16700	--------	AS/ELE.	Double heightGLAZING
28	G2	17000	--------	AS/ELE	GLAZING
29	G2A	17000	--------	AS/ELE	GLAZING
30	G3	16700	--------	AS/ELE	Triple height GLAZING
31	G4	8100	--------	AS/ELE	GLAZING
32	G5	2100	--------	AS/ELE	GLAZING
33	G5A	2100	--------	AS/ELE	GLAZING
34	G6	1900	--------	AS/ELE	GLAZING
35	G7	4600	--------	AS/ELE	GLAZING
36	G8	2100	--------	AS/ELE	GLAZING
37	G8A	2100	--------	AS/ELE	GLAZING
38	OP	As/Plan	--------	B.O.B.	OPENING

THIS DRAWING IS THE PROPERTY OF THE DESIGN ASSOCIATES INC. AND SHALL NOT BE COPIED OR USED IN ANY MANNER WITHOUT PRIOR PERMISSION.

KEY PLAN

NOTES:

1. ALL DIMENSIONS ARE IN MM.
2. ALL DIMENSIONS ARE TO BE READ AND NOT MEASURED.
3. ALL LEVELS ARE IN METERS.
4. GRID DIMENSIONS AND PLOT LINES ARE TO BE STRICTLY ADHERED TO.
5. ALL LEVELS INCLUDING FLOOR LEVELS, CILL & LINTEL LEVELS, LANDING LEVELS, PARAPET HEIGHT/ LEVELS, LEVELS OF HORIZONTAL PROJECTION & BANDS INCLUDING ANY SURFACE FEATURES INDICATED IN THE DRAWINGS ARE TO BE STRICTLY ADHERED TO.
6. IN CASE OF ANY DISCREPANCY BETWEEN ANY DRAWING, ARCHITECT HAS TO BE INFORMED PRIOR TO ANY EXECUTION.

R2		REVISION
R1		REVISION
GFC		GOOD FOR CONSTRUCTION
AC		ADVANCE COPY
MARK	DATE	DESCRIPTION

OWNER-

GOA SHIPYARD LIMITED
(A Govt. of India Undertaking)
VASCO DA GAMA, GOA, 403802
contactus@goashipyard.com
TEL.No: - (0832) 251252-56, 2512359
FAX No: -(0091-832) 2514232, 2512148

EXECUTING AGENCY-

NBCC (INDIA) LIMITED
(Formerly National Buildings Construction Limited
(A Government of India Enterprise)
NBCC Bhawan, Lodhi Road
New Delhi - 110 003, India
Telephone No : 011 - 24367314 - 17, 24367573
Fax : 011 - 24366995

ARCHITECTS-

DESIGN ASSOCIATES INC.
ARCHITECTURE
A - 163, Sector - 136,
Noida - Greater Noida Expressway,
Noida - 201301, Phone no: 0120-2428600/30
e-mail: matinder.sharma@designassociates.in

MECHANICAL CONSULTANT-
DESIGN CENTER CONSULTING ENGINEERS, NEW DELHI

ELECTRICAL CONSULTANT-
DESIGN CENTER CONSULTING ENGINEERS, NEW DELHI

PLUMBING CONSULTANT-
DESIGN CENTER CONSULTING ENGINEERS, NEW DELHI

STRUCTURE CONSULTANT-
LKT ENGINEERING CONSULTANTS LTD.
10/49, Subhash Nagar,New Delhi-110027
Phone:+011-45565818,Tel/Fax:+011-25126129
info@lktengineering.com
http://www.lktengineering.com

PROJECT-
CONSTRUCTION OF MCMV OFFICE BUILDING AT GOA SHIPYARD, GOA


DRAWING TITLE-
FOURTH FLOOR PLAN

DRAWING PURPOSE-
TENDER DRAWING

JOB NO. -	DWG. REF. NO.-	DATE-
538	----------	----------
SCALE-	REVISION-	DATE OF ISSUE-
1:110	----------	03.01.17

DWG. NO.-
538/GSL/TD/AR/156

	SHEET SIZE-	SHEET NO-
	A1	06
	DRAWN BY-	CHECKED BY-
	RAJEEV	MATINDER

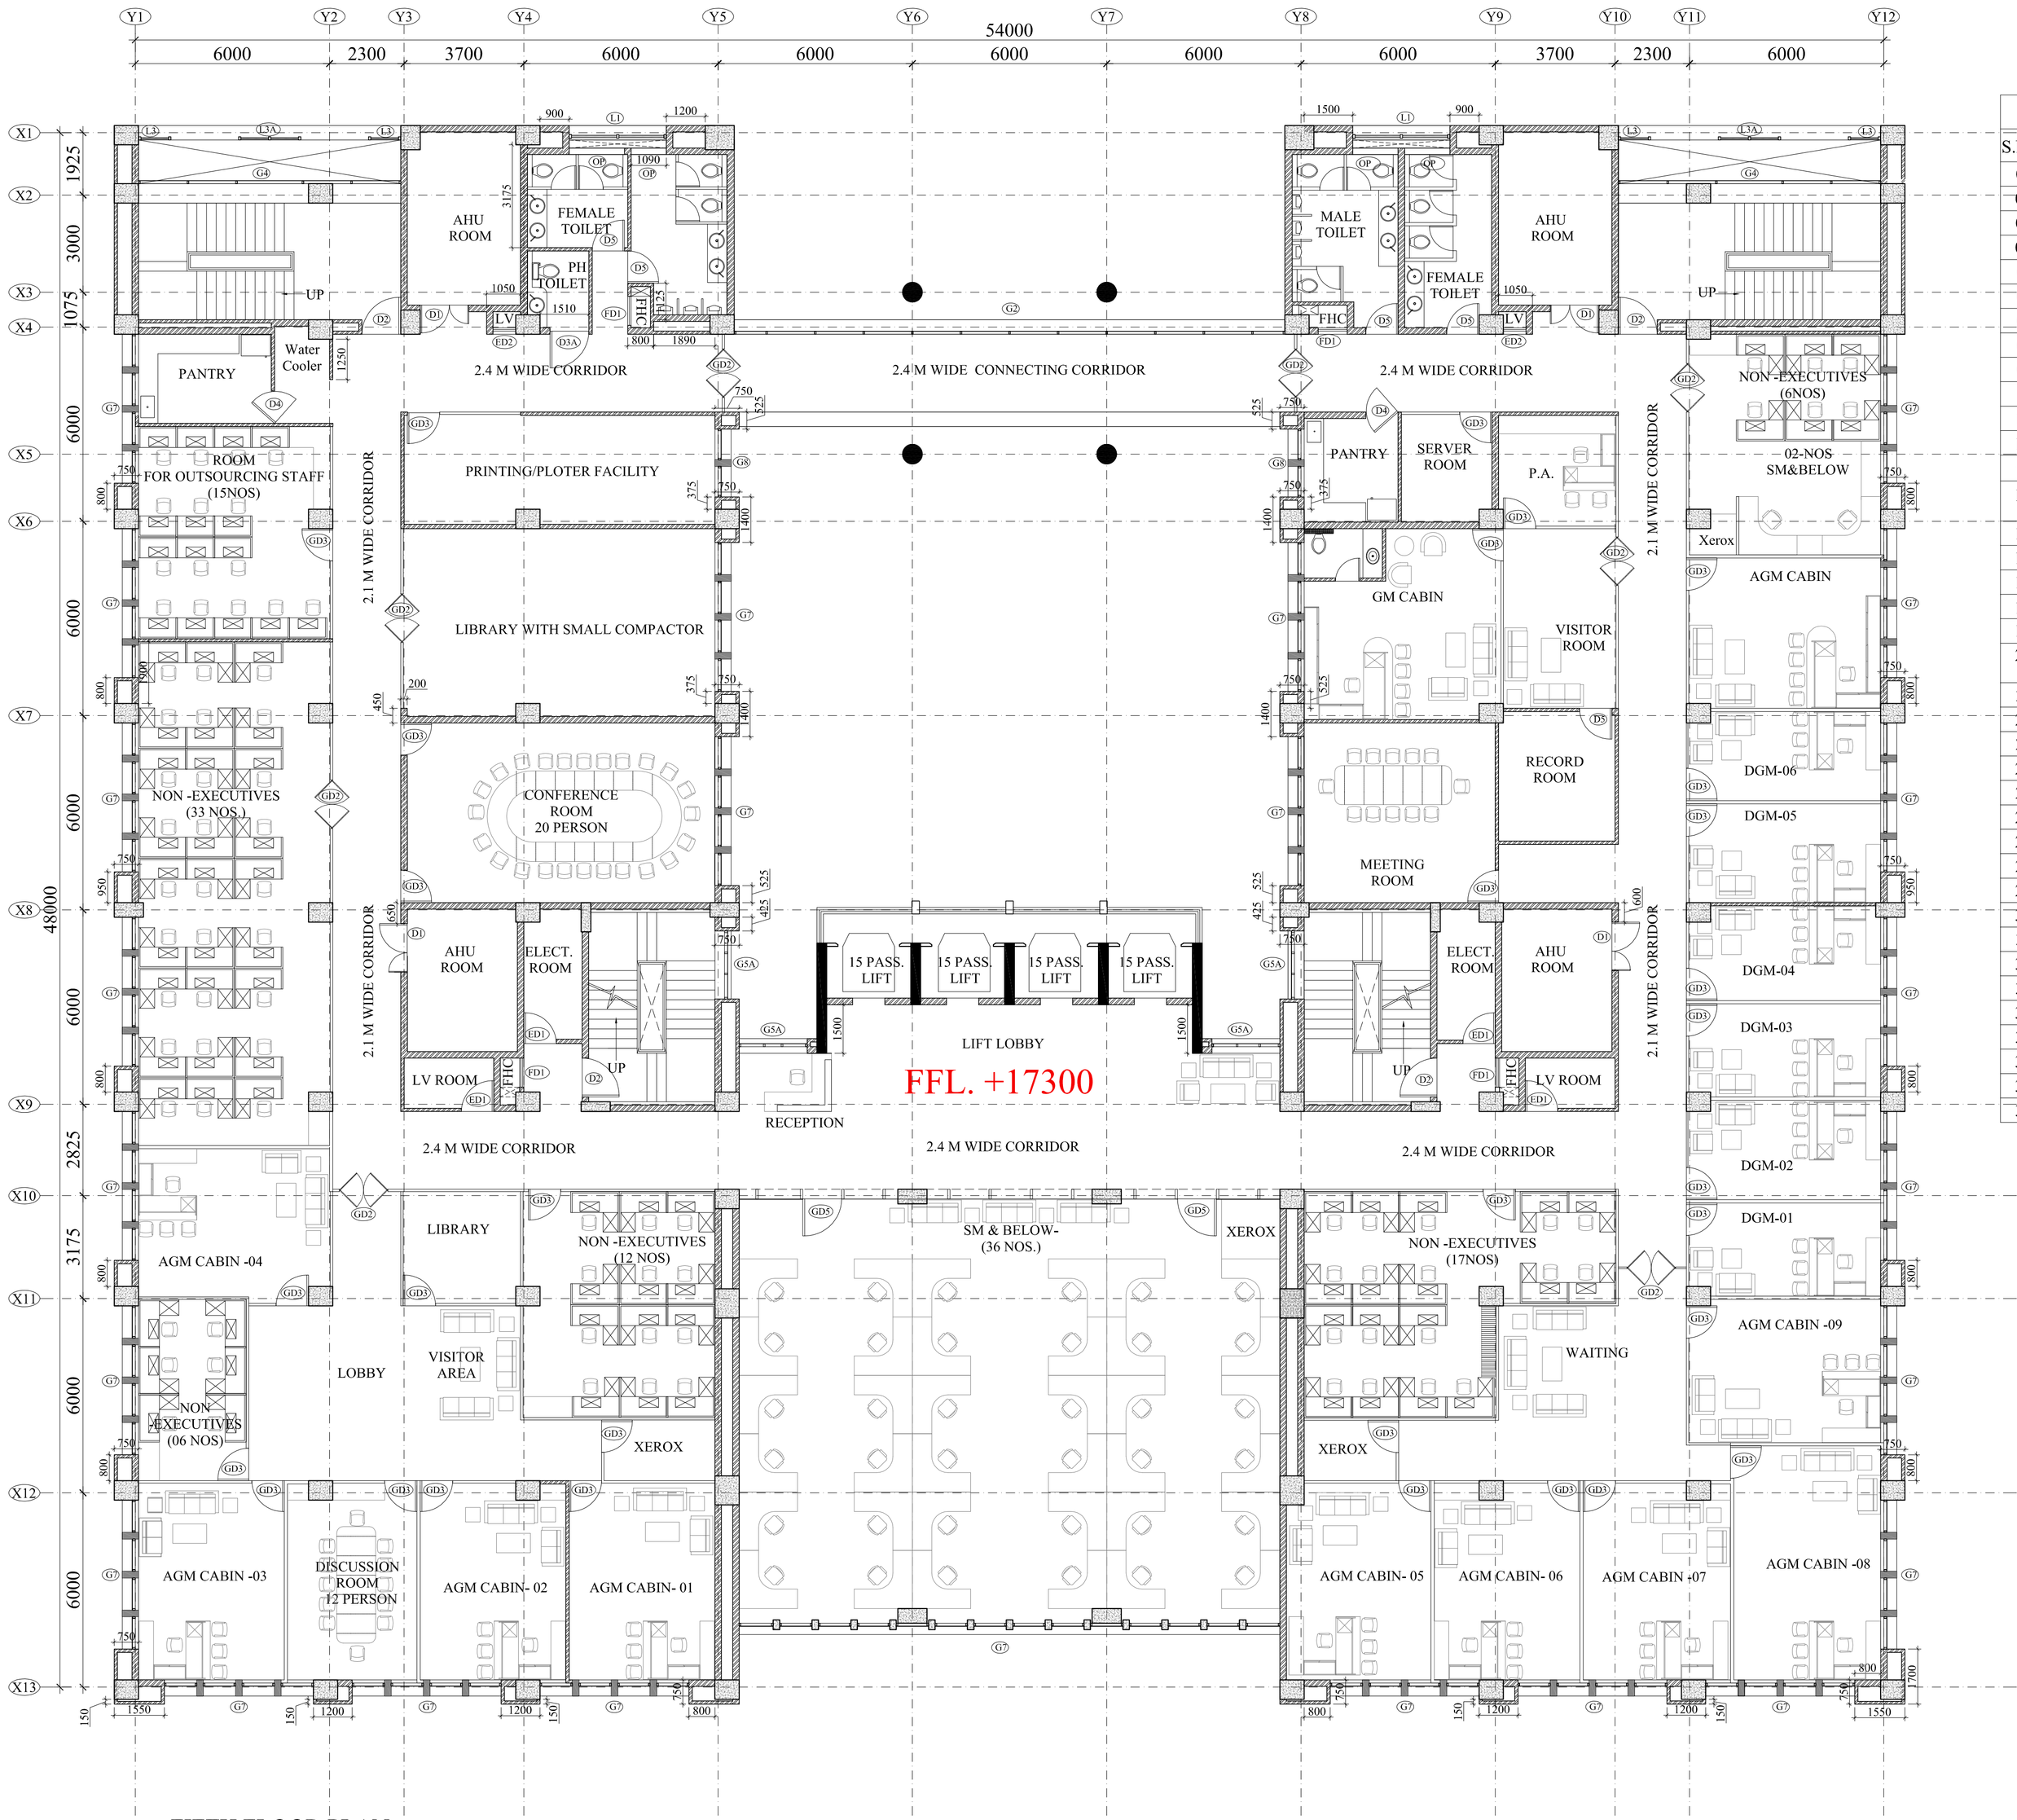

FIFTH FLOOR PLAN
(MCMV TECHNICAL SERVICES+GES)

DOOR-WINDOW OPENING SCHEDULE

S.NO.	TYPE	WIDTH	CILL	LINTEL	DISCRIPTION
01	D1	1500	-------	2400	A.H.U. DOOR
02	D2	1200	-------	2400	STAIRCASE DOOR
03	D3	1200	-------	2400	KITCHEN DOOR
04	D3A	1200	-------	2400	PH TOILET DOOR
05	D4	1000	-------	2400	Swing Door w/vision Panel
06	D5	1000	-------	2400	Door for Toilet,Record etc.
07	D6	750	-------	2100	Attached TOILET DOOR
08	D7	2000	-------	2400	ACOUSTICAL DOOR
09	ED1	1200	-------	2400	ELECTRICAL DOOR
10	ED2	750	100	2100	ELECTRICAL DOOR
11	ED3	2000	-------	2400	ELECTRICAL DOOR
12	FD1	900	100	2100	FHC DOOR
13	GD1	1800	-------	2400	SLIDING Glass Door
14	GD2	1500	-------	2400	Double Panel Swing Glass Door
15	GD3	1000	-------	2400	GLASS DOOR
16	GD4	1000	-------	2400	SWING GLASS DOOR
17	GD5	1200	-------	2400	GLASS DOOR
18	GD5A	1200	-------	2400	SWING GLASS DOOR
19	GD6	1150	-------	2400	SWING GLASS DOOR
20	GD7	1800	-------	2400	AUTOMATIC SLIDING DOOR
21	L1	3000	100	B.O.B.	ALUMINIUM LOUVERS
22	L2	1800	100	B.O.B.	ALUMINIUM LOUVERS
23	L3	1000	100	B.O.B.	ALUMINIUM LOUVERS
24	L3A	2000	100	B.O.B.	ALUMINIUM LOUVERS
25	L4	17000	100	B.O.B.	ALUMINIUM LOUVERS
26	G1	16700	--------	AS/ELE.	Double heightGLAZING
27	G1A	16700	--------	AS/ELE.	Double heightGLAZING
28	G2	17000	--------	AS/ELE	GLAZING
29	G2A	17000	--------	AS/ELE	GLAZING
30	G3	16700	--------	AS/ELE	Triple height GLAZING
31	G4	8100	--------	AS/ELE	GLAZING
32	G5	2100	--------	AS/ELE	GLAZING
33	G5A	2100	--------	AS/ELE	GLAZING
34	G6	1900	--------	AS/ELE	GLAZING
35	G7	4600	--------	AS/ELE	GLAZING
36	G8	2100	--------	AS/ELE	GLAZING
37	G8A	2100	--------	AS/ELE	GLAZING
38	OP	As/Plan	--------	B.O.B.	OPENING

THIS DRAWING IS THE PROPERTY OF THE DESIGN ASSOCIATES INC. AND SHALL NOT BE COPIED OR USED IN ANY MANNER WITHOUT PRIOR PERMISSION.

KEY PLAN

NOTES:

1. ALL DIMENSIONS ARE IN MM.
2. ALL DIMENSIONS ARE TO BE READ AND NOT MEASURED.
3. ALL LEVELS ARE IN METERS.
4. GRID DIMENSIONS AND PLOT LINES ARE TO BE STRICTLY ADHERED TO.
5. ALL LEVELS INCLUDING FLOOR LEVELS, CILL & LINTEL LEVELS, LANDING LEVELS, PARAPET HEIGHT/ LEVELS, LEVELS OF HORIZONTAL PROJECTION & BANDS INCLUDING ANY SURFACE FEATURES INDICATED IN THE DRAWINGS ARE TO BE STRICTLY ADHERED TO.
6. IN CASE OF ANY DISCREPANCY BETWEEN ANY DRAWING, ARCHITECT HAS TO BE INFORMED PRIOR TO ANY EXECUTION.

R2		REVISION
R1		REVISION
GFC		GOOD FOR CONSTRUCTION
AC		ADVANCE COPY
MARK	DATE	DESCRIPTION

OWNER-

GOA SHIPYARD LIMITED
(A Govt. of India Undertaking)
VASCO DA GAMA, GOA, 403802
contactus@goashipyard.com
TEL.No: - (0832) 251252-56, 2512359
FAX No: -(0091-832) 2514232, 2512148

EXECUTING AGENCY-

NBCC (INDIA) LIMITED
(Formerly National Buildings Construction Limited
(A Government of India Enterprise)
NBCC Bhawan, Lodhi Road
New Delhi - 110 003, India
Telephone No : 011 - 24367314 - 17, 24367573
Fax : 011 - 24366995

ARCHITECTS-

DESIGN ASSOCIATES INC.
ARCHITECTURE
A - 163, Sector - 136,
Noida - Greater Noida Expressway,
Noida - 201301, Phone no: 0120-2428600/30
e-mail: matinder.sharma@designassociates.in

MECHANICAL CONSULTANT-
DESIGN CENTER CONSULTING ENGINEERS, NEW DELHI

ELECTRICAL CONSULTANT-
DESIGN CENTER CONSULTING ENGINEERS, NEW DELHI

PLUMBING CONSULTANT-
DESIGN CENTER CONSULTING ENGINEERS, NEW DELHI

STRUCTURE CONSULTANT-
LKT ENGINEERING CONSULTANTS LTD.
10/49, Subhash Nagar,New Delhi-110027
Phone:+011-45565818,Tel/Fax:+011-25126129
info@lktengineering.com
http://www.lktengineering.com

PROJECT-
CONSTRUCTION OF MCMV OFFICE BUILDING AT GOA SHIPYARD, GOA

DRAWING TITLE-
FIFTH FLOOR PLAN


DRAWING PURPOSE-
TENDER DRAWING

JOB NO. -	DWG. REF. NO.-	DATE-
538	----------	----------
SCALE-	REVISION-	DATE OF ISSUE-
1:110	----------	03.01.17

DWG. NO.-
538/GSL/TD/AR/157

	SHEET SIZE-	SHEET NO-
	A1	07
	DRAWN BY-	CHECKED BY-
	RAJEEV	MATINDER

SIXTH FLOOR PLAN
(DIRECTORS+ CMD+ VIGILANCE+ CS&EL)

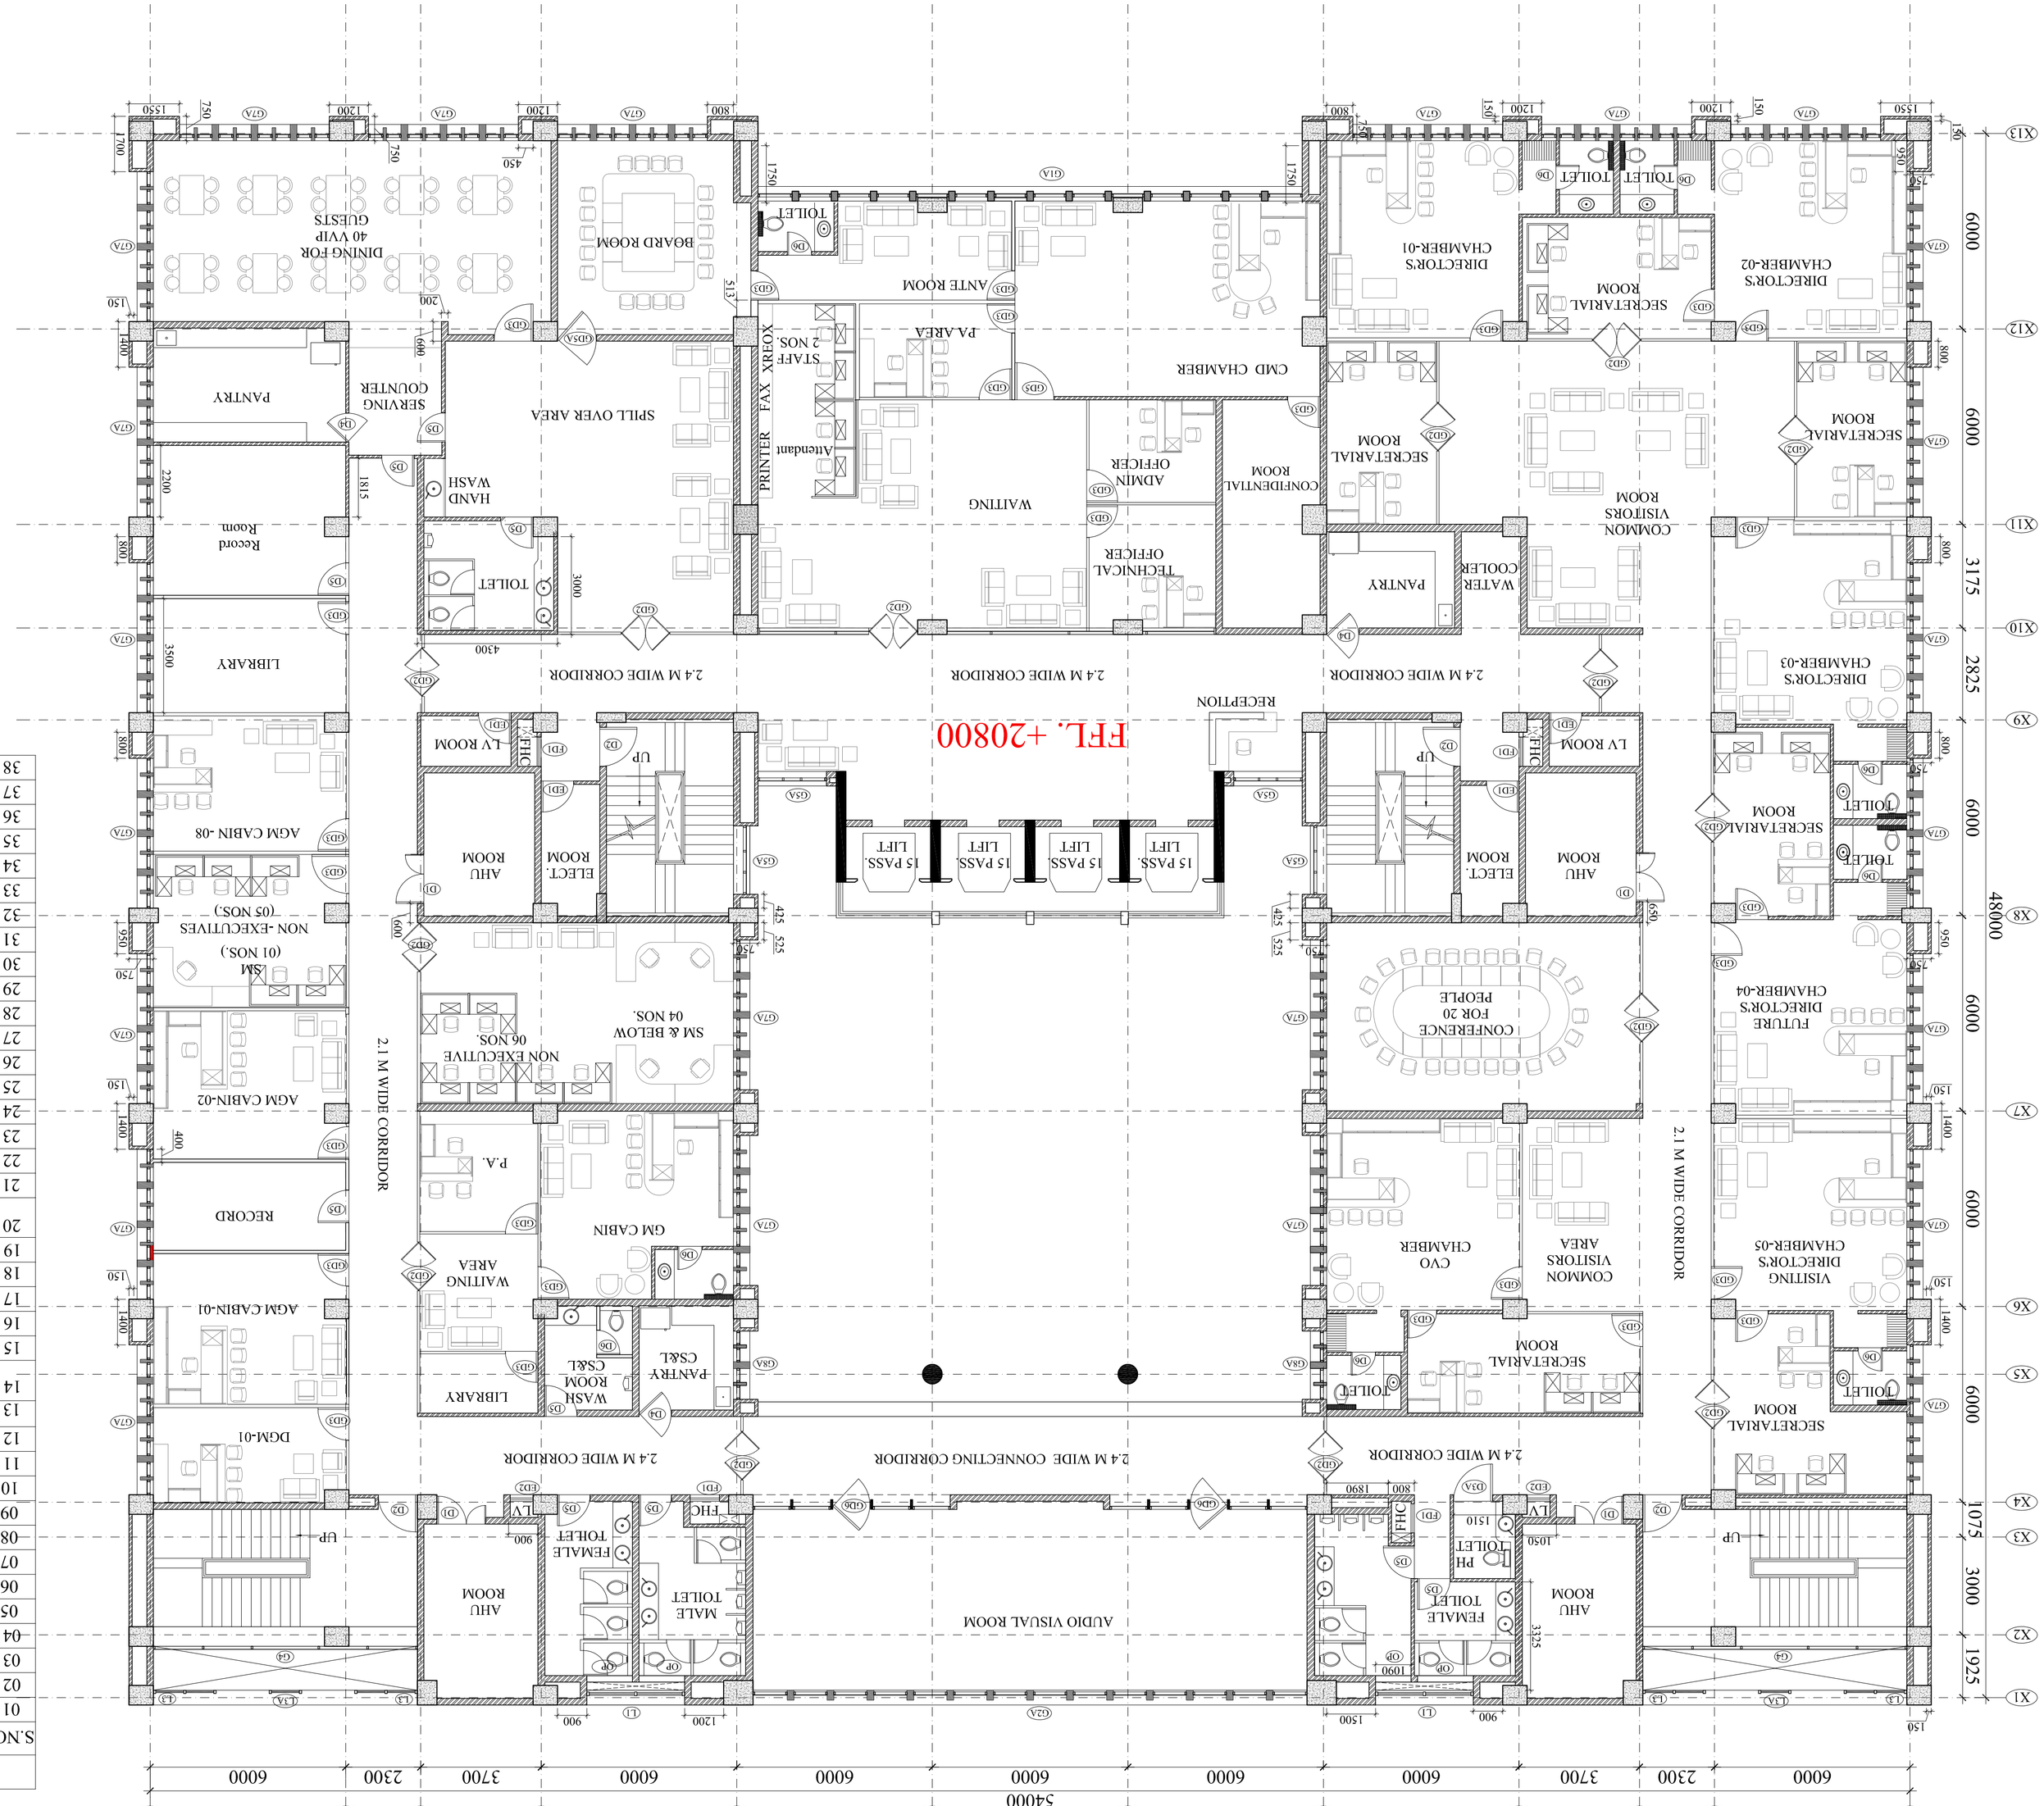

DOOR-WINDOW OPENING SCHEDULE

S.NO.	TYPE	WIDTH	CILL	LINTEL	DISCRIPTION
01	D1	1500	-------	2400	A.H.U. DOOR
02	D2	1200	-------	2400	STAIRCASE DOOR
03	D3	1200	-------	2400	KITCHEN DOOR
04	D3A	1200	-------	2400	PH TOILET DOOR
05	D4	1000	-------	2400	Swing Door w/vision Panel
06	D5	1000	-------	2400	Door for Toilet,Record etc.
07	D6	750	-------	2100	Attached TOILET DOOR
08	D7	2000	-------	2400	ACOUSTICAL DOOR
09	ED1	1200	-------	2400	ELECTRICAL DOOR
10	ED2	750	100	2100	ELECTRICAL DOOR
11	ED3	2000	-------	2400	ELECTRICAL DOOR
12	FD1	900	100	2100	FHC DOOR
13	GD1	1800	-------	2400	SLIDING Glass Door
14	GD2	1500	-------	2400	Double Panel Swing Glass Door
15	GD3	1000	-------	2400	GLASS DOOR
16	GD4	1000	-------	2400	SWING GLASS DOOR
17	GD5	1200	-------	2400	GLASS DOOR
18	GD5A	1200	-------	2400	SWING GLASS DOOR
19	GD6	1150	-------	2400	SWING GLASS DOOR
20	GD7	1800	-------	2400	AUTOMATIC SLIDING DOOR
21	L1	3000	100	B.O.B.	ALUMINIUM LOUVERS
22	L2	1800	100	B.O.B.	ALUMINIUM LOUVERS
23	L3	1000	100	B.O.B.	ALUMINIUM LOUVERS
24	L3A	2000	100	B.O.B.	ALUMINIUM LOUVERS
25	L4	17000	100	B.O.B.	ALUMINIUM LOUVERS
26	G1	16700	-------	AS/ELE.	Double heighGLAZING
27	G1A	16700	-------	AS/ELE.	Double heighGLAZING
28	G2	17000	-------	AS/ELE	GLAZING
29	G2A	17000	-------	AS/ELE	GLAZING
30	G3	16700	-------	AS/ELE	Triple height GLAZING
31	G4	8100	-------	AS/ELE	GLAZING
32	G5	2100	-------	AS/ELE	GLAZING
33	G5A	2100	-------	AS/ELE	GLAZING
34	G6	1900	-------	AS/ELE	GLAZING
35	G7	4600	-------	AS/ELE	GLAZING
36	G8	2100	-------	AS/ELE	GLAZING
37	G8A	2100	-------	AS/ELE	GLAZING
38	OP	AS/Plan	-------	B.O.B.	OPENING

DESIGN ASSOCIATES INC.
A R C H I T E C T S
A - 163, Sector - 136,
Noida - Expressway,
Noida - 201301, Phone no: 0120-2428600/30
e-mail: mathur.sharma@designassociates.in

ARCHITECTS-

NBCC (INDIA) LIMITED
(Formerly National Buildings Construction Limited)
(A Government of India Enterprise)
NBCC Bhawan, Lodhi Road
New Delhi - 110 003, India
Telephone No : 011 - 24367314 - 17, 24367573
Fax : 011 - 24366995

EXECUTING AGENCY-

GOA SHIPYARD LIMITED
(A Govt. of India Undertaking)
VASCO DA GAMA, GOA, 403802
contactus@goashipyard.com
TEL-No: - (0832) 2512252-56, 2512359
FAX No: -(0091-832) 2514232, 2512148

OWNER-

MARK	DATE	DESCRIPTION
R2		REVISION
R1		REVISION
GFC		GOOD FOR CONSTRUCTION
AC		ADVANCE COPY

KEY PLAN

NOTES:
1. ALL DIMENSIONS ARE IN MM.
2. ALL DIMENSIONS ARE TO BE READ AND NOT MEASURED.
3. ALL LEVELS ARE IN METERS.
4. GRID DIMENSIONS AND PLOT LINES ARE TO BE STRICTLY ADHERED TO.
5. ALL LEVELS INCLUDING FLOOR LEVELS, CILL & LINTEL LEVELS, LANDING LEVELS, PARAPET HEIGHT, LEVELS, LEVELS OF HORIZONTAL FEATURES INDICATED IN THE DRAWINGS ARE TO BE STRICTLY ADHERED TO.
6. IN CASE OF ANY DISCREPANCY BETWEEN ANY DRAWING, ARCHITECT HAS TO BE INFORMED PRIOR TO ANY EXECUTION.

THIS DRAWING IS THE PROPERTY OF THE DESIGN ASSOCIATES INC. AND SHALL NOT BE COPIED OR USED IN ANY MANNER WITHOUT PRIOR PERMISSION.

DRAWN BY-	CHECKED BY-
RAJEEV	MATINDER
SHEET SIZE-	SHEET NO-
A1	08

SCALE-	REVISION-
1:110	----------
DWG. NO.-	DATE OF ISSUE-
538/GSL/TD/AR/158	03.01.17

JOB NO. -	DWG. REF. NO.-	DATE-
538	----------	----------

DRAWING PURPOSE-
TENDER DRAWING

DRAWING TITLE-
SIXTH FLOOR PLAN


PROJECT-
CONSTRUCTION OF MCMV OFFICE BUILDING AT GOA SHIPYARD, GOA

STRUCTURE CONSULTANT-
LKT ENGINEERING CONSULTANTS LTD.
10/49, Subhash Nagar,New Delhi-110027
Phone:-+011-45565881(6)Tel/Fax:-+011-25126129
info@lktengineering.com
http://www.lktengineering.com

PLUMBING CONSULTANT-
DESIGN CENTER CONSULTING ENGINEERS, NEW DELHI

ELECTRICAL CONSULTANT-
DESIGN CENTER CONSULTING ENGINEERS, NEW DELHI

MECHANICAL CONSULTANT-
DESIGN CENTER CONSULTING ENGINEERS, NEW DELHI

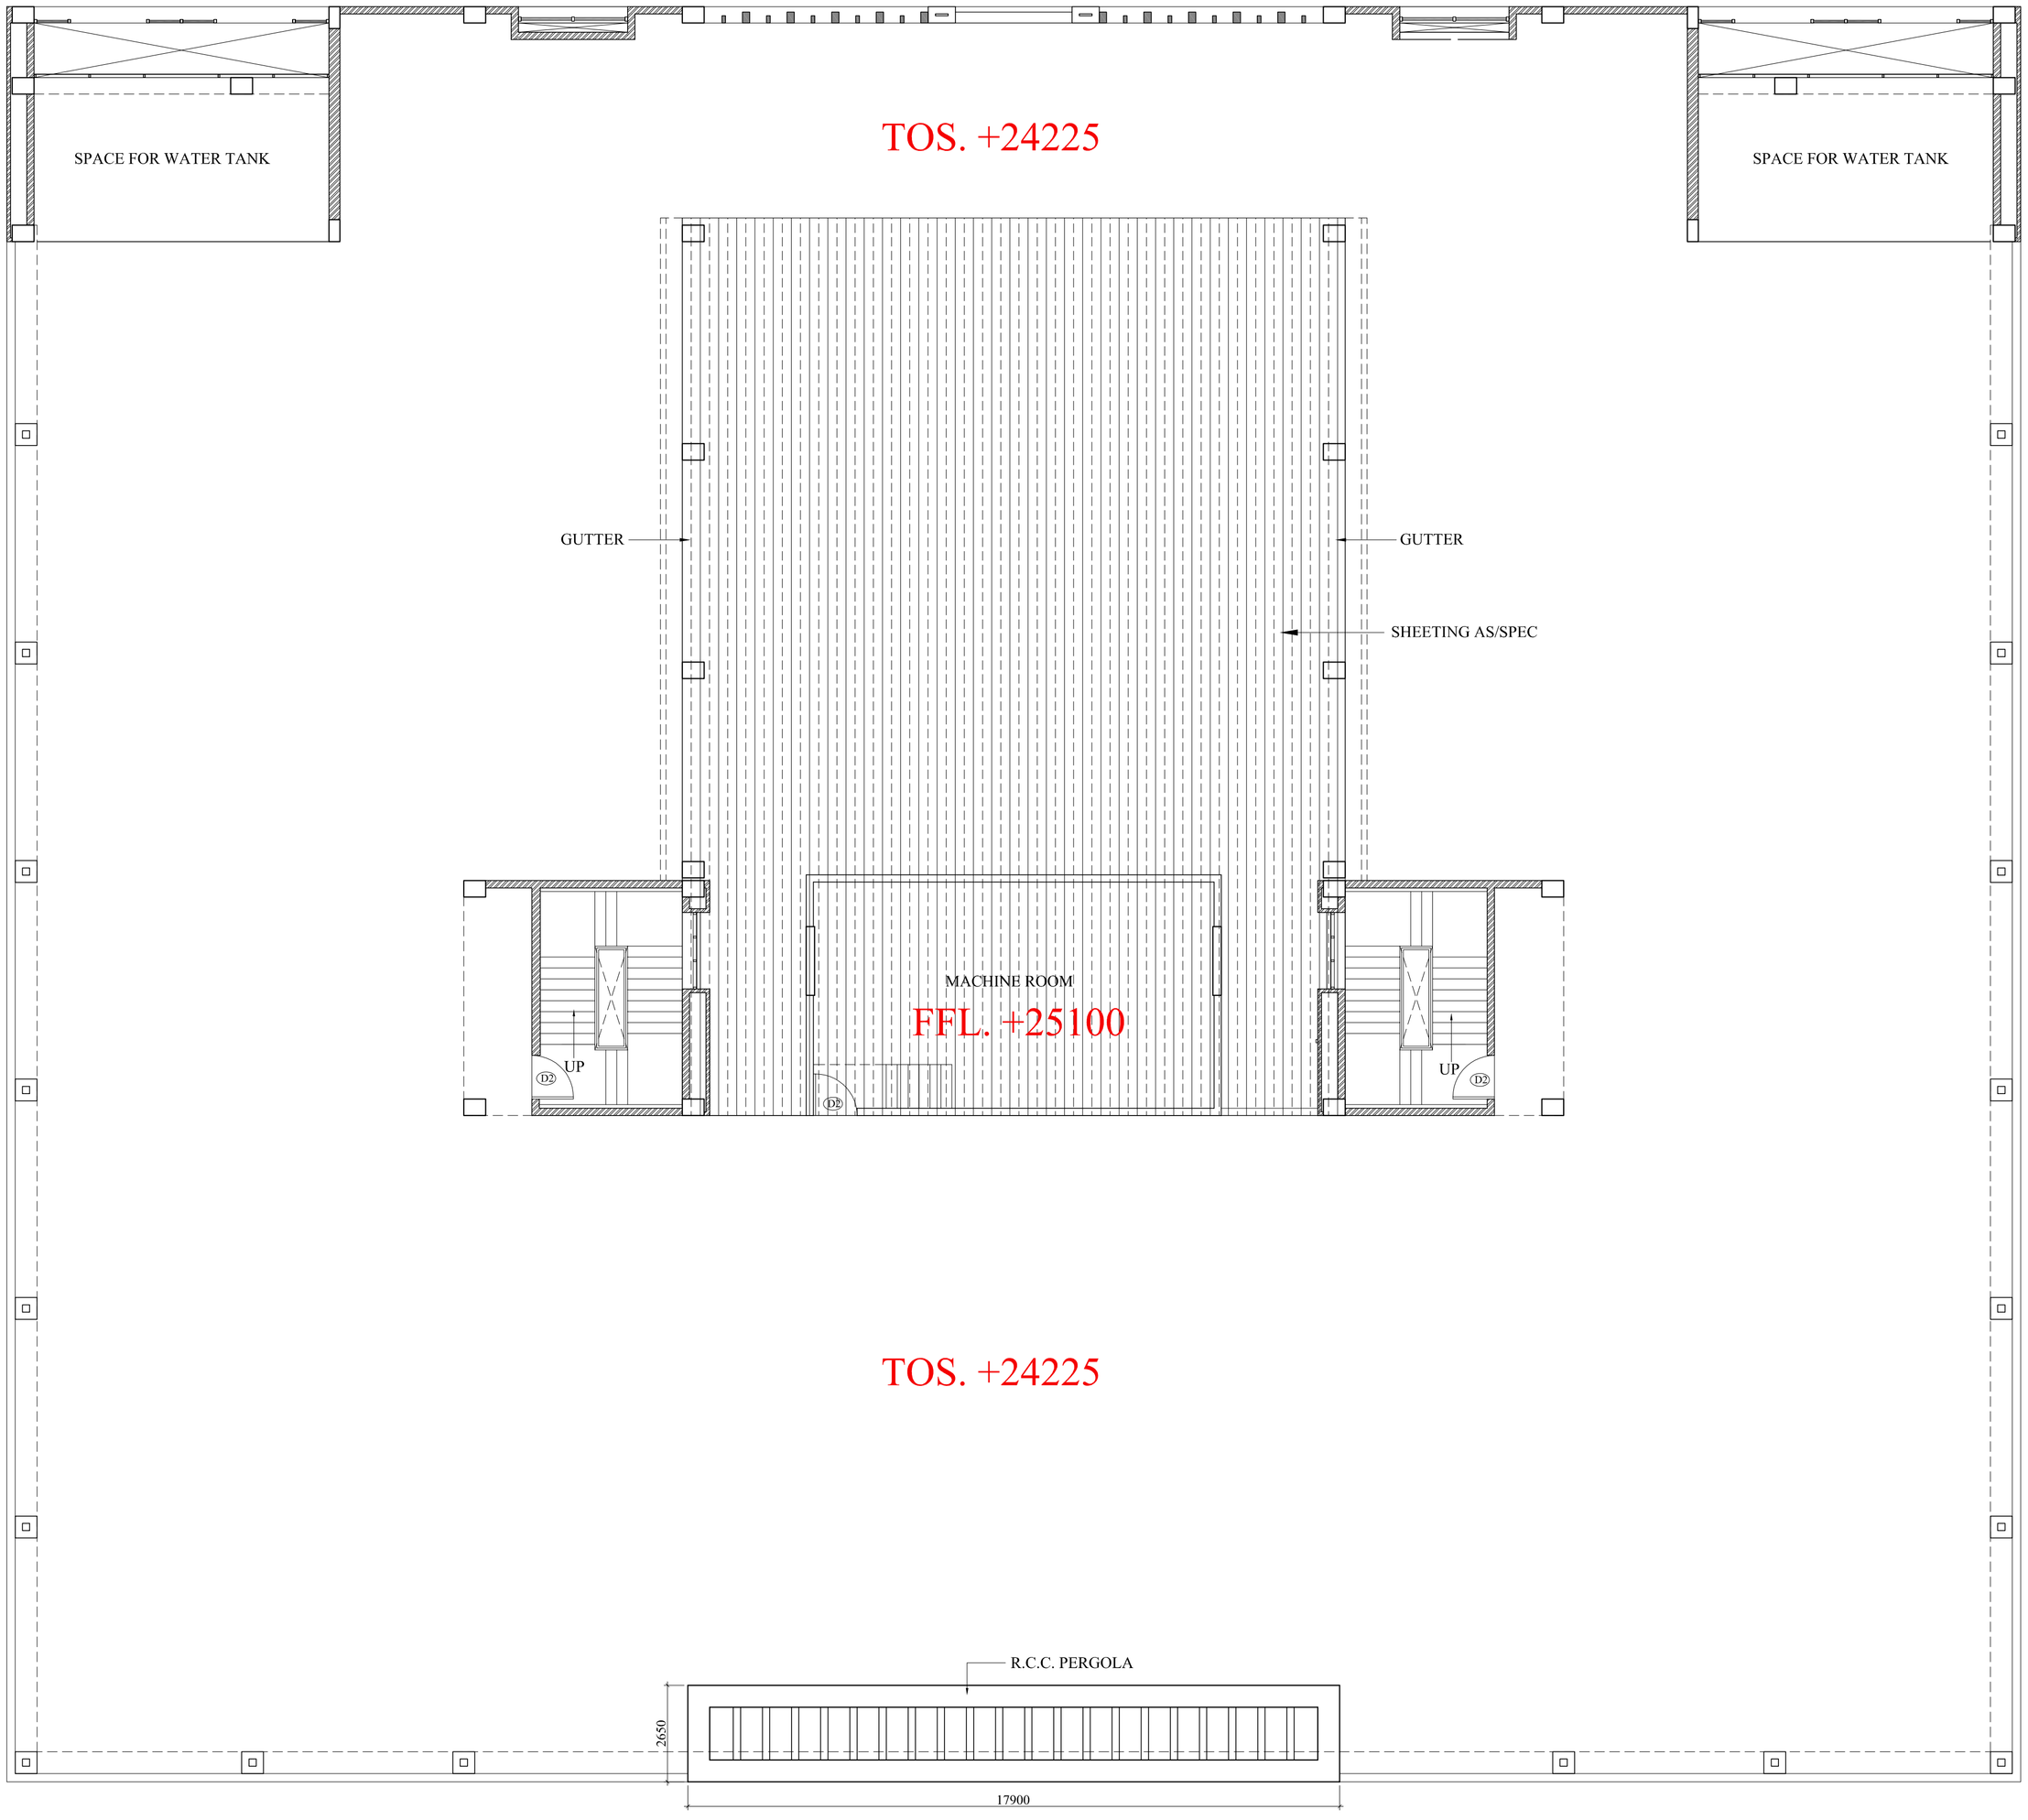

TERRACE PLAN

DOOR-WINDOW OPENING SCHEDULE

S.NO.	TYPE	WIDTH	CILL	LINTEL	DISCRIPTION
01	D1	1500	-------	2400	A.H.U. DOOR
02	D2	1200	-------	2400	STAIRCASE DOOR
03	D3	1200	-------	2400	KITCHEN DOOR
04	D3A	1200	-------	2400	PH TOILET DOOR
05	D4	1000	-------	2400	Swing Door w/vision Panel
06	D5	1000	-------	2400	Door for Toilet,Record etc.
07	D6	750	-------	2100	Attached TOILET DOOR
08	D7	2000	-------	2400	ACOUSTICAL DOOR
09	ED1	1200	-------	2400	ELECTRICAL DOOR
10	ED2	750	100	2100	ELECTRICAL DOOR
11	ED3	2000	-------	2400	ELECTRICAL DOOR
12	FD1	900	100	2100	FHC DOOR
13	GD1	1800	-------	2400	SLIDING Glass Door
14	GD2	1500	-------	2400	Double Panel Swing Glass Door
15	GD3	1000	-------	2400	GLASS DOOR
16	GD4	1000	-------	2400	SWING GLASS DOOR
17	GD5	1200	-------	2400	GLASS DOOR
18	GD5A	1200	-------	2400	SWING GLASS DOOR
19	GD6	1150	-------	2400	SWING GLASS DOOR
20	GD7	1800	-------	2400	AUTOMATIC SLIDING DOOR
21	L1	3000	100	B.O.B.	ALUMINIUM LOUVERS
22	L2	1800	100	B.O.B.	ALUMINIUM LOUVERS
23	L3	1000	100	B.O.B.	ALUMINIUM LOUVERS
24	L3A	2000	100	B.O.B.	ALUMINIUM LOUVERS
25	L4	17000	100	B.O.B.	ALUMINIUM LOUVERS
26	G1	16700	--------	AS/ELE.	Double heightGLAZING
27	G1A	16700	--------	AS/ELE.	Double heightGLAZING
28	G2	17000	--------	AS/ELE	GLAZING
29	G2A	17000	--------	AS/ELE	GLAZING
30	G3	16700	--------	AS/ELE	Triple height GLAZING
31	G4	8100	--------	AS/ELE	GLAZING
32	G5	2100	--------	AS/ELE	GLAZING
33	G5A	2100	--------	AS/ELE	GLAZING
34	G6	1900	--------	AS/ELE	GLAZING
35	G7	4600	--------	AS/ELE	GLAZING
36	G8	2100	--------	AS/ELE	GLAZING
37	G8A	2100	--------	AS/ELE	GLAZING
38	OP	As/Plan	--------	B.O.B.	OPENING

THIS DRAWING IS THE PROPERTY OF THE DESIGN ASSOCIATES INC. AND SHALL NOT BE COPIED OR USED IN ANY MANNER WITHOUT PRIOR PERMISSION.

KEY PLAN

NOTES:

1. ALL DIMENSIONS ARE IN MM.
2. ALL DIMENSIONS ARE TO BE READ AND NOT MEASURED.
3. ALL LEVELS ARE IN METERS.
4. GRID DIMENSIONS AND PLOT LINES ARE TO BE STRICTLY ADHERED TO.
5. ALL LEVELS INCLUDING FLOOR LEVELS, CILL & LINTEL LEVELS, LANDING LEVELS, PARAPET HEIGHT/ LEVELS, LEVELS OF HORIZONTAL PROJECTION & BANDS INCLUDING ANY SURFACE FEATURES INDICATED IN THE DRAWINGS ARE TO BE STRICTLY ADHERED TO.

6. IN CASE OF ANY DISCREPANCY BETWEEN ANY DRAWING, ARCHITECT HAS TO BE INFORMED PRIOR TO ANY EXECUTION.

R2		REVISION
R1		REVISION
GFC		GOOD FOR CONSTRUCTION
AC		ADVANCE COPY
MARK	DATE	DESCRIPTION

OWNER-

GOA SHIPYARD LIMITED
(A Govt. of India Undertaking)
VASCO DA GAMA, GOA, 403802
contactus@goashipyard.com
TEL.No: - (0832) 251252-56, 2512359
FAX No: -(0091-832) 2514232, 2512148

EXECUTING AGENCY-

NBCC (INDIA) LIMITED
(Formerly National Buildings Construction Limited
(A Government of India Enterprise)
NBCC Bhawan, Lodhi Road
New Delhi - 110 003, India
Telephone No : 011 - 24367314 - 17, 24367573
Fax : 011 - 24366995

ARCHITECTS-

DESIGN ASSOCIATES INC.
ARCHITECTURE
A - 163, Sector - 136,
Noida - Greater Noida Expressway,
Noida - 201301, Phone no: 0120-2428600/30
e-mail: matinder.sharma@designassociates.in

MECHANICAL CONSULTANT-
DESIGN CENTER CONSULTING ENGINEERS, NEW DELHI

ELECTRICAL CONSULTANT-
DESIGN CENTER CONSULTING ENGINEERS, NEW DELHI

PLUMBING CONSULTANT-
DESIGN CENTER CONSULTING ENGINEERS, NEW DELHI

STRUCTURE CONSULTANT-
LKT ENGINEERING CONSULTANTS LTD.
10/49, Subhash Nagar,New Delhi-110027
Phone :+011-45565818,Tel/Fax:+011-25126129
info@lktengineering.com
http:-www.lktengineering.com

PROJECT-
CONSTRUCTION OF MCMV OFFICE BUILDING AT GOA SHIPYARD, GOA


DRAWING TITLE-
MUMTY LEVEL FLOOR PLAN

DRAWING PURPOSE-
TENDER DRAWING

JOB NO. -	DWG. REF. NO.-	DATE-
538	----------	----------
SCALE-	REVISION-	DATE OF ISSUE-
1:110	----------	21.12.16

DWG. NO.-
538/GSL/TD/AR/159

	SHEET SIZE-	SHEET NO-
	A1	----------
	DRAWN BY-	CHECKED BY-
	RAJEEV	MATINDER

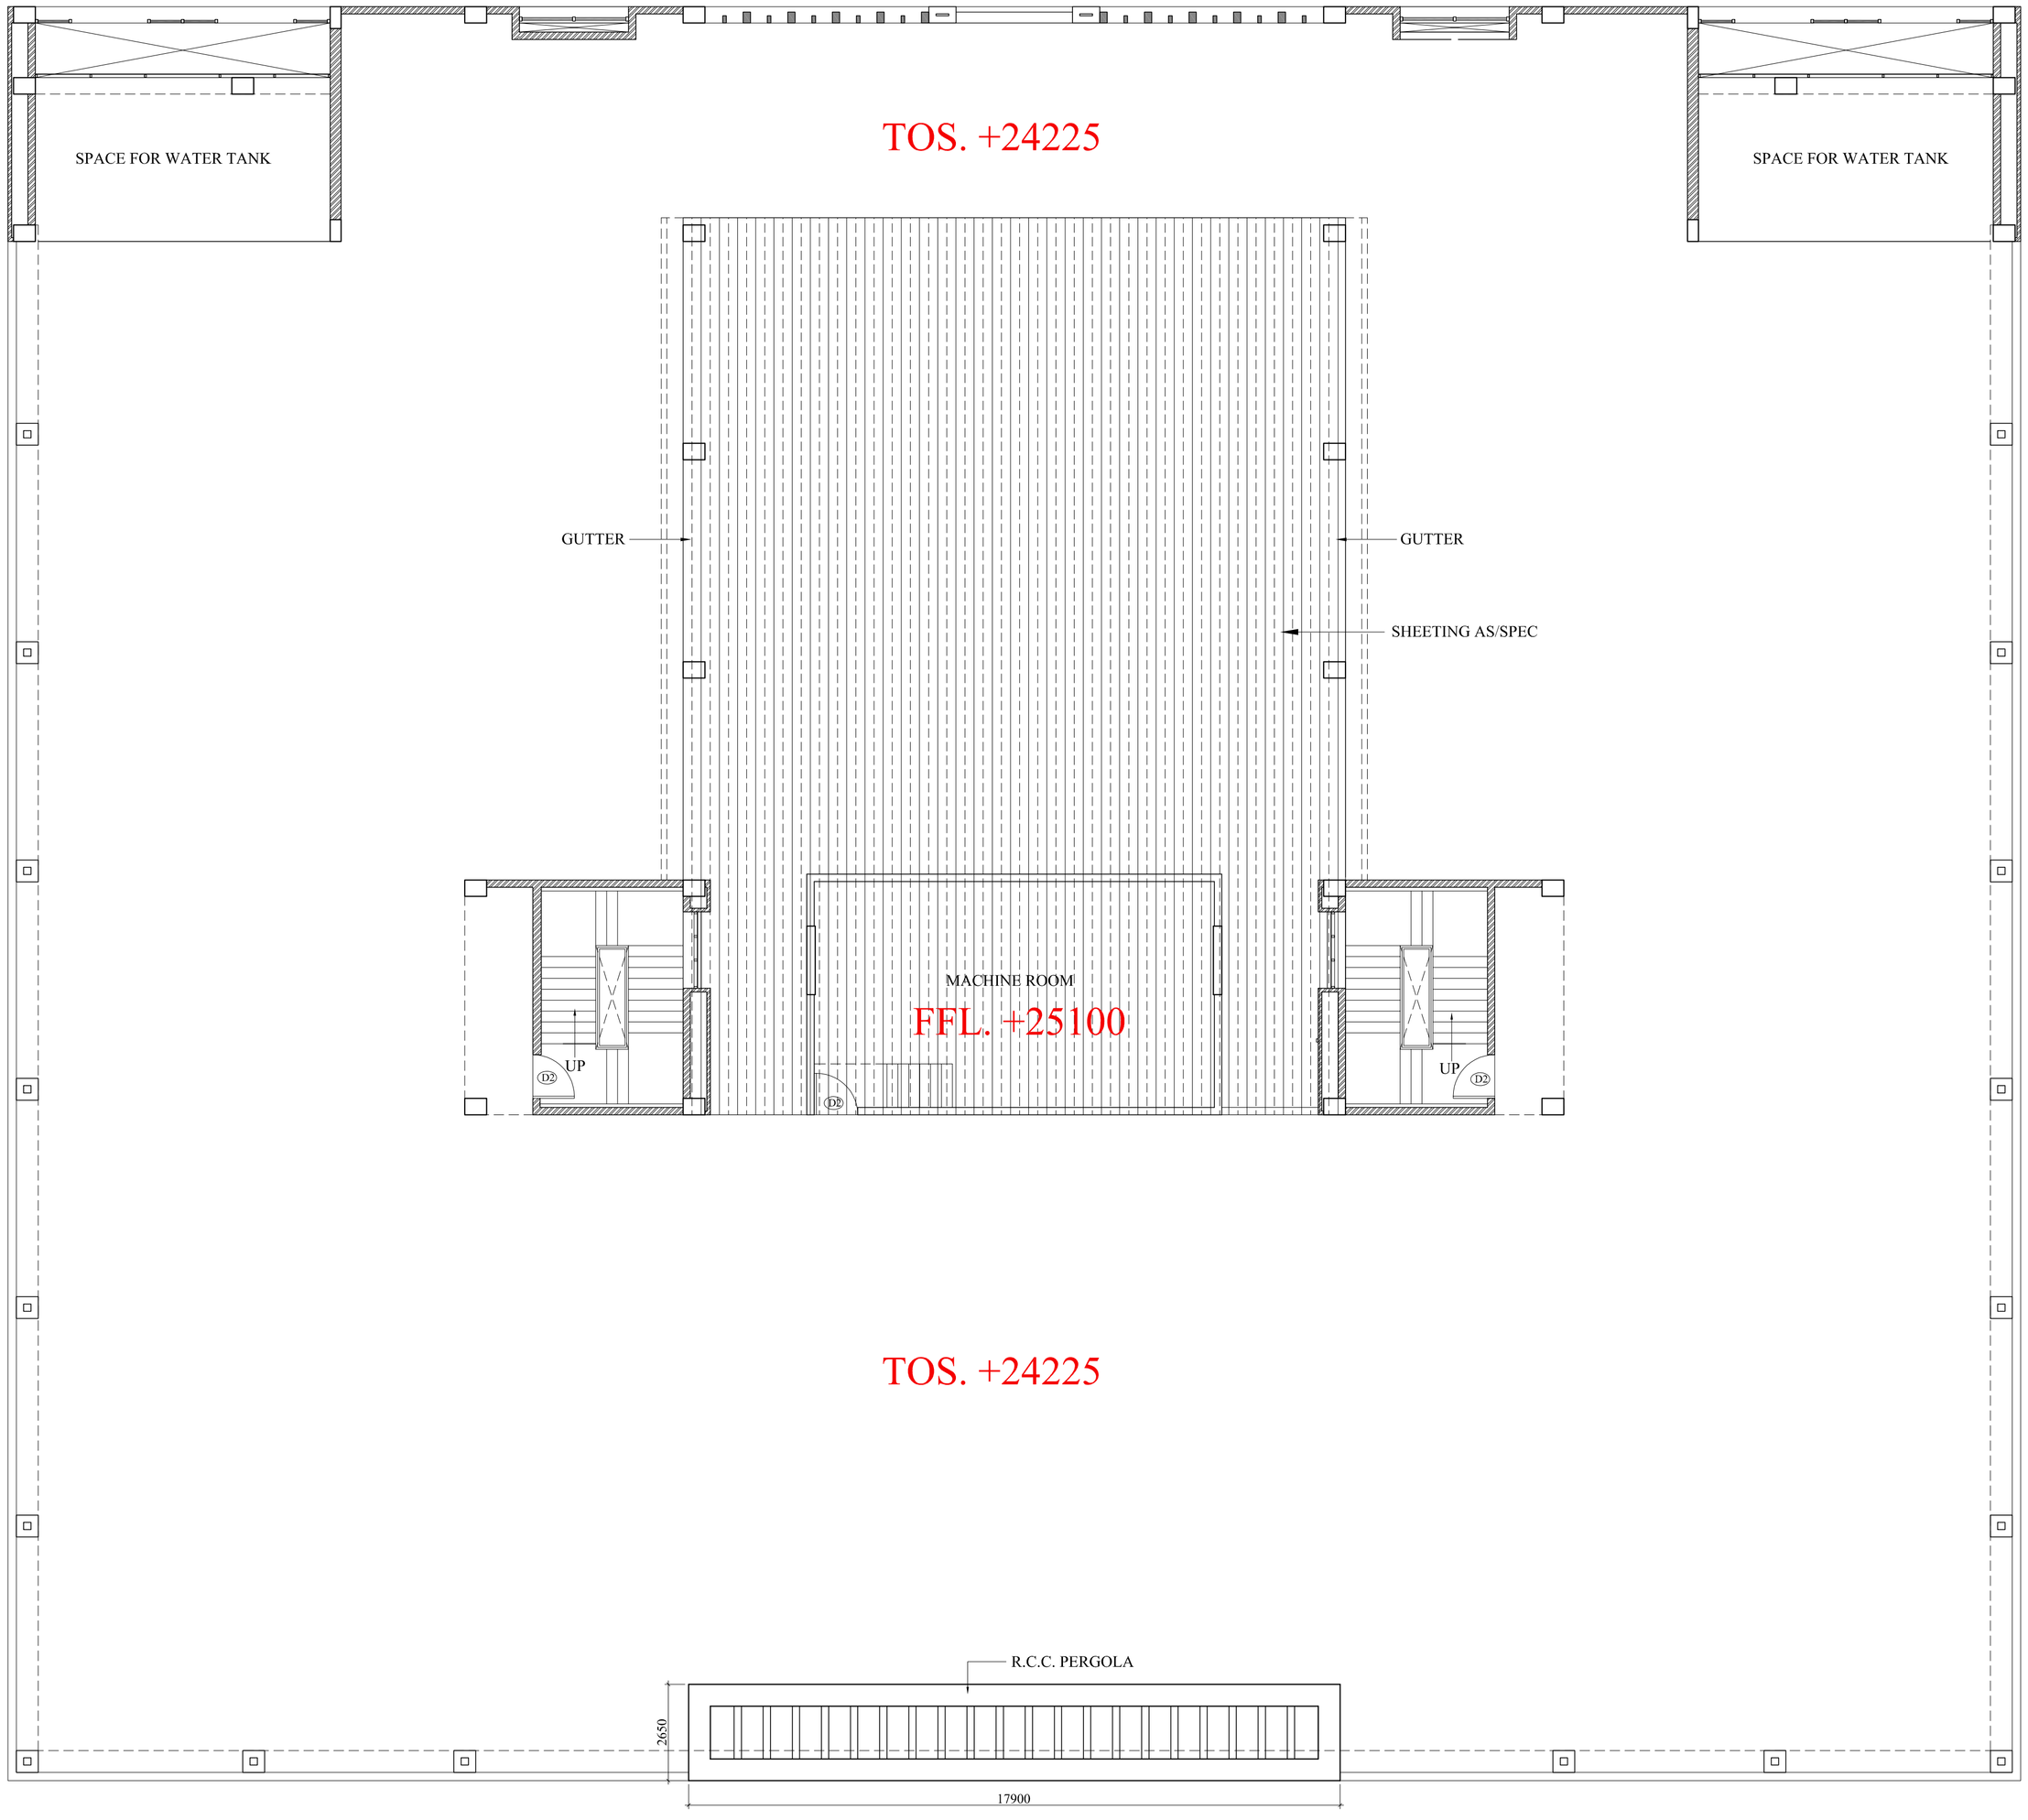

TERRACE PLAN

DOOR-WINDOW OPENING SCHEDULE

S.NO.	TYPE	WIDTH	CILL	LINTEL	DISCRIPTION
01	D1	1500	-------	2400	A.H.U. DOOR
02	D2	1200	-------	2400	STAIRCASE DOOR
03	D3	1200	-------	2400	KITCHEN DOOR
04	D3A	1200	-------	2400	PH TOILET DOOR
05	D4	1000	-------	2400	Swing Door w/vision Panel
06	D5	1000	-------	2400	Door for Toilet,Record etc.
07	D6	750	-------	2100	Attached TOILET DOOR
08	D7	2000	-------	2400	ACOUSTICAL DOOR
09	ED1	1200	-------	2400	ELECTRICAL DOOR
10	ED2	750	100	2100	ELECTRICAL DOOR
11	ED3	2000	-------	2400	ELECTRICAL DOOR
12	FD1	900	100	2100	FHC DOOR
13	GD1	1800	-------	2400	SLIDING Glass Door
14	GD2	1500	-------	2400	Double Panel Swing Glass Door
15	GD3	1000	-------	2400	GLASS DOOR
16	GD4	1000	-------	2400	SWING GLASS DOOR
17	GD5	1200	-------	2400	GLASS DOOR
18	GD5A	1200	-------	2400	SWING GLASS DOOR
19	GD6	1150	-------	2400	SWING GLASS DOOR
20	GD7	1800	-------	2400	AUTOMATIC SLIDING DOOR
21	L1	3000	100	B.O.B.	ALUMINIUM LOUVERS
22	L2	1800	100	B.O.B.	ALUMINIUM LOUVERS
23	L3	1000	100	B.O.B.	ALUMINIUM LOUVERS
24	L3A	2000	100	B.O.B.	ALUMINIUM LOUVERS
25	L4	17000	100	B.O.B.	ALUMINIUM LOUVERS
26	G1	16700	--------	AS/ELE.	Double heightGLAZING
27	G1A	16700	--------	AS/ELE.	Double heightGLAZING
28	G2	17000	--------	AS/ELE	GLAZING
29	G2A	17000	--------	AS/ELE	GLAZING
30	G3	16700	--------	AS/ELE	Triple height GLAZING
31	G4	8100	--------	AS/ELE	GLAZING
32	G5	2100	--------	AS/ELE	GLAZING
33	G5A	2100	--------	AS/ELE	GLAZING
34	G6	1900	--------	AS/ELE	GLAZING
35	G7	4600	--------	AS/ELE	GLAZING
36	G8	2100	--------	AS/ELE	GLAZING
37	G8A	2100	--------	AS/ELE	GLAZING
38	OP	As/Plan	--------	B.O.B.	OPENING

THIS DRAWING IS THE PROPERTY OF THE DESIGN ASSOCIATES INC. AND SHALL NOT BE COPIED OR USED IN ANY MANNER WITHOUT PRIOR PERMISSION.

KEY PLAN

NOTES:

1. ALL DIMENSIONS ARE IN MM.
2. ALL DIMENSIONS ARE TO BE READ AND NOT MEASURED.
3. ALL LEVELS ARE IN METERS.
4. GRID DIMENSIONS AND PLOT LINES ARE TO BE STRICTLY ADHERED TO.
5. ALL LEVELS INCLUDING FLOOR LEVELS, CILL & LINTEL LEVELS, LANDING LEVELS, PARAPET HEIGHT/ LEVELS, LEVELS OF HORIZONTAL PROJECTION & BANDS INCLUDING ANY SURFACE FEATURES INDICATED IN THE DRAWINGS ARE TO BE STRICTLY ADHERED TO.
6. IN CASE OF ANY DISCREPANCY BETWEEN ANY DRAWING, ARCHITECT HAS TO BE INFORMED PRIOR TO ANY EXECUTION.

MARK	DATE	DESCRIPTION
R2		REVISION
R1		REVISION
GFC		GOOD FOR CONSTRUCTION
AC		ADVANCE COPY

OWNER-

GOA SHIPYARD LIMITED
(A Govt. of India Undertaking)
VASCO DA GAMA, GOA, 403802
contactus@goashipyard.com
TEL.No: - (0832) 251252-56, 2512359
FAX No: -(0091-832) 2514232, 2512148

EXECUTING AGENCY-

NBCC (INDIA) LIMITED
(Formerly National Buildings Construction Limited
(A Government of India Enterprise)
NBCC Bhawan, Lodhi Road
New Delhi - 110 003, India
Telephone No : 011 - 24367314 - 17, 24367573
Fax : 011 - 24366995

ARCHITECTS-

DESIGN ASSOCIATES INC.
ARCHITECTURE
A - 163, Sector - 136,
Noida - Greater Noida Expressway,
Noida - 201301, Phone no: 0120-2428600/30
e-mail: matinder.sharma@designassociates.in

MECHANICAL CONSULTANT-
DESIGN CENTER CONSULTING ENGINEERS, NEW DELHI

ELECTRICAL CONSULTANT-
DESIGN CENTER CONSULTING ENGINEERS, NEW DELHI

PLUMBING CONSULTANT-
DESIGN CENTER CONSULTING ENGINEERS, NEW DELHI

STRUCTURE CONSULTANT-
LKT ENGINEERING CONSULTANTS LTD.
10/49, Subhash Nagar,New Delhi-110027
Phone:+011-45565818,Tel/Fax:+011-25126129
info@lktengineering.com
http://www.lktengineering.com

PROJECT-
CONSTRUCTION OF MCMV OFFICE BUILDING AT GOA SHIPYARD, GOA

DRAWING TITLE-
TERRACE FLOOR PLAN

DRAWING PURPOSE-
TENDER DRAWING

JOB NO. -	DWG. REF. NO.-	DATE-
538	----------	----------
SCALE-	REVISION-	DATE OF ISSUE-
1:110	----------	03.01.17

DWG. NO.-
538/GSL/TD/AR/159

	SHEET SIZE-	SHEET NO-
	A1	09
	DRAWN BY-	CHECKED BY-
	RAJEEV	MATINDER