




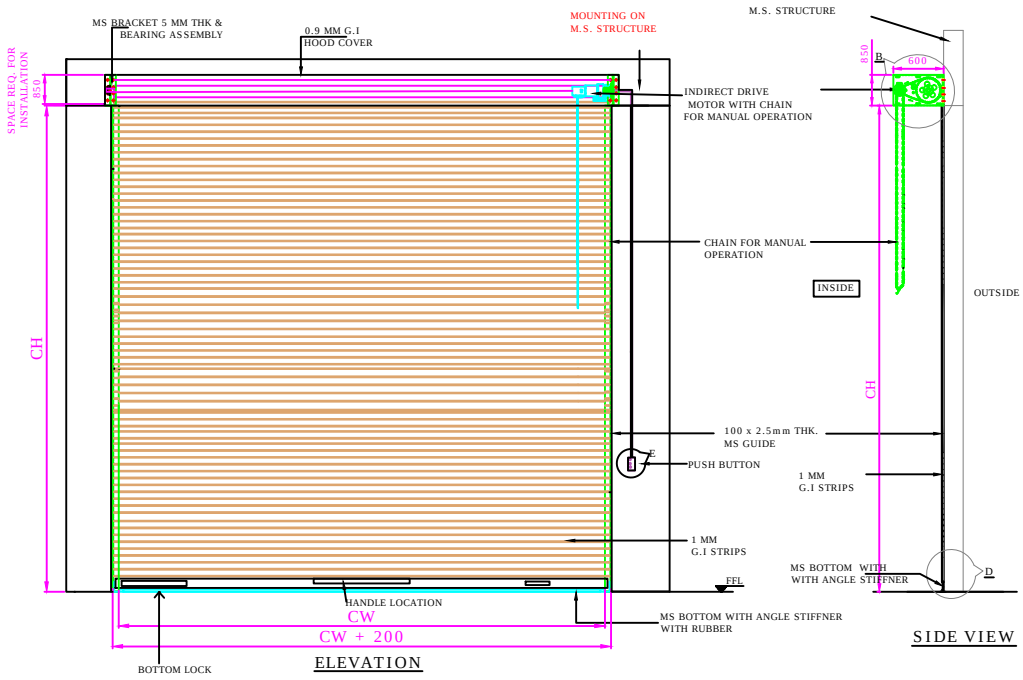


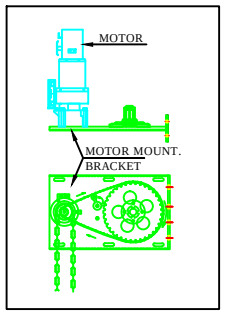

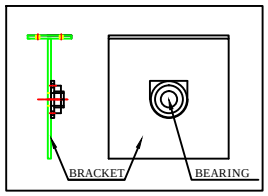

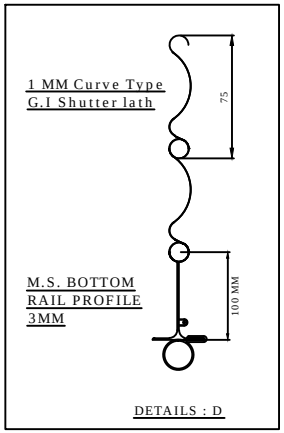

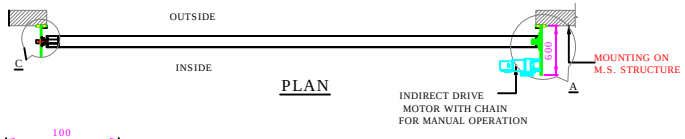

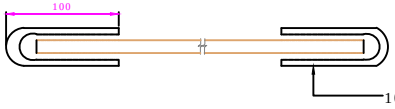

RAL CODE	SHADE	COLOUR
RAL 9001	CREAM	
RAL 9002	GREY WHITE	
RAL 9010	PURE WHITE	
RAL 5002	ULTRAMARINE BLUE	
RAL 7035	LIGHT GREY	
RAL 7001	SILVER GREY	

NOTES-
(1) REQUIRED MS STRUCTURE , FITTING & ALL CIVIL WORK IN CLIENT SCOPE .
(2) SHUTTER WILL BE ONLY INSTALLED AFTER READINESS OF STRUCTURE AS PER DRAWING PROVIDED.
(3) KINDLY REFER RAL SHADE CHART & MENTION RAL SHADE FOR POWDER COATING IN TABLE PROVIDED.

3000	3000	1 NOS		
CLEAR WIDTH (CW)	CLEAR HEIGHT (CH)	QUANTITY	RAL SHADE FOR POWDER COATING	MOTOR SIDE (LH/RH SEEN FROM INSIDE)

This drawing & design is the property of NIHVA TECHNOLOGIES. Not to be sold or copied to any other concern.

TITLE: GI MOTORIZED ROLLING SHUTTER

NIHVA TECHNOLOGIES PVT. LTD.

NIHVA TECHNOLOGIES PVT. LTD. PUNE
Tel : 020 66304033
Email:- info@nihva.com
Website:- www.nihva.com

	NAME	SIGN	DATE
DRAWN	S.M.S.		9.12.2020
CHECK			
APPRD.			

If any queries contact : design@nihva.com

ALL DIMENSION ARE IN mm

CLIENT - A R CONSTRUCTION

PROJECT - MOTORISED ROLLING SHUTTER

SITE LOCATION - PUNE

DWG. NO. : NIHVA/20-21/0057 | REV- R00

SCALE: NTS | WT: | SHEET: