






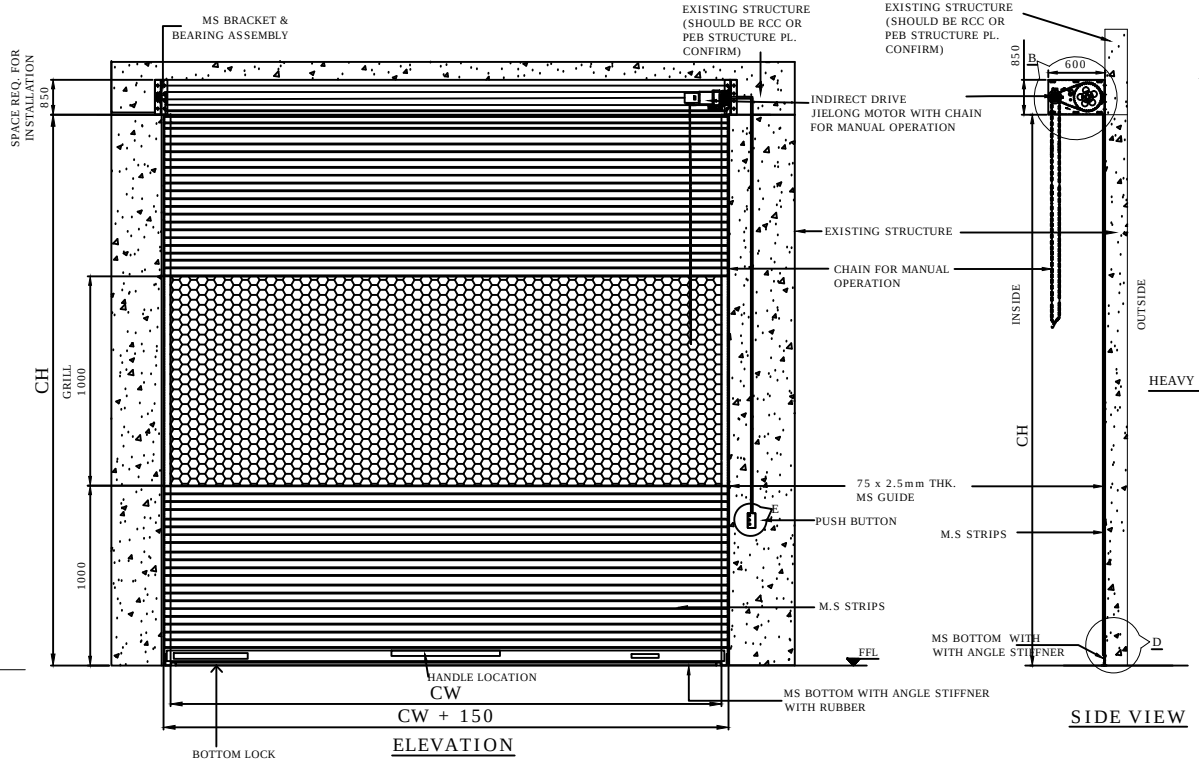


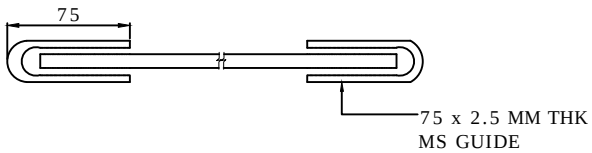

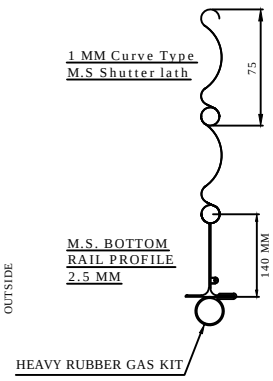

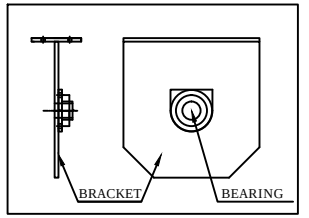

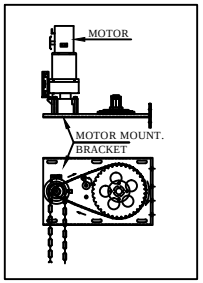

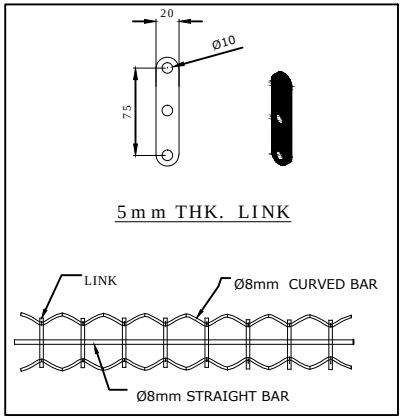

SR NO	LOCATION	TYPE	CLEAR WIDTH	NEW CLEAR HEIGHT	QTY	SIDE WALL/ SUPPORTING STRUCTURE
2	OUTGOING SHED	RS1	4000	4660	1	PEB
1	INCOMING SHED	RS1	4000	4660	1	PEB

NOTE :
1. WE ARE USING EXISTING SUPPLIED 4000W X 3660H SHUTTER MATERIAL ON SITE.
2. FOR INCREASING 1000 MM HEIGHT REQ. MATERIAL WILL BE SUPPLY BY NIHVA.

This drawing & design is the property of NIHVA TECHNOLOGIES. Not to be sold or copied to any other concern.

TITLE: MOTORIZED ROLLING SHUTTER

	NAME	SIGN	DATE
DRAWN	P.A		07.10.2020
CHECK	G.J		07.10.2020
APPRD.			

NIHVA TECHNOLOGIES PVT. LTD.
NIHVA TECHNOLOGIES PVT. LTD. PUNE
Tel : 020 66304033
Email:- info@nihva.com
Website:- www.nihva.com

CLIENT - DESAI CONSTRUCTION
PROJECT - GE LOCOMOTIVE
SITE LOCATION - GUJARAT

If any queries contact : design@nihva.com
DWG. NO. : NIHVA/20-21/0061
REV- R00

ALL DIMENSION ARE IN mm
SCALE: NTS
WT:
SHEET: