

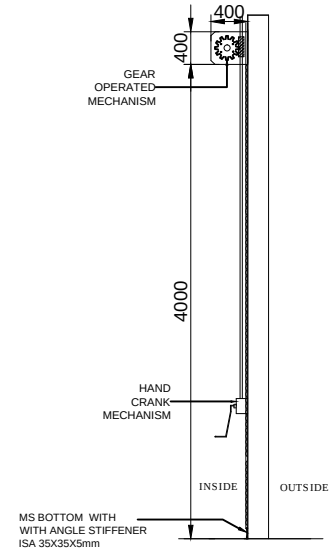



SIDE VIEW

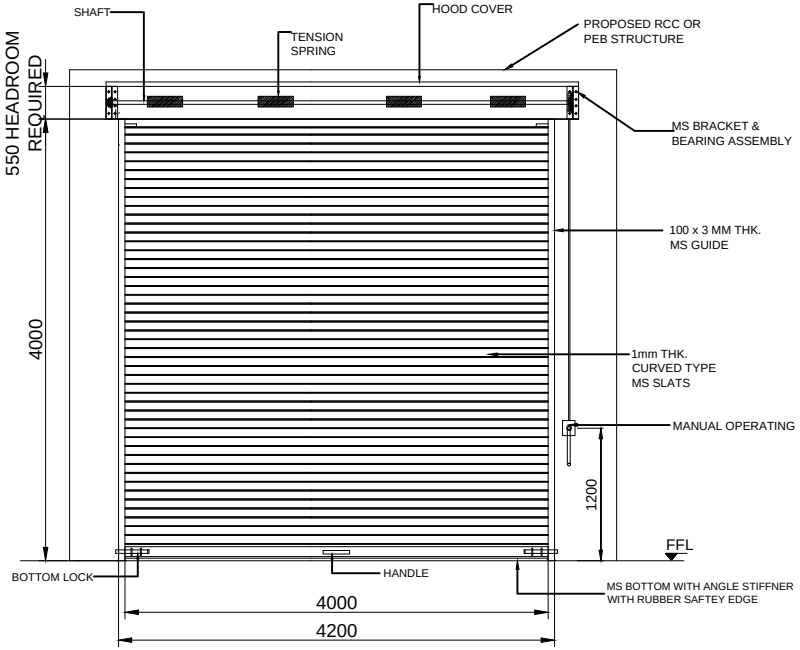

INSIDE ELEVATION

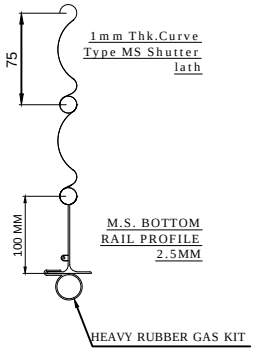

M.S. BOTTOM RAIL PROFILE 2.5MM

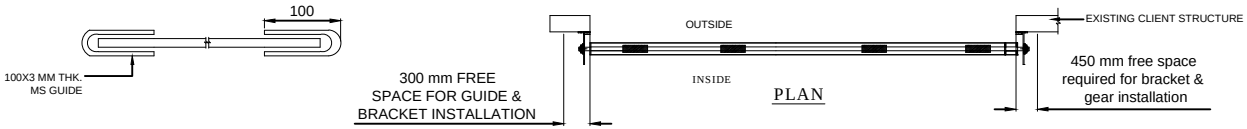

PLAN

TOLERANCE - ±10mm

S.N.	LOCATION	SIZE	QUANTITY
1	-	4000(W)X4000(H)	04
TOTAL QTY. OF SHUTTER			04

NOTE-
1. ALL CIVIL WORK WILL BE CLIENT'S SCOPE.
2.STRUCTURE REQUIRED FOR SHUTTER IS IN CLIENT'S SCOPE.

This drawing & design is the property of NIHVA TECHNOLOGIES. Not to be sold or copied to any other concern.

TITLE
GEAR OPERATED ROLLING SHUTTER 4mX4m

NIHVA TECHNOLOGIES PVT. LTD.
NIHVA TECHNOLOGIES PVT. LTD. PUNE
Tel : 020 66304033
Email:- info@nihva.com
Website:- www.nihva.com

	NAME	SIGN	DATE
DRAWN	SURAJ		07.07.2018
CHECK	PRADEEP		07.07.2018
APPRD.	R.D		07.07.2018

CLIENT - REWARD CONSTRUCTIONS PVT LTD.
PROJECT - REWARD CONSTRUCTIONS PVT LTD.
SITE LOCATION - RANJANGAON MIDC.
If any queries contact : design@nihva.com
DWG. NO. : NIHVA/18-19/0075 REV- 0
ALL DIMENSION ARE IN mm
SCALE: NTS WT: SHEET: 01 OF 01