

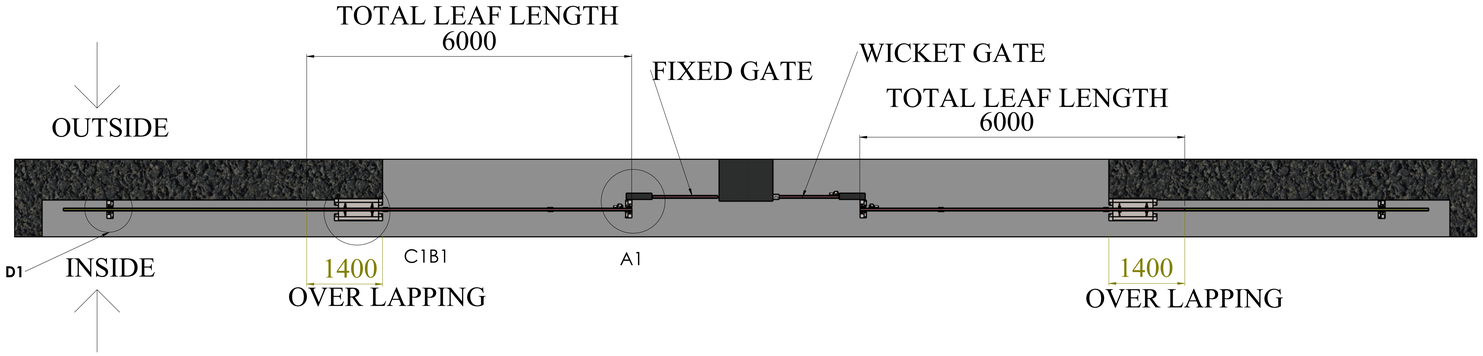


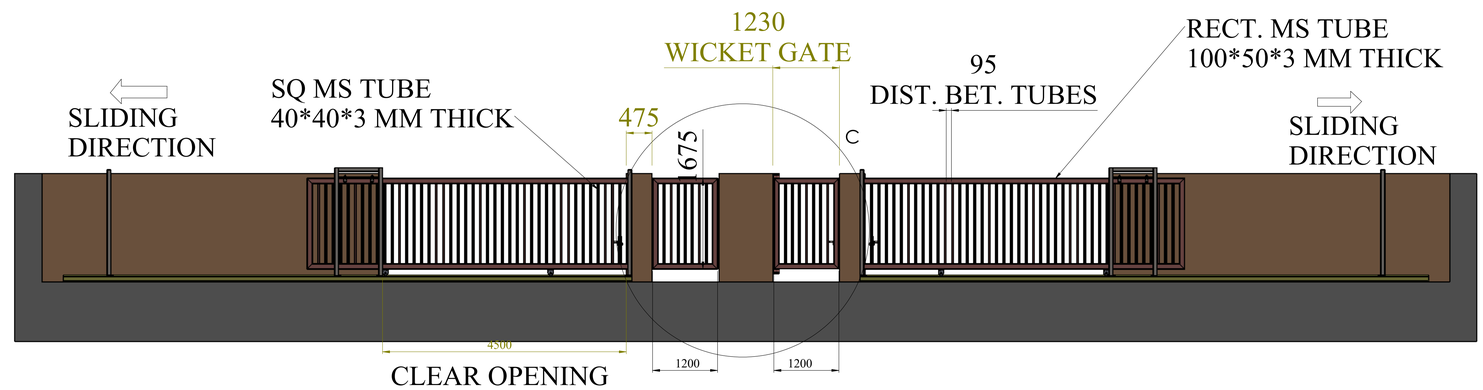


CLEAR OPENING

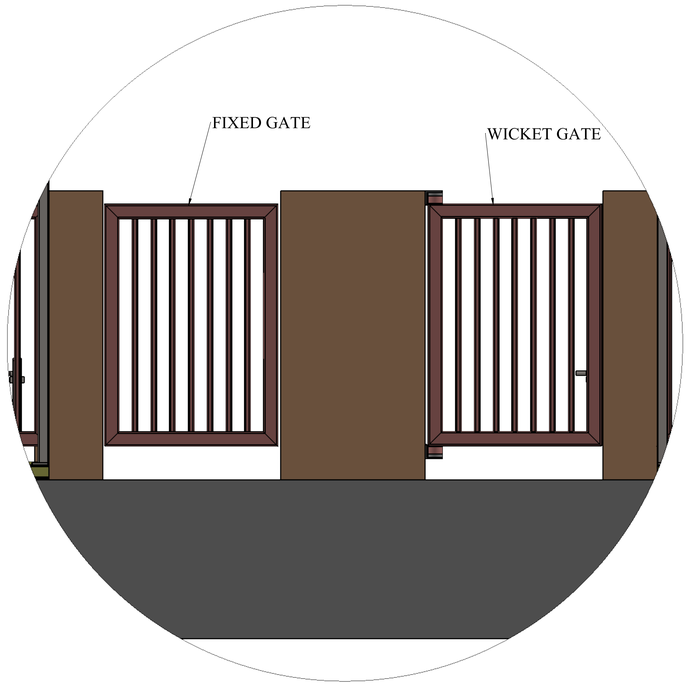


FIXED GATE AND SWING GATE VIEW

DETAIL C
SCALE 1 : 15

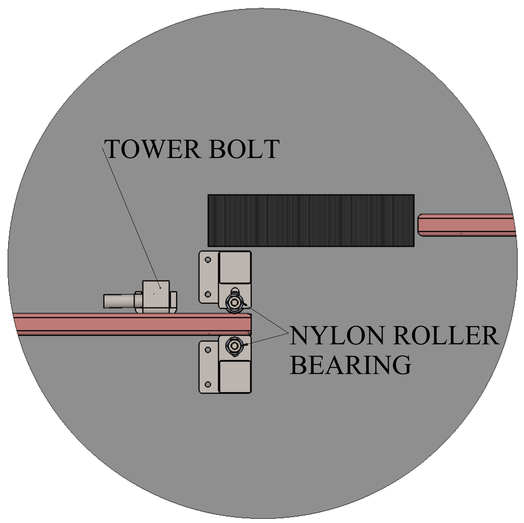


POST 1 AND NYLON ROLLER BEARING ASSEM.

DETAIL A1
SCALE 1 : 5

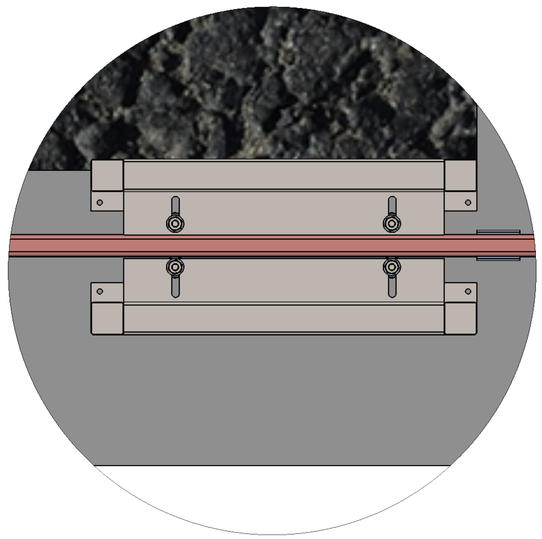

POST 2 AND NYLON ROLLER BEARING ASSEM.

DETAIL C1B1
SCALE 1 : 5

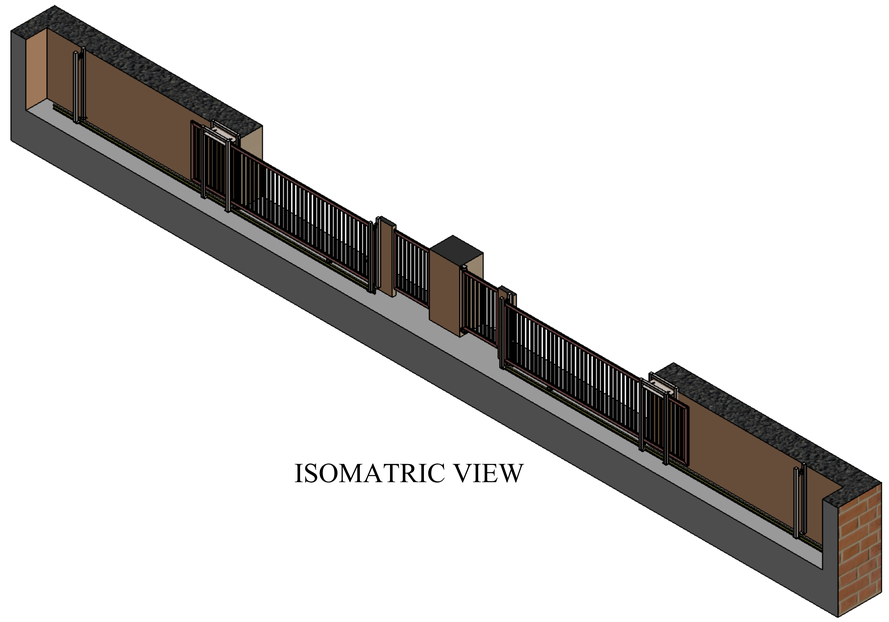

ISOMATRIC VIEW

Note : - 1)dwg no 4
2) barbed wire is not menstion in this dwg.
3)Total column -04 (A1,B1,C1,D1)
4) 03 column posts when the gates is in the closed position.(A1,B1,C1)
5) 03 column posts when the gates is in the fully open position.(B1,C1,D1)

UNLESS OTHERWISE SPECIFIED: DIMENSIONS ARE IN MILLIMETERS SURFACE FINISH: TOLERANCES: LINEAR: ANGULAR:					FINISH:	DEBURR AND BREAK SHARP EDGES	DO NOT SCALE DRAWING / REVISION
	NAME	SIGNATURE	DATE				TITLE:
DRAWN							
CHK'D							
APPV'D							
MFG							
Q.A							
					MATERIAL:		DWG NO. SBFINAL ASSM. GA DRAWING / REV
					WEIGHT:		SCALE:1:100 / SHEET 1 OF 1